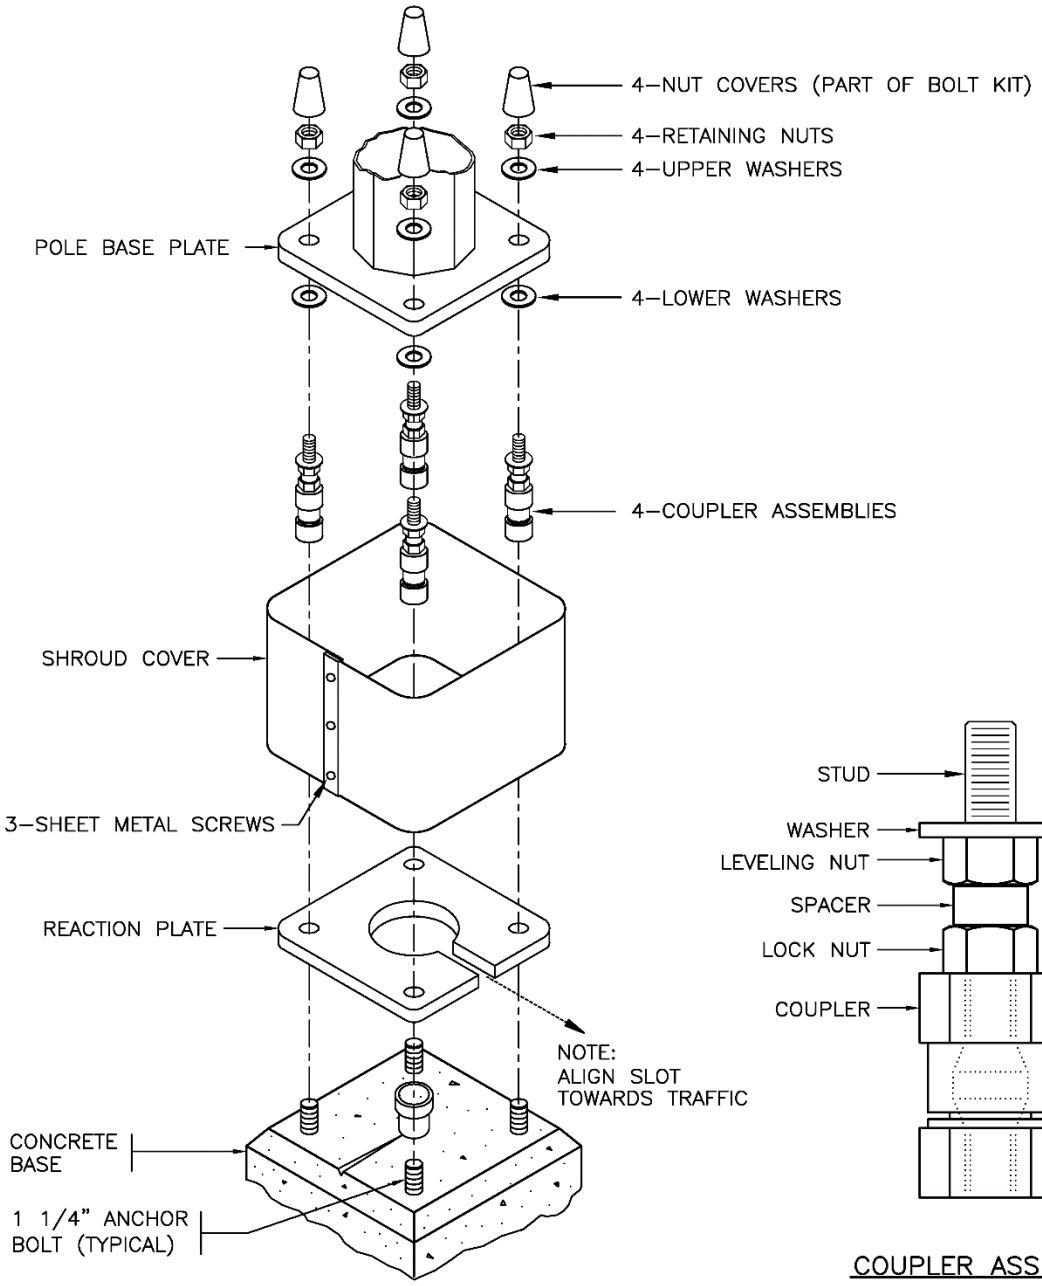


BREAKAWAY BASE ASSEMBLY

COUPLER ASSEMBLY

NOTES:

1. SEE STANDARD SPECIFICATIONS & SPECIAL PROVISIONS FOR ADDITIONAL INFORMATION.
2. INSTALL BASE AND TIGHTEN BOLTS AS PER MANUFACTURERS INSTRUCTIONS.

NOT TO SCALE


BRITISH COLUMBIA | Ministry of Transportation and Infrastructure

No.	Revision	Date
F		
E		
D		
C	GENERAL REVISIONS	APR 17
B	NOTE 2, COUPLERS & REACTION PLATE REV'D	JAN 97
A	GENERAL REVISIONS	AUG 94

BREAKAWAY BASE
FOR 13.5 m LUMINAIRE POLES

Date Approved
30/09/93 E.L. (Signature on File)
Chief Highway Engineer

SPECIFICATION DRAWING No.
SP635–2.1.16

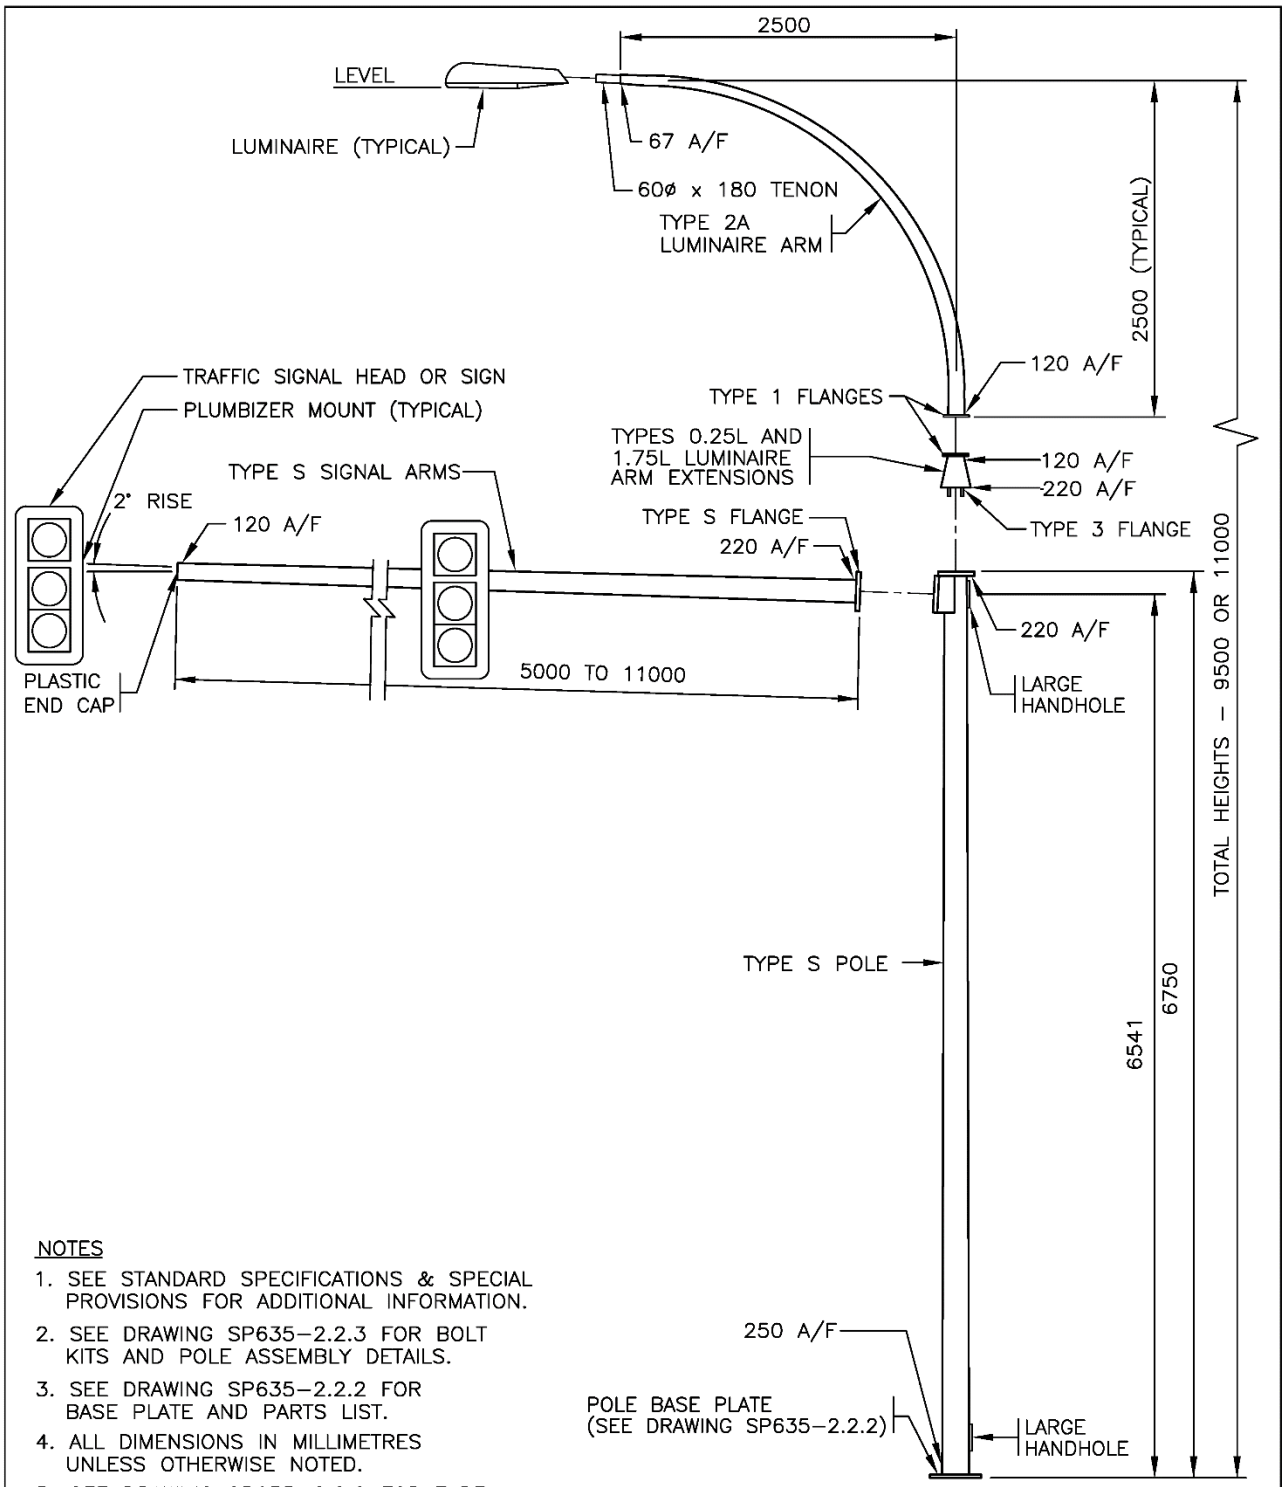

NOTES

1. SEE STANDARD SPECIFICATIONS & SPECIAL PROVISIONS FOR ADDITIONAL INFORMATION.
2. SEE DRAWING SP635–2.2.3 FOR BOLT KITS AND POLE ASSEMBLY DETAILS.
3. SEE DRAWING SP635–2.2.2 FOR BASE PLATE AND PARTS LIST.
4. ALL DIMENSIONS IN MILLIMETRES UNLESS OTHERWISE NOTED.
5. SEE DRAWING SP635–2.2.2 FOR TYPE 2C LUMINAIRE ARM DETAILS.

NOT TO SCALE


BRITISH COLUMBIA | Ministry of Transportation and Infrastructure

No.	Revision	Date
E		
D		
C	GENERAL REVISIONS AND NEW DRAWING NUMBER	APR 20
B	GENERAL REVISIONS	APR 17
A	NEW DRAWING–PREVIOUS DRAWING 2.2.7 TO MOVED TO 2.2.10	OCT 03


TYPE S SIGNAL POLE INSTALLATION DETAILS

Date: **14/11/03** Approved: **D.N. (Signature on File)** Chief Engineer

SPECIFICATION DRAWING No. SP635–2.2.1

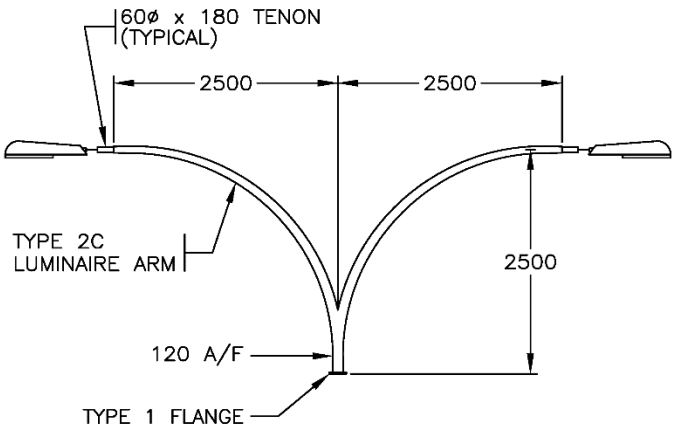

TYPE 2C LUMINAIRE ARM DETAILS

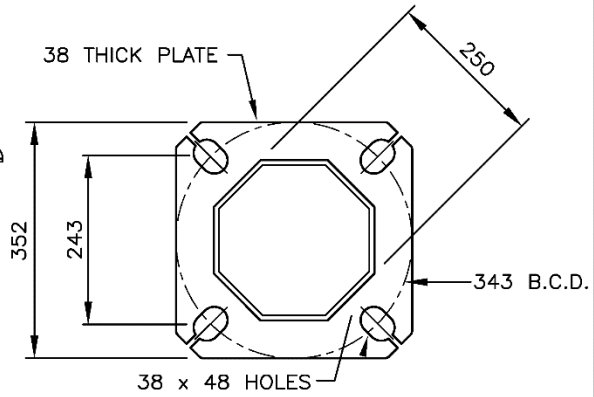

TYPE S POLE BASE PLATE

PARTS LIST FOR TYPE S SIGNAL POLE	
PART	MASS (kg)
TYPE [S] POLE	385
TYPE [5S] SIGNAL ARM – 5.0m	104
TYPE [5.5S] SIGNAL ARM – 5.5m	111
TYPE [6S] SIGNAL ARM – 6.0m	118
TYPE [6.5S] SIGNAL ARM – 6.5m	125
TYPE [7S] SIGNAL ARM – 7.0m	132
TYPE [7.5S] SIGNAL ARM – 7.5m	192
TYPE [8S] SIGNAL ARM – 8.0m	204
TYPE [8.5S] SIGNAL ARM – 8.5m	214
TYPE [9S] SIGNAL ARM – 9.0m	224
TYPE [9.5S] SIGNAL ARM – 9.5m	292
TYPE [10S] SIGNAL ARM – 10.0m	306
TYPE [10.5S] SIGNAL ARM – 10.5m	320
TYPE [11S] SIGNAL ARM – 11.0m	340
TYPE [1.75L] LUMINAIRE ARM EXTENSION – 1.75m	29
TYPE [0.25L] LUMINAIRE ARM EXTENSION – 0.25m	10
TYPE [2A] LUMINAIRE ARM	35
TYPE [2C] LUMINAIRE ARM	65
TYPE 1 FLANGE COVER PLATE [1 FCP]	1.5
TYPE S FLANGE COVER PLATE [S FCP]	3
TYPE 3 FLANGE COVER PLATE [3 FCP]	4
POST TOP TENON [PTT]	5

* [ ] I.D. LABEL ON POLE

BRITISH COLUMBIA Ministry of Transportation and Infrastructure


NOT TO SCALE

No.	Revision	Date
F		
E		
D		
C		
B	NEW DRAWING NUMBER	APR 20
A	GENERAL REVISIONS	APR 17

TYPE S SIGNAL POLE INSTALLATION DETAILS

Date: **14/11/03** Approved: **D.N. (Signature on File)** Chief Engineer

SPECIFICATION DRAWING No. SP635–2.2.2

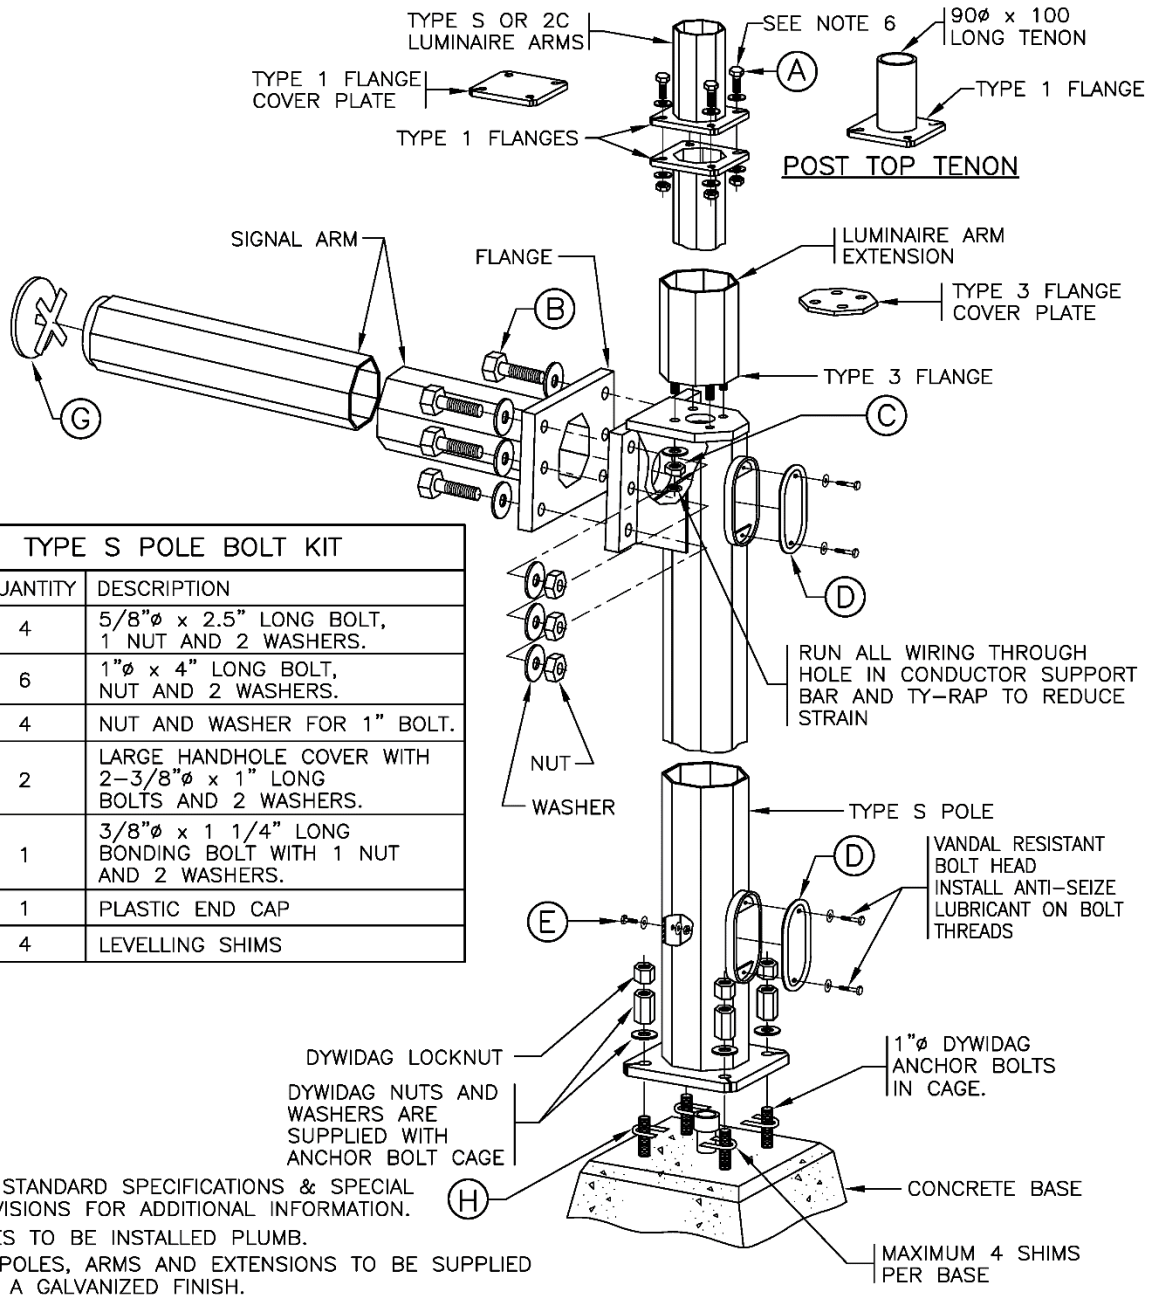

POLE ASSEMBLY DETAIL

TYPE S POLE BOLT KIT		
ITEM	QUANTITY	DESCRIPTION
A	4	5/8"ø x 2.5" LONG BOLT, 1 NUT AND 2 WASHERS.
B	6	1"ø x 4" LONG BOLT, NUT AND 2 WASHERS.
C	4	NUT AND WASHER FOR 1" BOLT.
D	2	LARGE HANDHOLE COVER WITH 2-3/8"ø x 1" LONG BOLTS AND 2 WASHERS.
E	1	3/8"ø x 1 1/4" LONG BONDING BOLT WITH 1 NUT AND 2 WASHERS.
G	1	PLASTIC END CAP
H	4	LEVELLING SHIMS

NOTES

1. SEE STANDARD SPECIFICATIONS & SPECIAL PROVISIONS FOR ADDITIONAL INFORMATION.
2. POLES TO BE INSTALLED PLUMB.
3. ALL POLES, ARMS AND EXTENSIONS TO BE SUPPLIED WITH A GALVANIZED FINISH.
4. APPLY GREASE TO ANCHOR BOLT THREADS.
5. TOUCH UP ANY SCRATCHES IN GALVANIZED SURFACES WITH COLD GALVANIZING COMPOUND.
6. BOLT, WASHERS, AND SINGLE NUT SHALL CONFORM TO ASTM F3125 GRADE A325. GRADE SAE 5 BOLTS WITH THE FOLLOWING SPECIFICATIONS MAY BE SUBSTITUTED: 5/8" DIAMETER, 3" LENGTH, 2 WASHERS, AND 2 NUTS. CONNECTION INSTALLATION TO BE IN ACCORDANCE WITH "TURN-OF-NUT" METHOD SPECIFIED IN CSA S6.

BRITISH COLUMBIA | Ministry of Transportation and Infrastructure


NOT TO SCALE

No.	Revision	Date
F		
E		
D		
C	GENERAL REVISIONS AND NEW DRAWING NUMBER	APR 20
B	GENERAL REVISIONS	APR 17
A	TYPE 1 FLANGE BOLTS CHANGED TO A325	DEC 10

TYPE S SIGNAL POLE INSTALLATION DETAILS

Date: **14/11/03** Approved: **D.N. (Signature on File)** Chief Engineer

SPECIFICATION DRAWING No. SP635-2.2.3

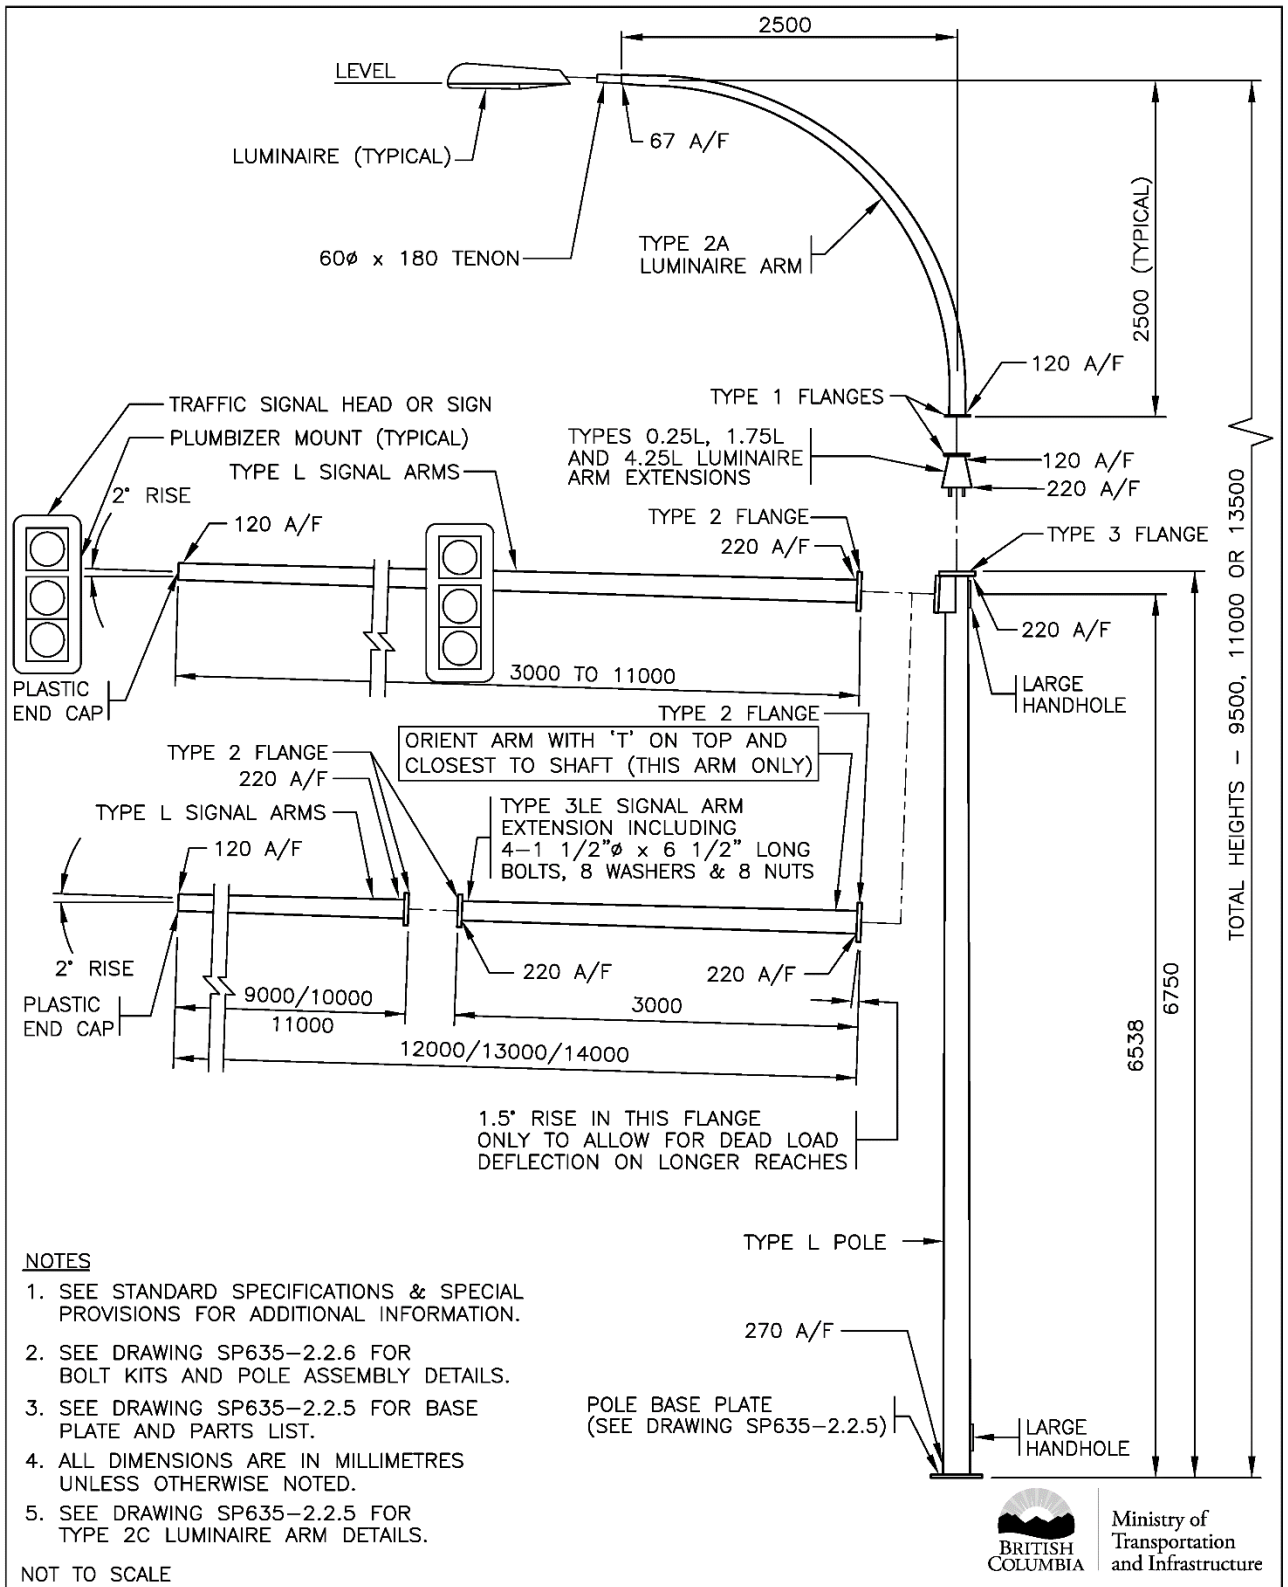

NOTES

1. SEE STANDARD SPECIFICATIONS & SPECIAL PROVISIONS FOR ADDITIONAL INFORMATION.
2. SEE DRAWING SP635–2.2.6 FOR BOLT KITS AND POLE ASSEMBLY DETAILS.
3. SEE DRAWING SP635–2.2.5 FOR BASE PLATE AND PARTS LIST.
4. ALL DIMENSIONS ARE IN MILLIMETRES UNLESS OTHERWISE NOTED.
5. SEE DRAWING SP635–2.2.5 FOR TYPE 2C LUMINAIRE ARM DETAILS.

NOT TO SCALE


BRITISH COLUMBIA — Ministry of Transportation and Infrastructure

No.	Revision	Date
F	GENERAL REVISIONS AND NEW DRAWING NUMBER	APR 20
E	GENERAL REVISIONS	APR 17
D	SIGNAL HEAD MOUNTING ADDED	OCT 03
C	BOLTS ON EXTENSION ARM REVISED	AUG 96
B	NOTE 5 ADDED & 3LE ARM REVISED	AUG 95
A	GENERAL REVISIONS	AUG 94


TYPE L SIGNAL POLE INSTALLATION DETAILS

Date: **30/09/93** Approved: **E.L.** **(Signature on File)**
Chief Highway Engineer

SPECIFICATION DRAWING No.
SP635–2.2.4

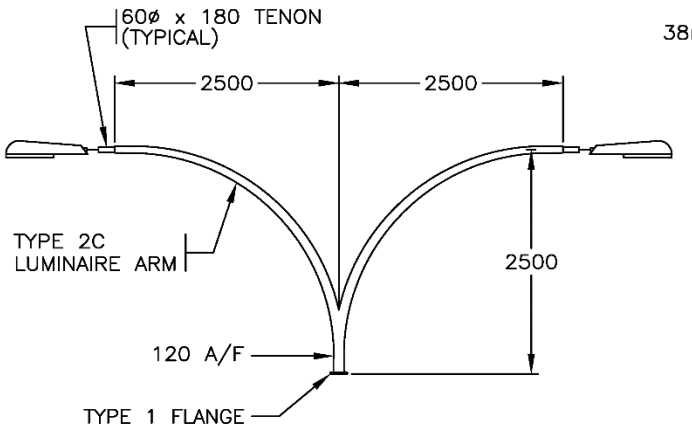

TYPE 2C LUMINAIRE ARM DETAILS

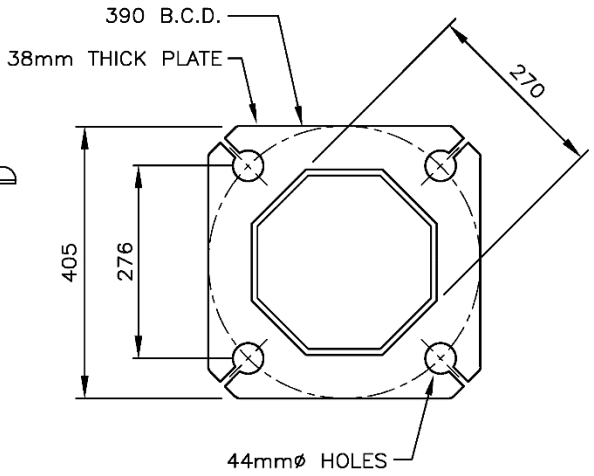

TYPE L POLE BASE PLATE

PARTS LIST FOR TYPE L SIGNAL POLE	
PART	MASS (kg)
TYPE [L] POLE	442
TYPE [3L] SIGNAL ARM – 3.0m	97
TYPE [4L] SIGNAL ARM – 4.0m	118
TYPE [5L] SIGNAL ARM – 5.0m	173
TYPE [6L] SIGNAL ARM – 6.0m	201
TYPE [7L] SIGNAL ARM – 7.0m	229
TYPE [8L] SIGNAL ARM – 8.0m	259
TYPE [9L] SIGNAL ARM – 9.0m	284
TYPE [10L] SIGNAL ARM – 10.0m	377
TYPE [11L] SIGNAL ARM – 11.0m	410
TYPE [3LE] SIGNAL ARM EXTENSION – 3.0m	114
TYPE [4.25L] LUMINAIRE ARM EXTENSION – 4.25m	82
TYPE [1.75L] LUMINAIRE ARM EXTENSION – 1.75m	29
TYPE [0.25L] LUMINAIRE ARM EXTENSION – 0.25m	10
TYPE [2A] LUMINAIRE ARM	35
TYPE [2C] LUMINAIRE ARM	65
TYPE 1 FLANGE COVER PLATE [1 FCP]	1.5
TYPE 2 FLANGE COVER PLATE [2 FCP]	4
TYPE 3 FLANGE COVER PLATE [3 FCP]	4
POST TOP TENON [PTT]	5

* [ ] I.D. LABEL ON POLE

NOT TO SCALE

BRITISH COLUMBIA | Ministry of Transportation and Infrastructure

No.	Revision	Date
F		
E		
D	NEW DRAWING NUMBER	APR 20
C	GENERAL REVISIONS	APR 17
B	HOLE SIZE REVISED & 2C ARM ADDED	AUG 95
A	GENERAL REVISIONS	AUG 94

TYPE L SIGNAL POLE INSTALLATION DETAILS


Date Approved

30/09/93 E.L. (Signature on File)

Chief Highway Engineer

SPECIFICATION DRAWING No.

SP635–2.2.5

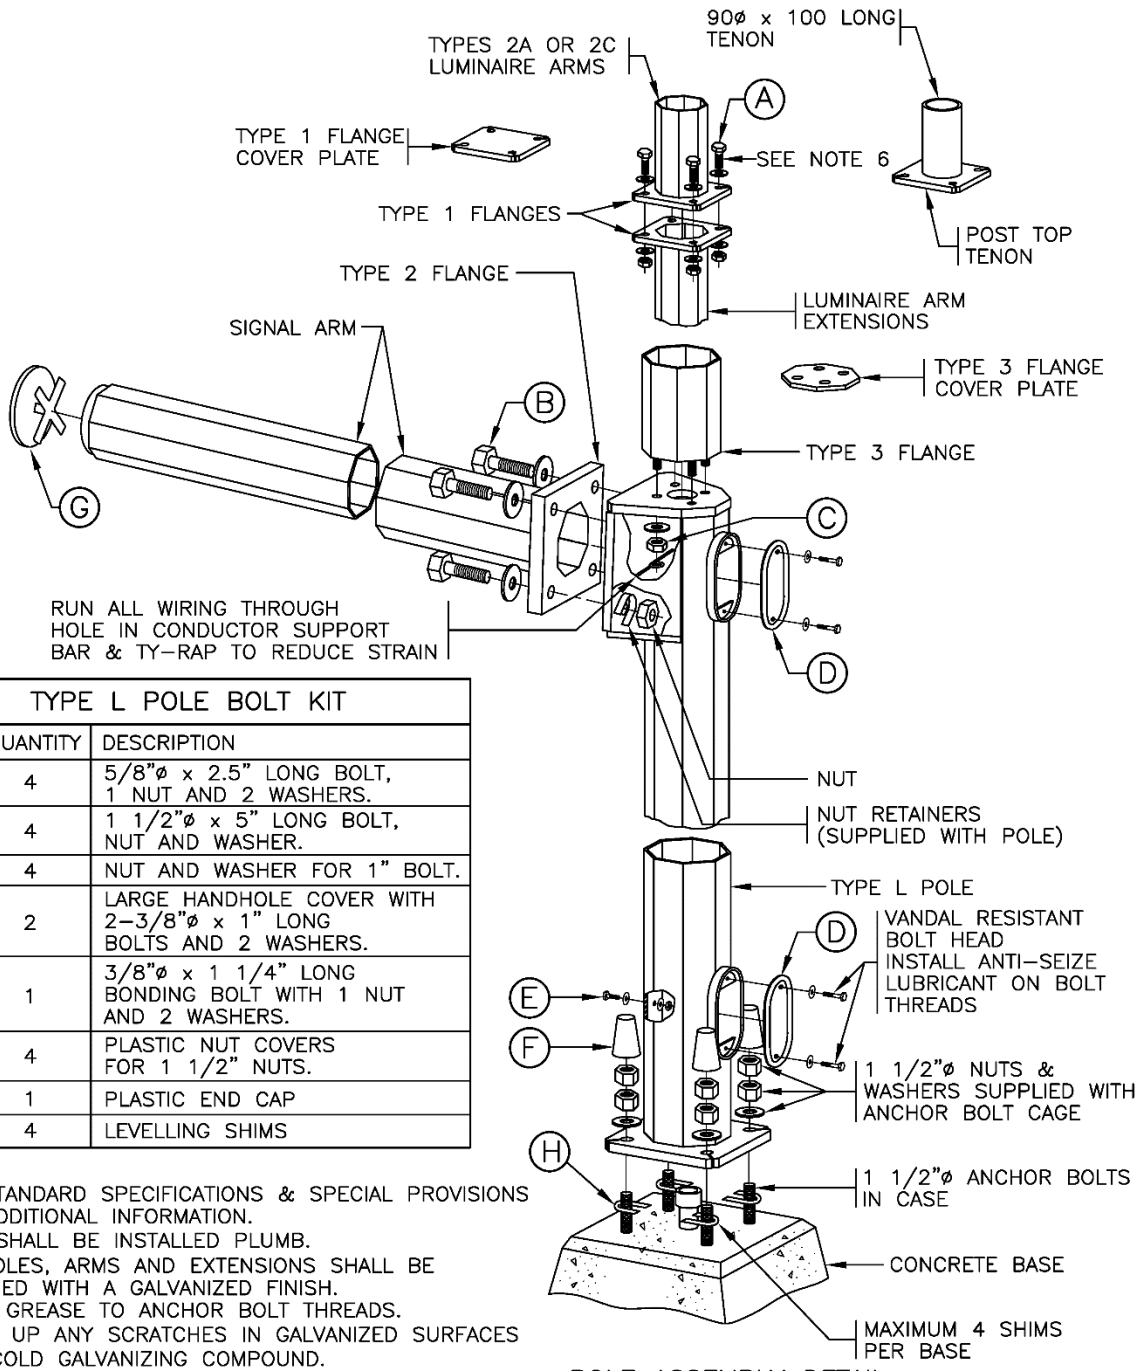

POLE ASSEMBLY DETAIL

TYPE L POLE BOLT KIT		
ITEM	QUANTITY	DESCRIPTION
A	4	5/8"ø x 2.5" LONG BOLT, 1 NUT AND 2 WASHERS.
B	4	1 1/2"ø x 5" LONG BOLT, NUT AND WASHER.
C	4	NUT AND WASHER FOR 1" BOLT.
D	2	LARGE HANDHOLE COVER WITH 2-3/8"ø x 1" LONG BOLTS AND 2 WASHERS.
E	1	3/8"ø x 1 1/4" LONG BONDING BOLT WITH 1 NUT AND 2 WASHERS.
F	4	PLASTIC NUT COVERS FOR 1 1/2" NUTS.
G	1	PLASTIC END CAP
H	4	LEVELLING SHIMS

NOTES

1. SEE STANDARD SPECIFICATIONS & SPECIAL PROVISIONS FOR ADDITIONAL INFORMATION.
2. POLE SHALL BE INSTALLED PLUMB.
3. ALL POLES, ARMS AND EXTENSIONS SHALL BE SUPPLIED WITH A GALVANIZED FINISH.
4. APPLY GREASE TO ANCHOR BOLT THREADS.
5. TOUCH UP ANY SCRATCHES IN GALVANIZED SURFACES WITH COLD GALVANIZING COMPOUND.
6. BOLT, WASHERS, AND SINGLE NUT SHALL CONFORM TO ASTM F3125 GRADE A325. GRADE SAE 5 BOLTS WITH THE FOLLOWING SPECIFICATIONS MAY BE SUBSTITUTED: 5/8" DIAMETER, 3" LENGTH, 2 WASHERS, AND 2 NUTS. CONNECTION INSTALLATION TO BE IN ACCORDANCE WITH "TURN-OF-NUT" METHOD SPECIFIED IN CSA S6.

NOT TO SCALE

BRITISH COLUMBIA | Ministry of Transportation and Infrastructure

No.	Revision	Date
G	GENERAL REVISIONS AND NEW DRAWING NUMBER	APR 20
F	GENERAL REVISIONS	APR 17
E	TYPE 1&2 FLANGE BOLTS CHANGED TO A325	DEC 10
D	ANTI-SEIZING LUBRICANT NOTED ON HANDHOLE BOLT	NOV 98
C	CONDUCTOR SUPPORT BAR ADDED	AUG 96

TYPE L SIGNAL POLE INSTALLATION DETAILS


Date Approved

30/09/93 E.L. (Signature on File)

Chief Highway Engineer

SPECIFICATION DRAWING No.

SP635-2.2.6

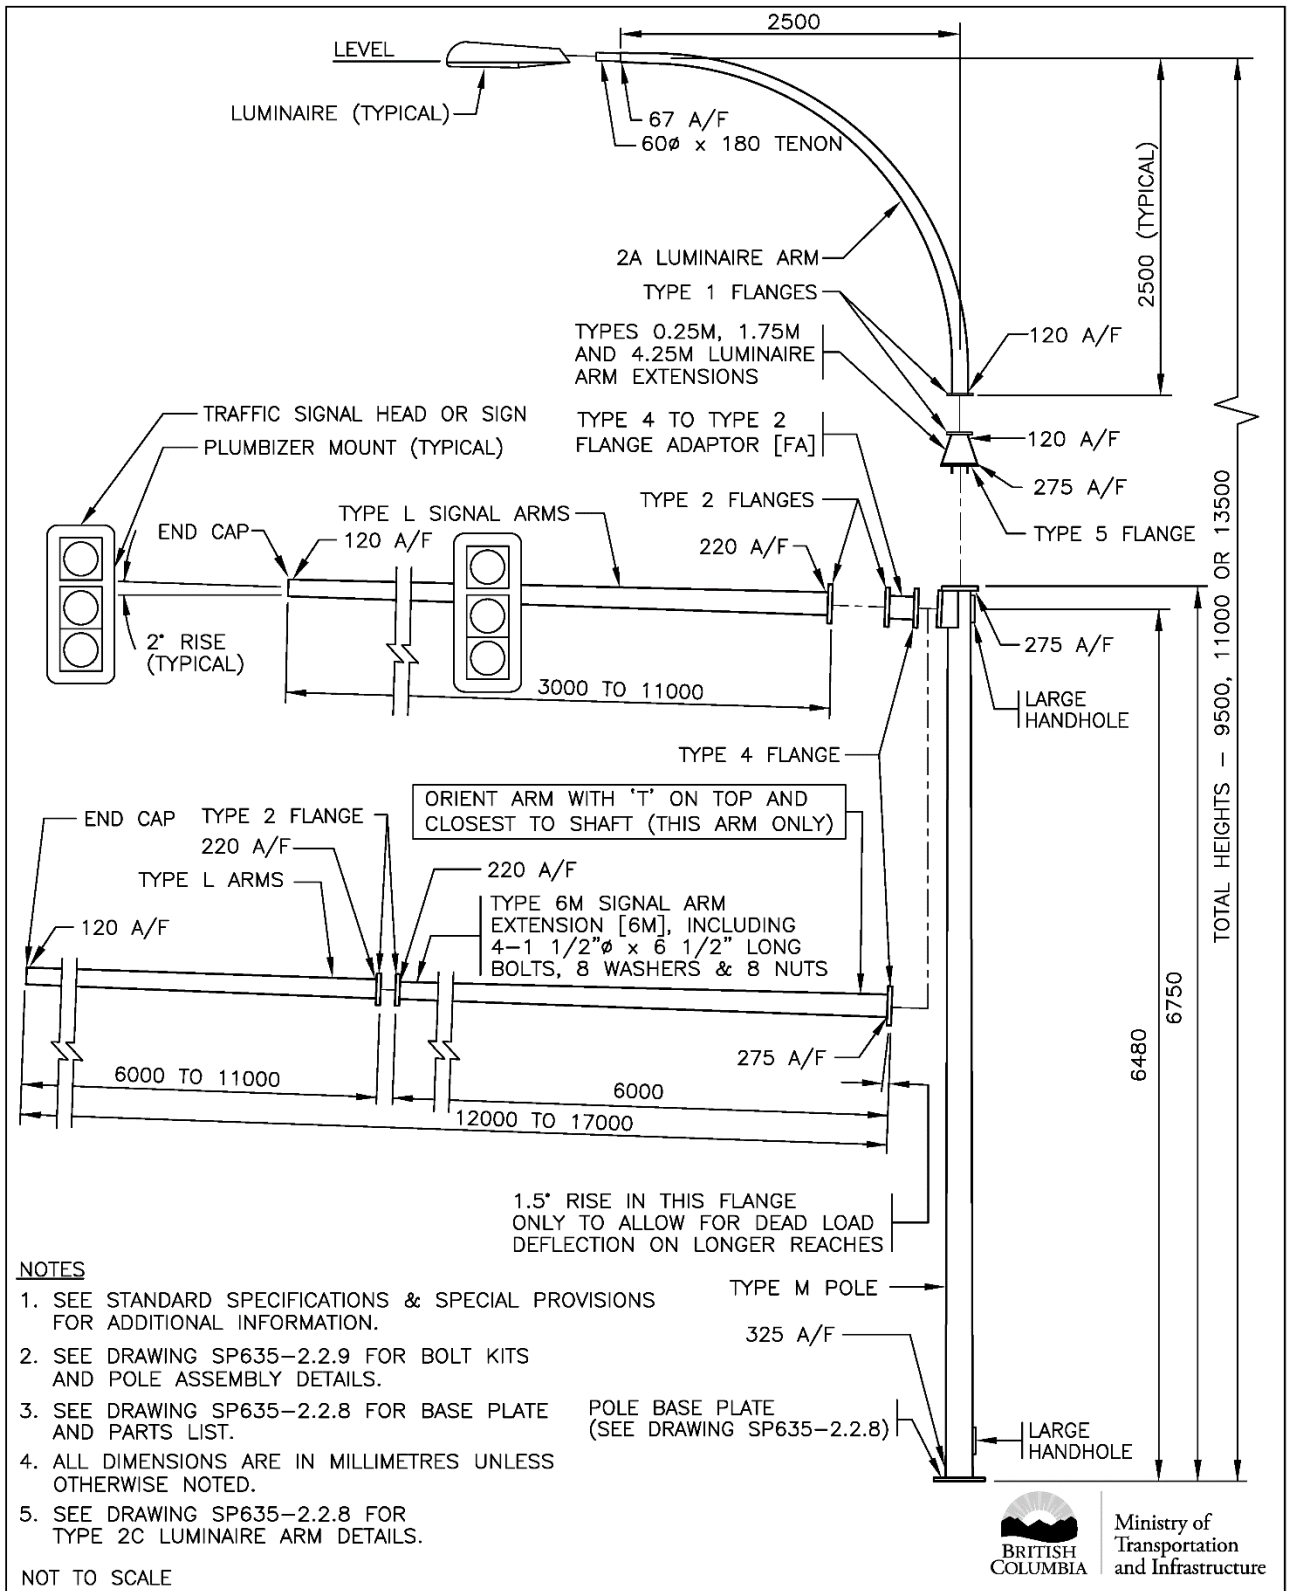

NOTES

1. SEE STANDARD SPECIFICATIONS & SPECIAL PROVISIONS FOR ADDITIONAL INFORMATION.
2. SEE DRAWING SP635–2.2.9 FOR BOLT KITS AND POLE ASSEMBLY DETAILS.
3. SEE DRAWING SP635–2.2.8 FOR BASE PLATE AND PARTS LIST.
4. ALL DIMENSIONS ARE IN MILLIMETRES UNLESS OTHERWISE NOTED.
5. SEE DRAWING SP635–2.2.8 FOR TYPE 2C LUMINAIRE ARM DETAILS.

NOT TO SCALE


BRITISH COLUMBIA | Ministry of Transportation and Infrastructure

No.	Revision	Date
F	GENERAL REVISIONS AND NEW DRAWING NUMBER	APR 20
E	GENERAL REVISIONS	APR 17
D	SIGNAL HEAD MOUNTING ADDED	OCT 03
C	TYPE 6M EXTENSION ARM NOTE REVISED	AUG 96
B	6M ARM REVISED	AUG 95
A	GENERAL REVISIONS	AUG 94


TYPE M SIGNAL POLE INSTALLATION DETAILS

Date: **30/09/93** Approved: **E.L.** **(Signature on File)**
Chief Highway Engineer

SPECIFICATION DRAWING No.
SP635–2.2.7

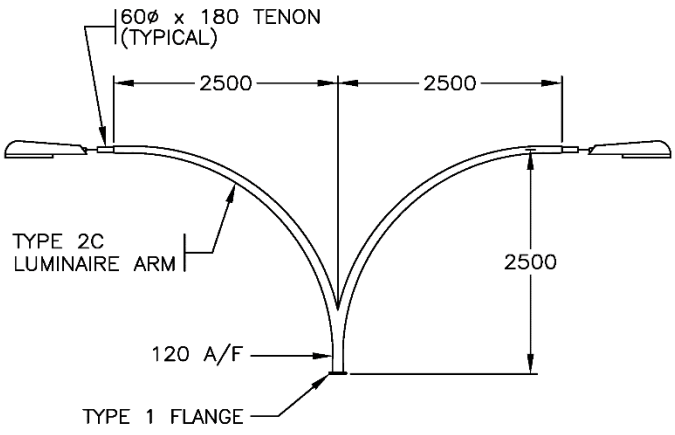

TYPE 2C LUMINAIRE ARM DETAILS

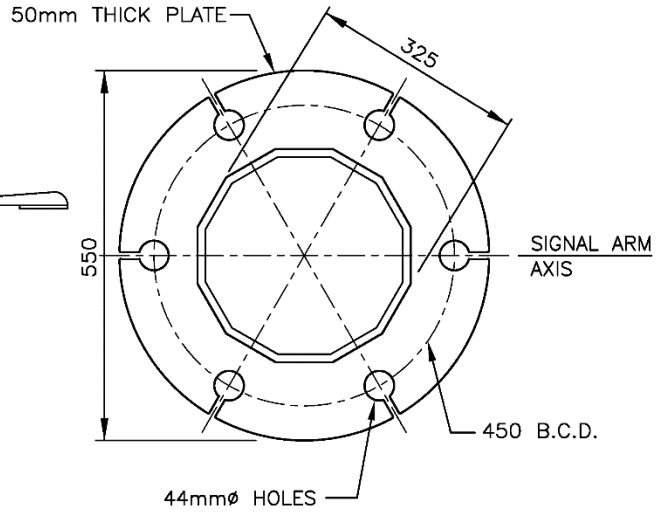

TYPE M POLE BASE PLATE

PARTS LIST FOR TYPE M SIGNAL POLE	
PART	MASS (kg)
TYPE [M] POLE	565
TYPE [6M] SIGNAL ARM EXTENSION – 6.0m	360
TYPE [3L] SIGNAL ARM – 3.0m	97
TYPE [4L] SIGNAL ARM – 4.0m	118
TYPE [5L] SIGNAL ARM – 5.0m	173
TYPE [6L] SIGNAL ARM – 6.0m	201
TYPE [7L] SIGNAL ARM – 7.0m	229
TYPE [8L] SIGNAL ARM – 8.0m	257
TYPE [9L] SIGNAL ARM – 9.0m	284
TYPE [10L] SIGNAL ARM – 10.0m	377
TYPE [11L] SIGNAL ARM – 11.0m	410
TYPE [4.25M] LUMINAIRE ARM EXTENSION – 4.25m	115
TYPE [1.75M] LUMINAIRE ARM EXTENSION – 1.75m	38
TYPE [0.25M] LUMINAIRE ARM EXTENSION – 0.25m	14
TYPE [2A] LUMINAIRE ARM	35
TYPE [2C] LUMINAIRE ARM	65
TYPE 1 FLANGE COVER PLATE [1 FCP]	1.5
TYPE 3 FLANGE COVER PLATE [3 FCP]	4
TYPE 4 FLANGE COVER PLATE [4 FCP]	8
TYPE 5 FLANGE COVER PLATE [5 FCP]	4
TYPE 4 TO 2 FLANGE ADAPTOR [FA]	75
POST TOP TENON [PTT]	5

* [ ] I.D. LABEL ON POLE

BRITISH COLUMBIA | Ministry of Transportation and Infrastructure

NOT TO SCALE

No.	Revision	Date
F		
E		
D	NEW DRAWING NUMBER	APR 20
C	GENERAL REVISIONS	APR 17
B	HOLE SIZE REVISED & 2C ARM ADDED	AUG 95
A	GENERAL REVISIONS	AUG 94

TYPE M SIGNAL POLE INSTALLATION DETAILS


Date Approved

30/09/93 E.L. (Signature on File)

Chief Highway Engineer

SPECIFICATION DRAWING No.

SP635–2.2.8

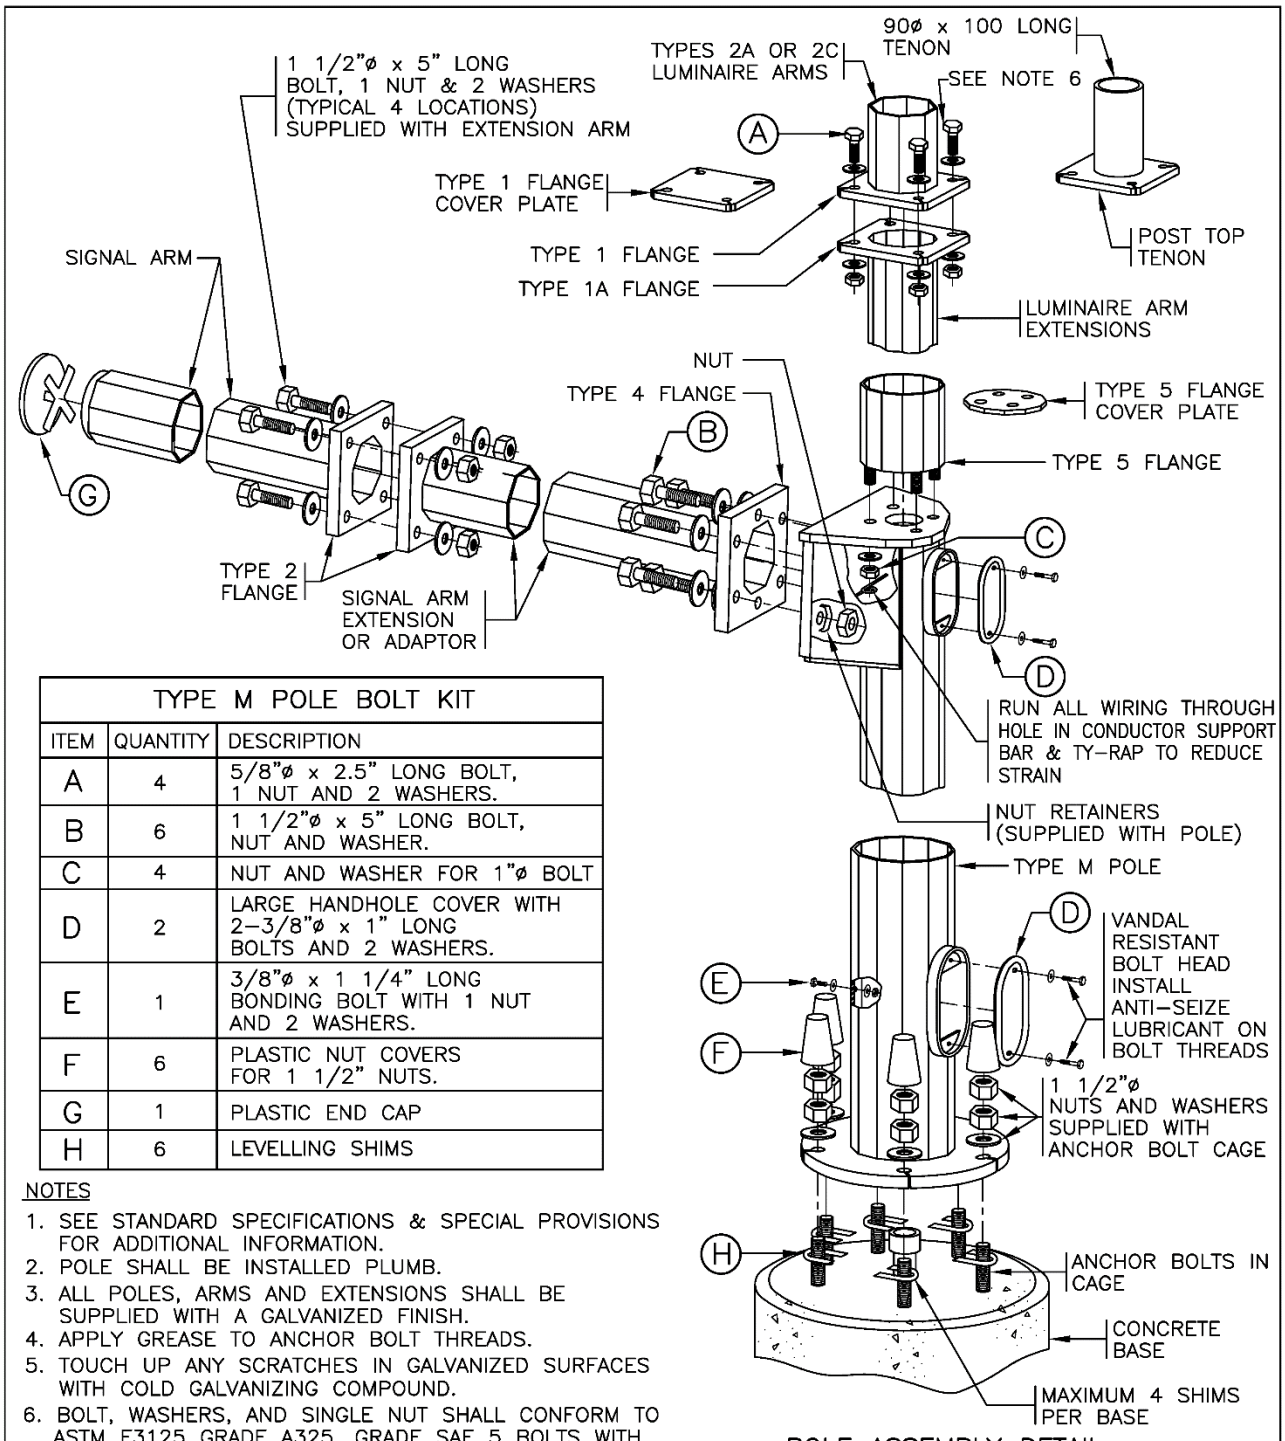

POLE ASSEMBLY DETAIL

TYPE M POLE BOLT KIT		
ITEM	QUANTITY	DESCRIPTION
A	4	5/8"ø x 2.5" LONG BOLT, 1 NUT AND 2 WASHERS.
B	6	1 1/2"ø x 5" LONG BOLT, NUT AND WASHER.
C	4	NUT AND WASHER FOR 1"ø BOLT
D	2	LARGE HANDHOLE COVER WITH 2-3/8"ø x 1" LONG BOLTS AND 2 WASHERS.
E	1	3/8"ø x 1 1/4" LONG BONDING BOLT WITH 1 NUT AND 2 WASHERS.
F	6	PLASTIC NUT COVERS FOR 1 1/2" NUTS.
G	1	PLASTIC END CAP
H	6	LEVELLING SHIMS

NOTES

1. SEE STANDARD SPECIFICATIONS & SPECIAL PROVISIONS FOR ADDITIONAL INFORMATION.
2. POLE SHALL BE INSTALLED PLUMB.
3. ALL POLES, ARMS AND EXTENSIONS SHALL BE SUPPLIED WITH A GALVANIZED FINISH.
4. APPLY GREASE TO ANCHOR BOLT THREADS.
5. TOUCH UP ANY SCRATCHES IN GALVANIZED SURFACES WITH COLD GALVANIZING COMPOUND.
6. BOLT, WASHERS, AND SINGLE NUT SHALL CONFORM TO ASTM F3125 GRADE A325. GRADE SAE 5 BOLTS WITH THE FOLLOWING SPECIFICATIONS MAY BE SUBSTITUTED: 5/8" DIAMETER, 3" LENGTH, 2 WASHERS, AND 2 NUTS. CONNECTION INSTALLATION TO BE IN ACCORDANCE WITH "TURN-OF-NUT" METHOD SPECIFIED IN CSA S6.

NOT TO SCALE

BRITISH COLUMBIA | Ministry of Transportation and Infrastructure

No.	Revision	Date
G	GENERAL REVISIONS AND NEW DRAWING NUMBER	APR 20
F	GENERAL REVISIONS	APR 17
E	TYPE 1&2 FLANGED BOLTS CHANGED TO A325	DEC 10
D	ANTI-SEIZING LUBRICANT NOTED ON HANDHOLE BOLT	NOV 98
C	BOLT KIT LIST REVISED & CONDUCTOR SUPPORT ADDED	AUG 96

TYPE M SIGNAL POLE INSTALLATION DETAILS


Date Approved

30/09/93 E.L. (Signature on File)


Chief Highway Engineer

SPECIFICATION DRAWING No.


SP635-2.2.9

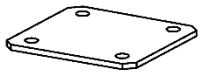


TYPE 1 FLANGE COVER PLATE

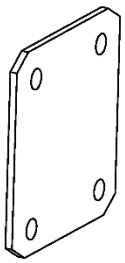


TYPE 2 FLANGE COVER PLATE

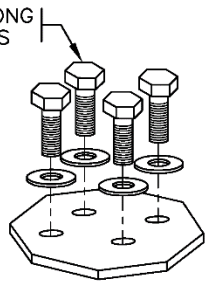


TYPE 3 FLANGE COVER PLATE

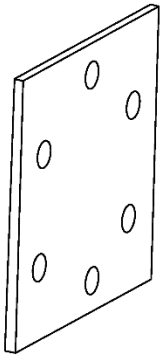


TYPE 4 FLANGE COVER PLATE

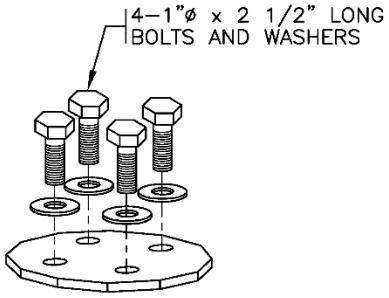


TYPE 5 FLANGE COVER PLATE

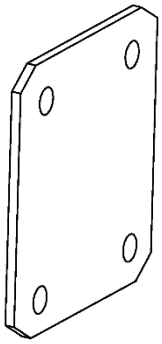


TYPE 8 FLANGE COVER PLATE

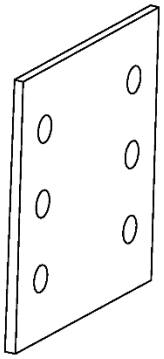

TYPE S FLANGE COVER PLATE

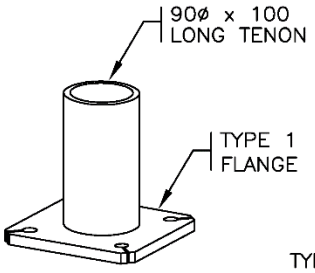

POST TOP TENON

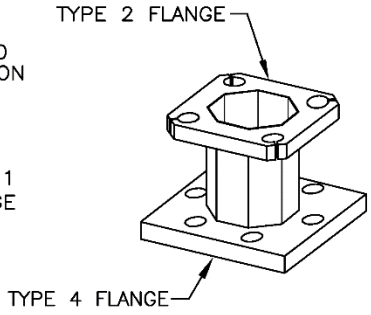

TYPE 4 TO TYPE 2 FLANGE ADAPTOR

NOTES

1. SEE STANDARD SPECIFICATIONS & SPECIAL PROVISIONS FOR ADDITIONAL INFORMATION.

NOT TO SCALE


BRITISH COLUMBIA | Ministry of Transportation and Infrastructure

No.	Revision	Date
F		
E		
D		
C		
B	GENERAL REVISIONS	APR 17
A	TYPE S FLANGE COVER PLATE ADDED	OCT 03

SIGNAL POLE ACCESSORIES

Date: **14/11/03** Approved: **D.N. (Signature on File)** Chief Engineer

SPECIFICATION DRAWING No. SP635–2.2.10

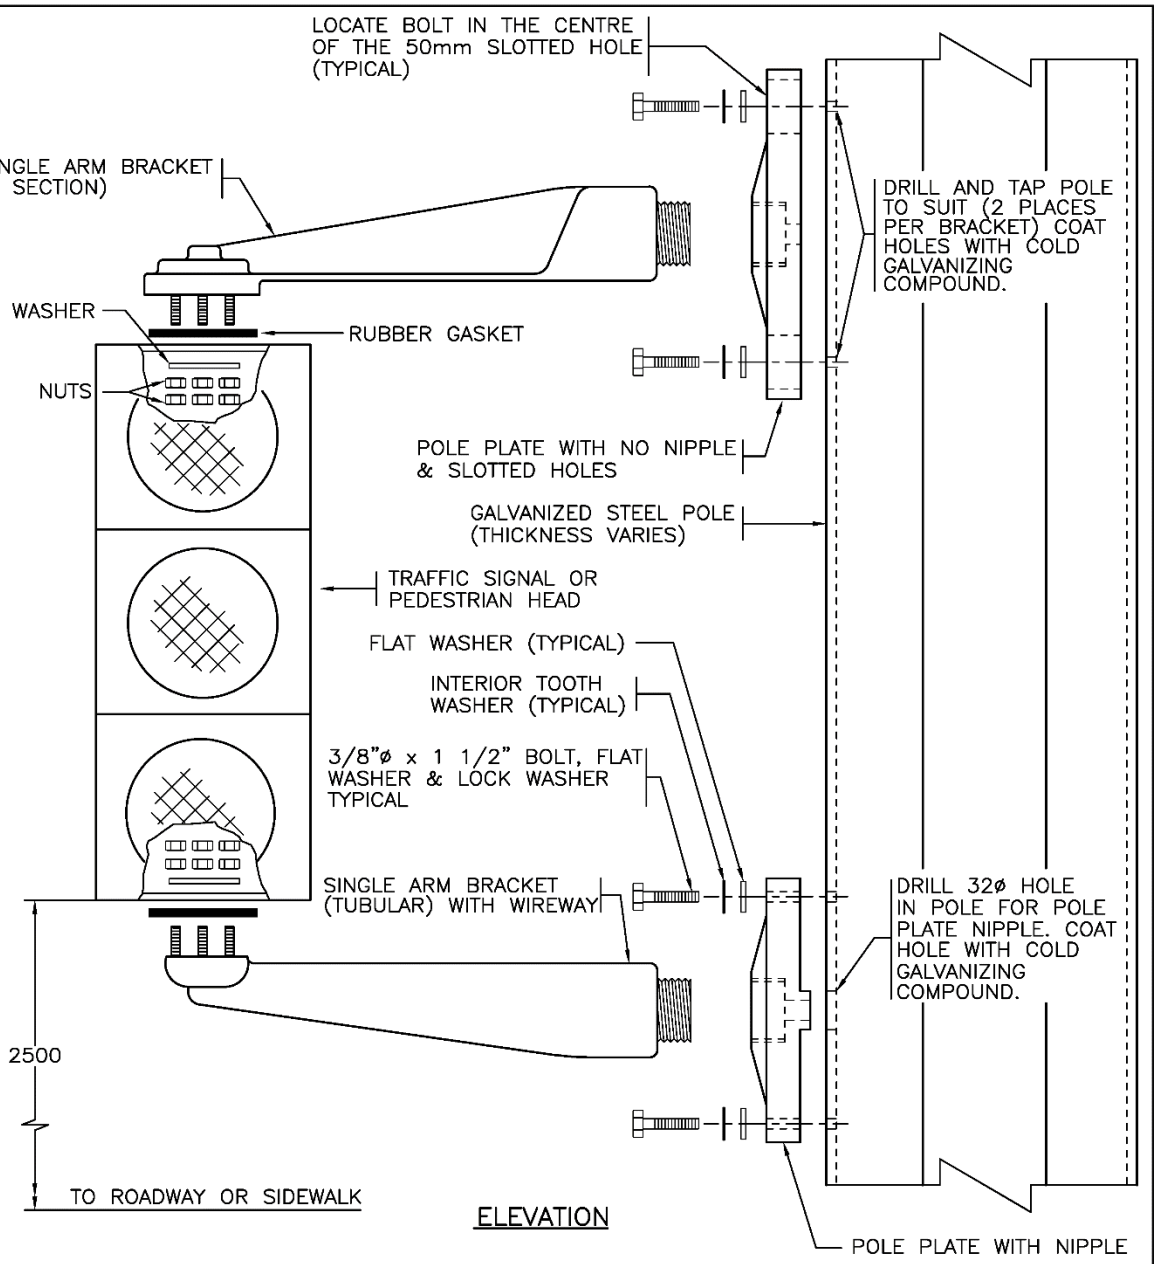

ELEVATION

NOTES:

1. SEE STANDARD SPECIFICATIONS & SPECIAL PROVISIONS FOR ADDITIONAL INFORMATION
2. AIM SIGNAL HEADS IN ACCORDANCE WITH DRAWING SP635–2.3.11
3. WHERE 3 OR MORE SIDE MOUNT SIGNAL HEADS ARE REQUIRED ON A POLE LOCATE THE 3rd AND 4th PEDESTRIAN HEAD ARM BRACKETS WITH WIREWAY AND POLE PLATE WITH THE NIPPLE TO THE TOP OF THE HEAD TO AVOID EXCESSIVE DRILLING OF THE POLE IN ONE AREA.

NOT TO SCALE

BRITISH COLUMBIA Ministry of Transportation and Infrastructure

No.	Revision	Date
F	GENERAL REVISIONS	APR 20
E	GENERAL REVISIONS	APR 17
D	NOTE 2 REVISED	OCT 03
C	NYLOCK NUTS REMOVED. DOUBLE NUTS ADDED	AUG 99
B	SIGN MOUNTING HEIGHT ADDED	AUG 95
A	GENERAL REVISIONS	AUG 94

SIGNAL AND PEDESTRIAN HEAD SIDE MOUNT INSTALLATION DETAILS


Date Approved

30/09/93 E.L. **(Signature on File)**

Chief Highway Engineer

SPECIFICATION DRAWING No.

SP635–2.3.1

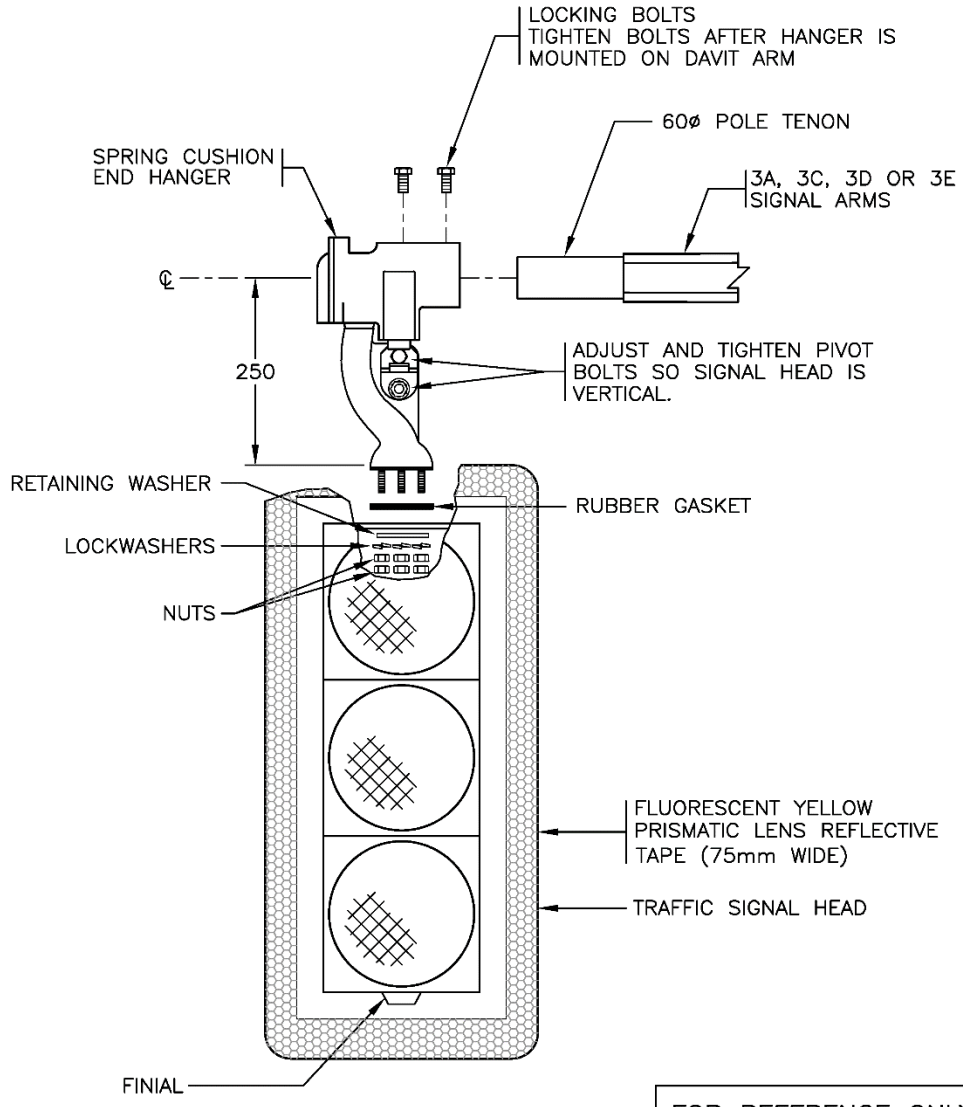

ELEVATION

FOR REFERENCE ONLY

USE END PLUMBIZER FOR INSTALLATIONS UNLESS OTHERWISE NOTED (SEE SP635–2.3.4 AND SP635–2.3.5)

NOTES

1. SEE STANDARD SPECIFICATIONS & SPECIAL PROVISIONS FOR ADDITIONAL INFORMATION.
2. AIM SIGNAL HEADS IN ACCORDANCE WITH DRAWING SP635–2.3.11

NOT TO SCALE

BRITISH COLUMBIA | Ministry of Transportation and Infrastructure

No.	Revision	Date
H	REFERENCE NOTE UPDATED	APR 20
G	GENERAL REVISIONS	APR 17
F	NOTE 2 REVISED	OCT 03
E	REFLECTIVE TAPE ADDED	NOV 01
D	NYLOCK NUTS REMOVED. DOUBLE NUTS ADDED	AUG 99
C	NEW DRAWING	OCT 97

OVERHEAD SPRING CUSHION END SIGNAL HEAD HANGER INSTALLATION DETAILS


Date Approved

30/09/93 E.L. (Signature on File)

Chief Highway Engineer

SPECIFICATION DRAWING No.

SP635–2.3.2

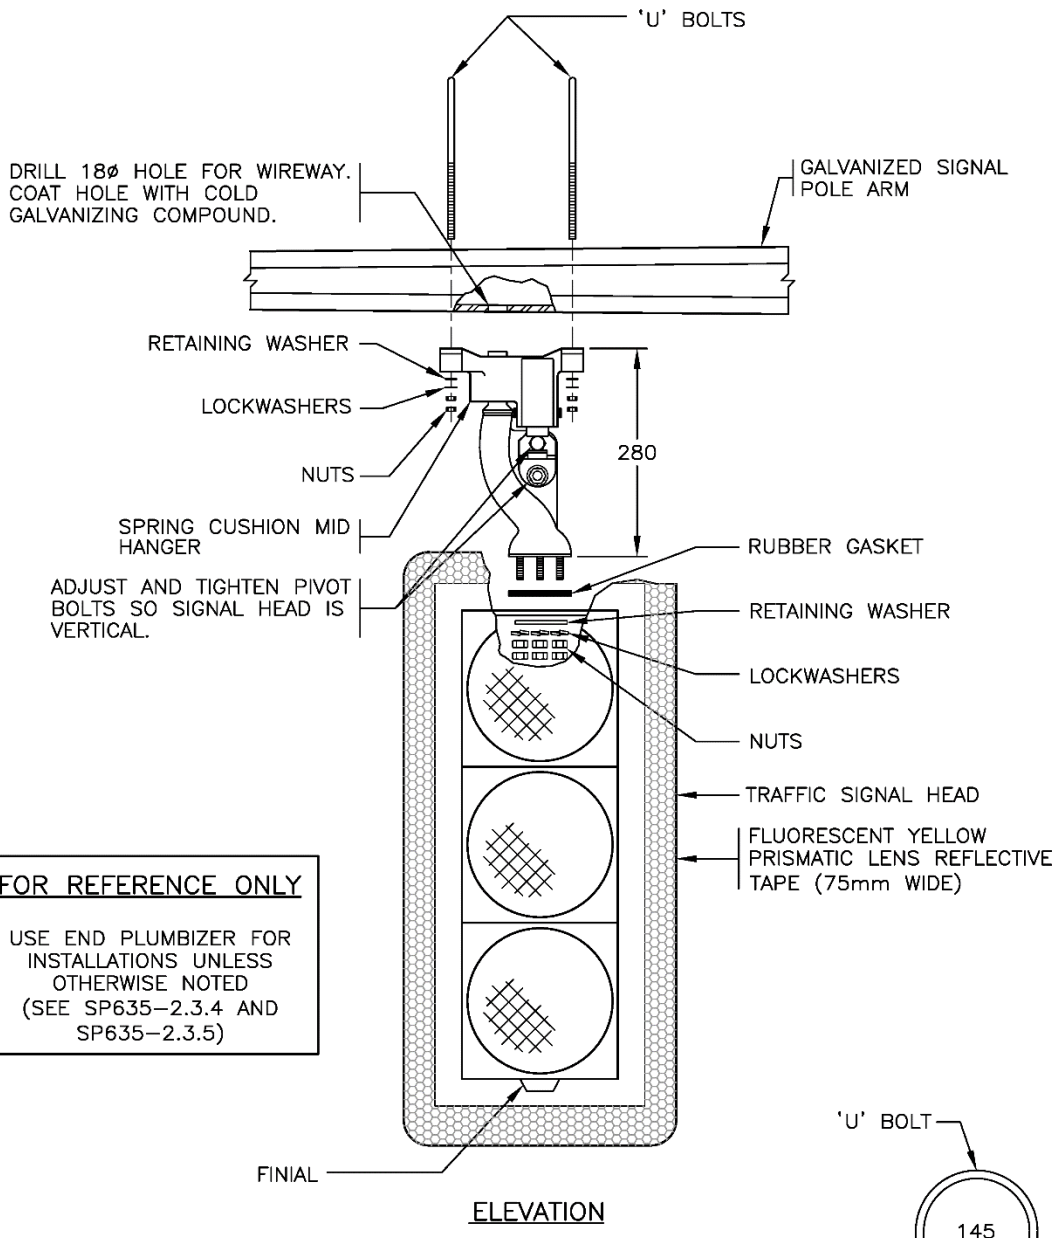

FOR REFERENCE ONLY

USE END PLUMBIZER FOR INSTALLATIONS UNLESS OTHERWISE NOTED (SEE SP635–2.3.4 AND SP635–2.3.5)

NOTES

1. SEE STANDARD SPECIFICATIONS & SPECIAL PROVISIONS FOR ADDITIONAL INFORMATION.
2. AIM SIGNAL HEADS IN ACCORDANCE WITH DRAWING SP635–2.3.11

NOT TO SCALE

BRITISH COLUMBIA Ministry of Transportation and Infrastructure

No.	Revision	Date
I	REFERENCE NOTE UPDATED	APR 20
H	GENERAL REVISIONS	APR 17
G	GENERAL REVISIONS	APR 17
F	NOTE 2 REVISED	OCT 03
E	REFLECTIVE TAPE ADDED	NOV 01
D	NYLOCK NUTS REMOVED. DOUBLE NUTS ADDED	AUG 99

OVERHEAD SPRING CUSHION MID HANGER SIGNAL HEAD INSTALLATION DETAILS


Date Approved

30/09/93 E.L. (Signature on File)


Chief Highway Engineer

SPECIFICATION DRAWING No.

SP635–2.3.3

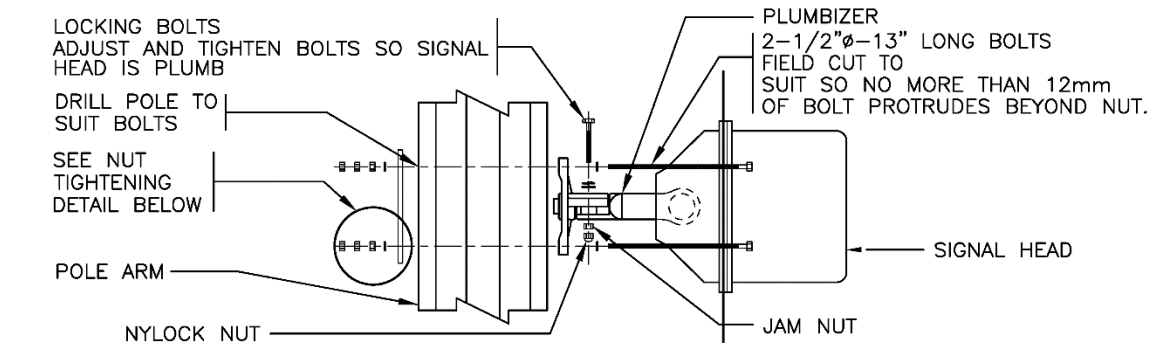


TOP VIEW

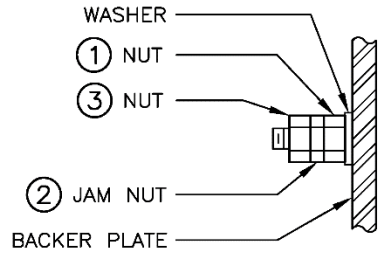


- TIGHTEN NUT (1) AGAINST WASHER,
- TIGHTEN JAM NUT (2) AGAINST NUT (1),
- SNUG NUT (3) AGAINST JAM NUT (2) AND THEN TIGHTEN NUT (3) AND JAM NUT (2) INTO EACH OTHER.

NUT TIGHTENING DETAIL

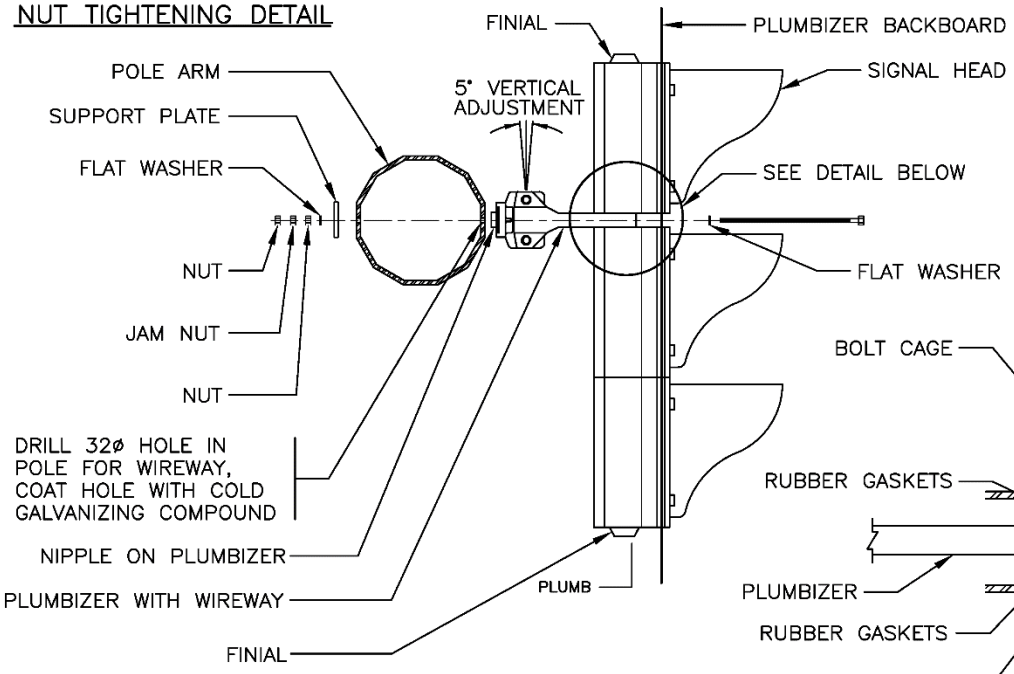

ELEVATION

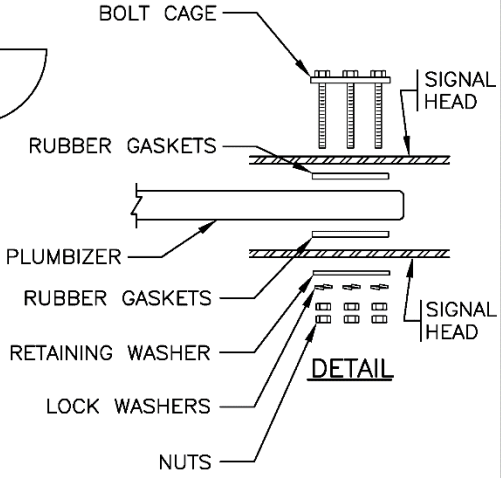

DETAIL

NOTES

1. SEE STANDARD SPECIFICATIONS & SPECIAL PROVISIONS FOR ADDITIONAL INFORMATION.
2. AIM SIGNAL HEADS IN ACCORDANCE WITH DRAWING SP635-2.3.11

NOT TO SCALE

BRITISH COLUMBIA | Ministry of Transportation and Infrastructure

No.	Revision	Date
G	GENERAL REVISIONS	APR 17
F	NOTE 2 REVISED	OCT 03
E	DETAILS FROM SP635-2.3.5 ADDED	NOV 01
D	NYLOCK NUTS REMOVED, DOUBLE NUTS ADDED	AUG 99
C	NEW DRAWING NUMBER	OCT 97
B	CONNECTION BOLTS REVISED	AUG 95

SIGNAL HEAD PLUMBIZER INSTALLATION DETAILS


Date Approved

30/09/93 E.L. **(Signature on File)**


Chief Highway Engineer

SPECIFICATION DRAWING No.

SP635-2.3.4

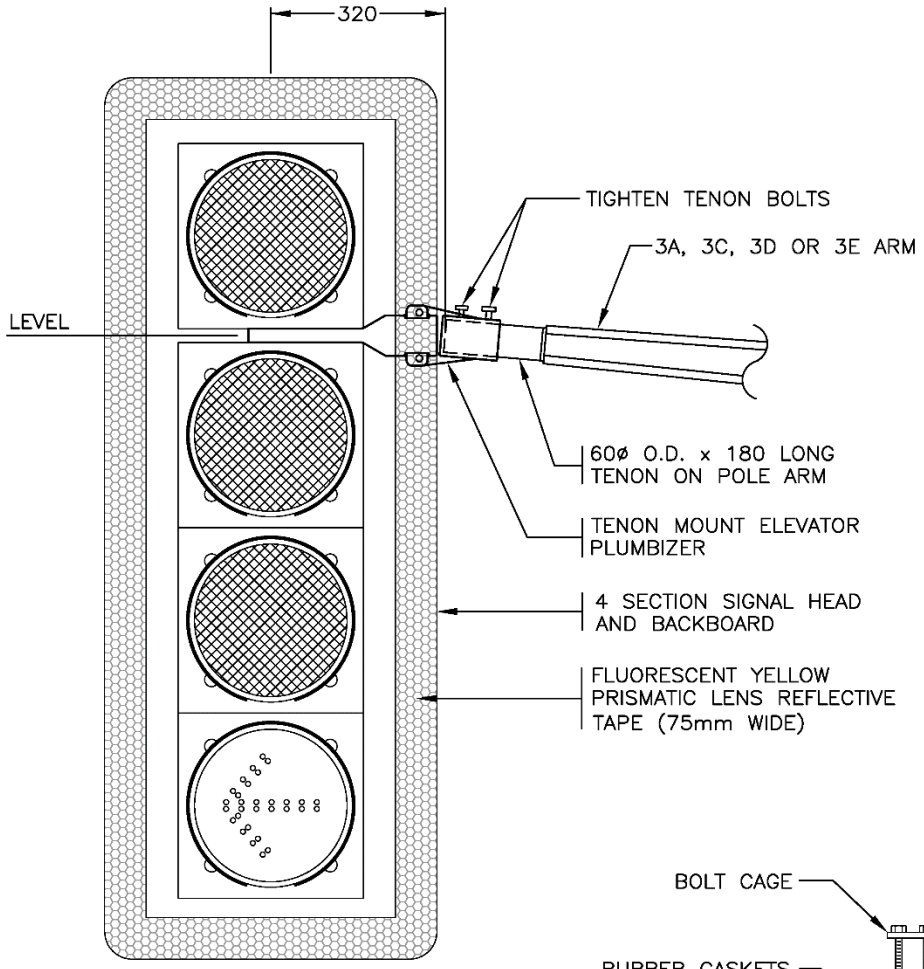

ELEVATION

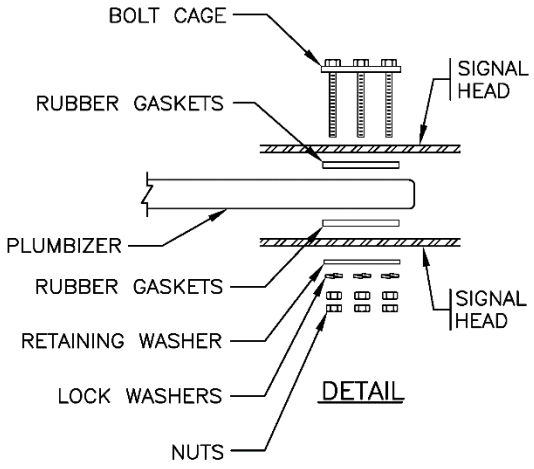

DETAIL

NOTES

1. SEE STANDARD SPECIFICATIONS & SPECIAL PROVISIONS FOR ADDITIONAL INFORMATION.
2. AIM SIGNAL HEADS IN ACCORDANCE WITH DRAWING SP635–2.3.11.

NOT TO SCALE


BRITISH COLUMBIA | Ministry of Transportation and Infrastructure

No.	Revision	Date
F		
E		
D		
C		
B		
A	GENERAL REVISIONS	APR 17

SIGNAL HEAD PLUMBIZER
INSTALLATION DETAILS (FOR TYPE 3 SIGNAL ARMS)

Date 14/11/03 Approved D.N. (Signature on File) Chief Engineer

SPECIFICATION DRAWING No. SP635–2.3.5

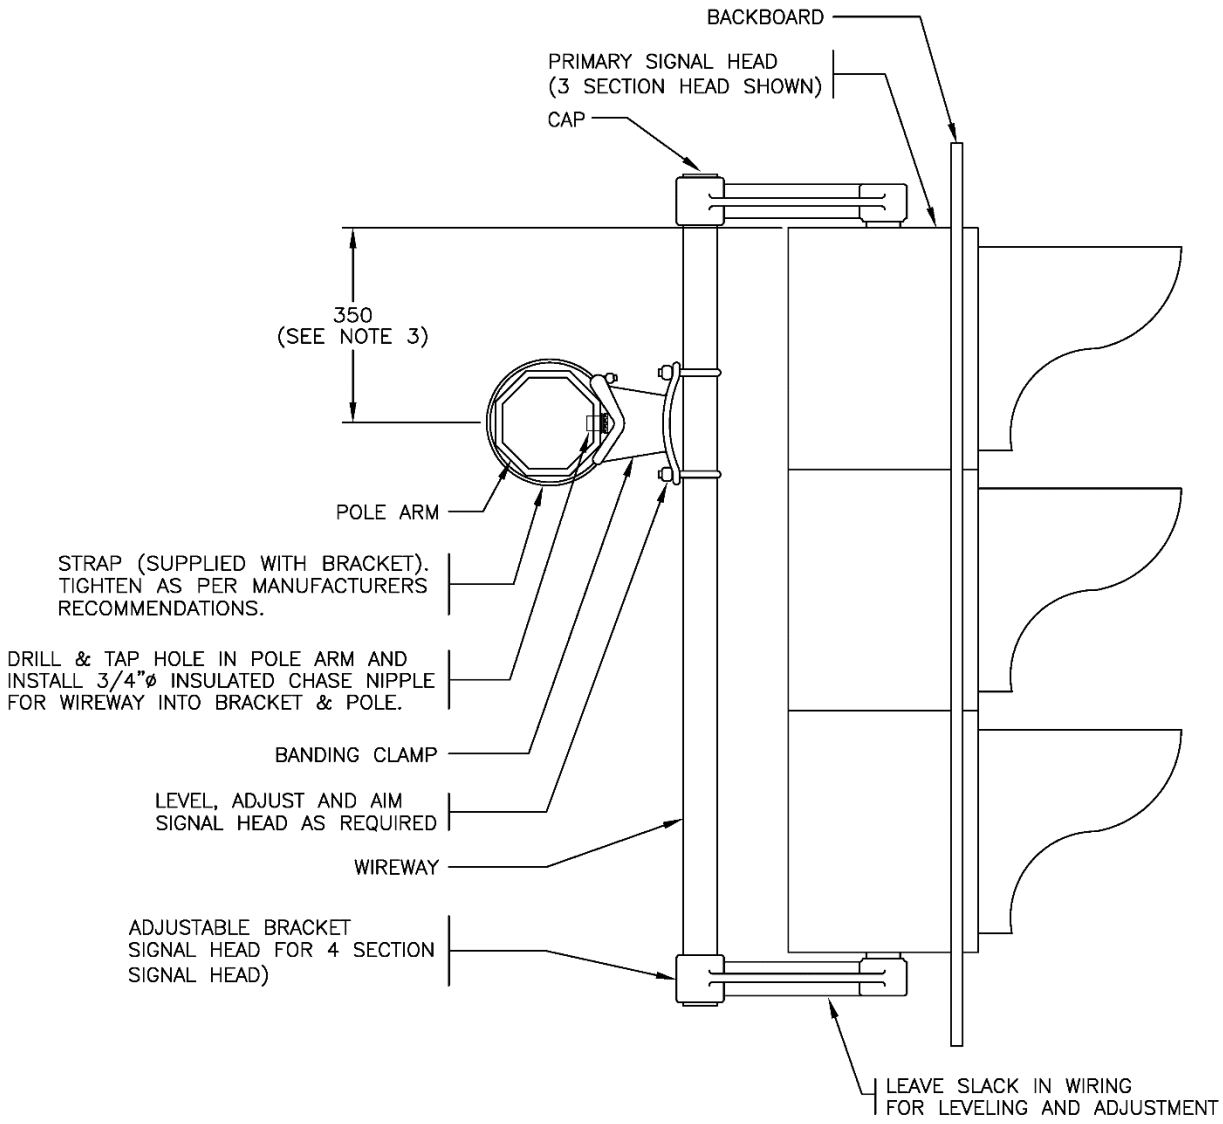

NOTES

1. SEE STANDARD SPECIFICATIONS & SPECIAL PROVISIONS FOR ADDITIONAL INFORMATION.
2. AIM SIGNAL HEADS IN ACCORDANCE WITH DRAWING SP635–2.3.11
3. ADJUST SIGNAL HEAD MOUNTING HEIGHT AS DIRECTED TO AVOID CONFLICTS.

NOT TO SCALE

BRITISH COLUMBIA | Ministry of Transportation and Infrastructure

No.	Revision	Date
F		
E		
D		
C		
B	GENERAL REVISIONS	APR 17
A	NOTE 2 REVISED	OCT 03

SIGNAL HEAD ADJUSTABLE BRACKET DETAILS


Date Approved

2001/12/13 D.N. (Signature on File)

Chief Highway Engineer

SPECIFICATION DRAWING No.

SP635–2.3.6

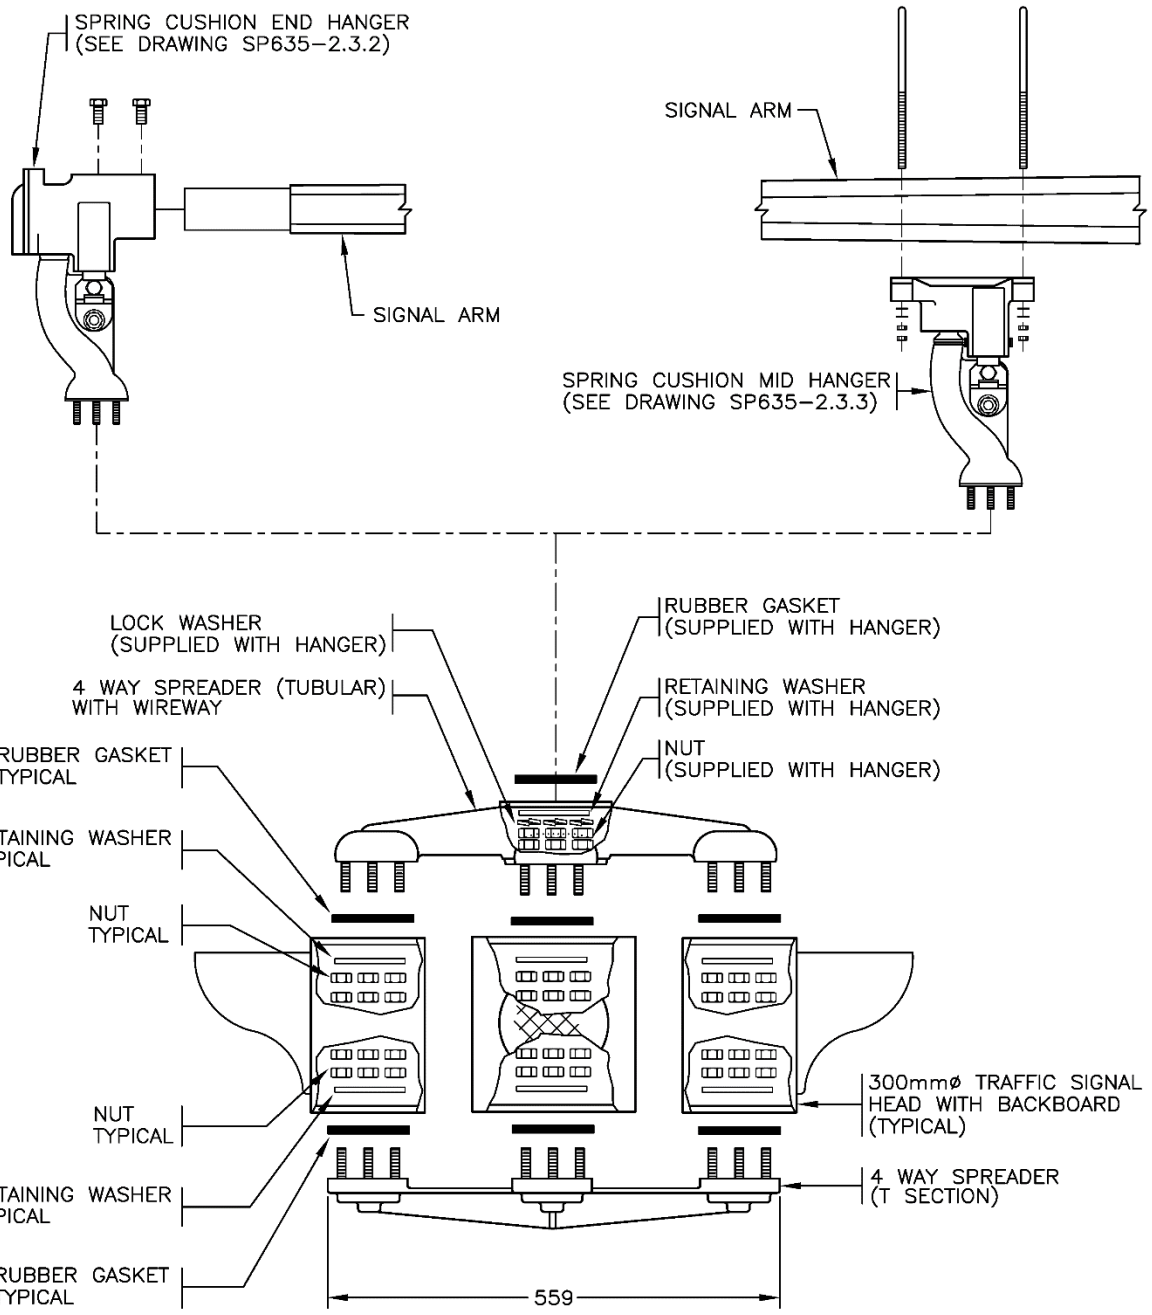

NOTES

1. SEE STANDARD SPECIFICATIONS & SPECIAL PROVISIONS FOR ADDITIONAL INFORMATION.
2. AIM SIGNAL HEADS IN ACCORDANCE WITH DRAWING SP635-2.3.11

MOUNTING FOR 2, 3 AND 4 WAY SPREADERS IDENTICAL

NOT TO SCALE

Ministry of Transportation and Infrastructure

No.	Revision	Date
H	GENERAL REVISIONS	APR 20
G	GENERAL REVISIONS	APR 17
F	NOTE 2 REVISED	OCT 03
E	NYLOCK NUTS REMOVED. DOUBLE NUTS ADDED	AUG 99
D	NEW DRAWING NUMBER	OCT 97
C	STOCK NUMBERS REVISED	AUG 96

FOUR-WAY OVERHEAD FLASHING SIGNAL HEAD INSTALLATION DETAILS


Date Approved

30/09/93 E.L. (Signature on File)


Chief Highway Engineer

SPECIFICATION DRAWING No.

SP635-2.3.7

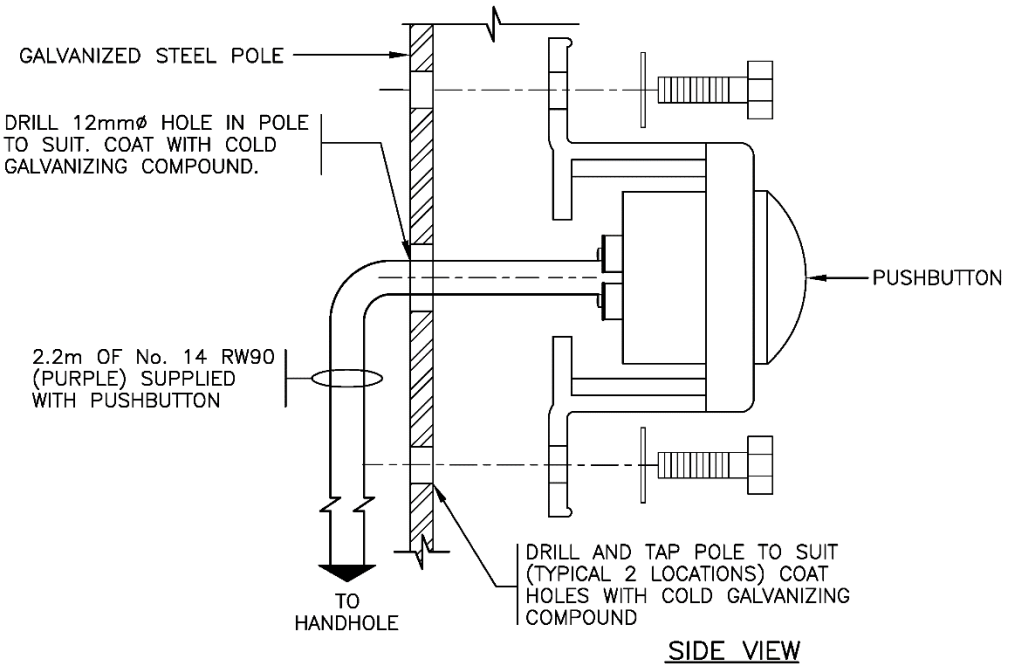

SIDE VIEW

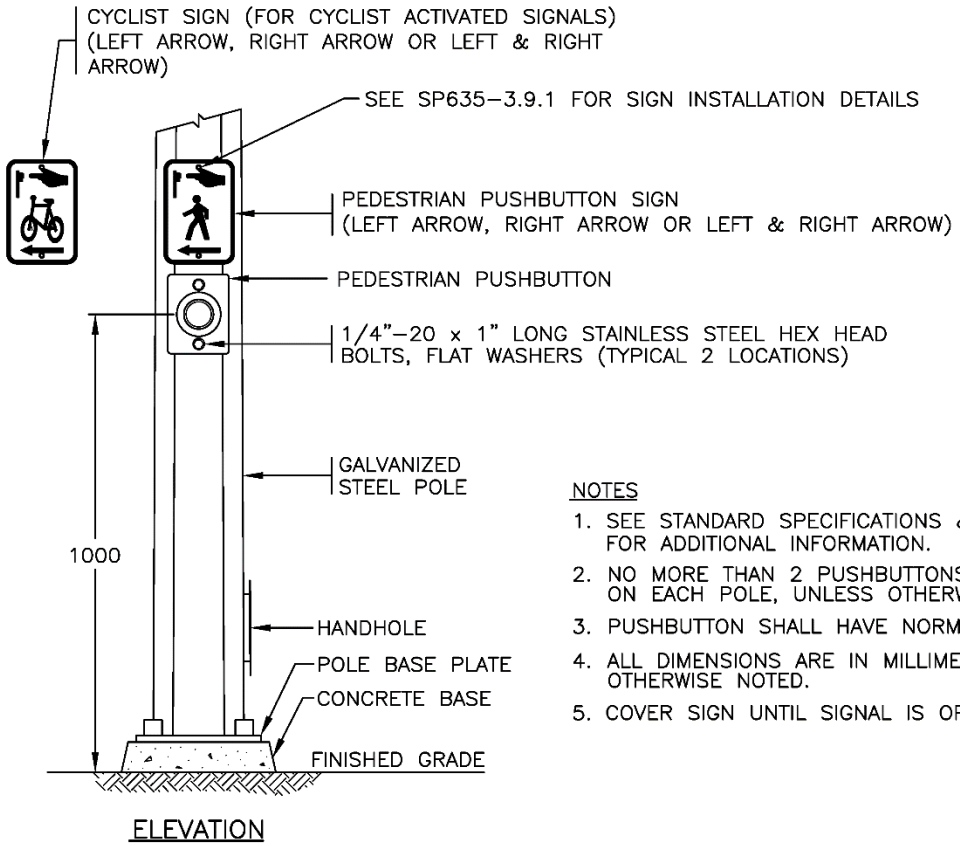

ELEVATION

NOTES

1. SEE STANDARD SPECIFICATIONS & SPECIAL PROVISIONS FOR ADDITIONAL INFORMATION.
2. NO MORE THAN 2 PUSHBUTTONS SHALL BE INSTALLED ON EACH POLE, UNLESS OTHERWISE NOTED.
3. PUSHBUTTON SHALL HAVE NORMALLY OPEN CONTACTS.
4. ALL DIMENSIONS ARE IN MILLIMETRES UNLESS OTHERWISE NOTED.
5. COVER SIGN UNTIL SIGNAL IS OPERATIONAL.

BRITISH COLUMBIA | Ministry of Transportation and Infrastructure

NOT TO SCALE

No.	Revision	Date
F	PUSHBUTTON & SIGN UPDATED	APR 20
E	GENERAL REVISIONS	APR 17
D	NEW PUSHBUTTON & SIGN	OCT 03
C	NEW DRAWING NUMBER	OCT 97
B	BOLTS AND DWG. No. REVISED	AUG 95
A	GENERAL REVISIONS	AUG 94

PEDESTRIAN PUSHBUTTON WITH INTEGRAL SIGN INSTALLATION DETAILS


Date Approved

30/09/93 E.L. (Signature on File)

Chief Highway Engineer

SPECIFICATION DRAWING No.

SP635-2.3.8

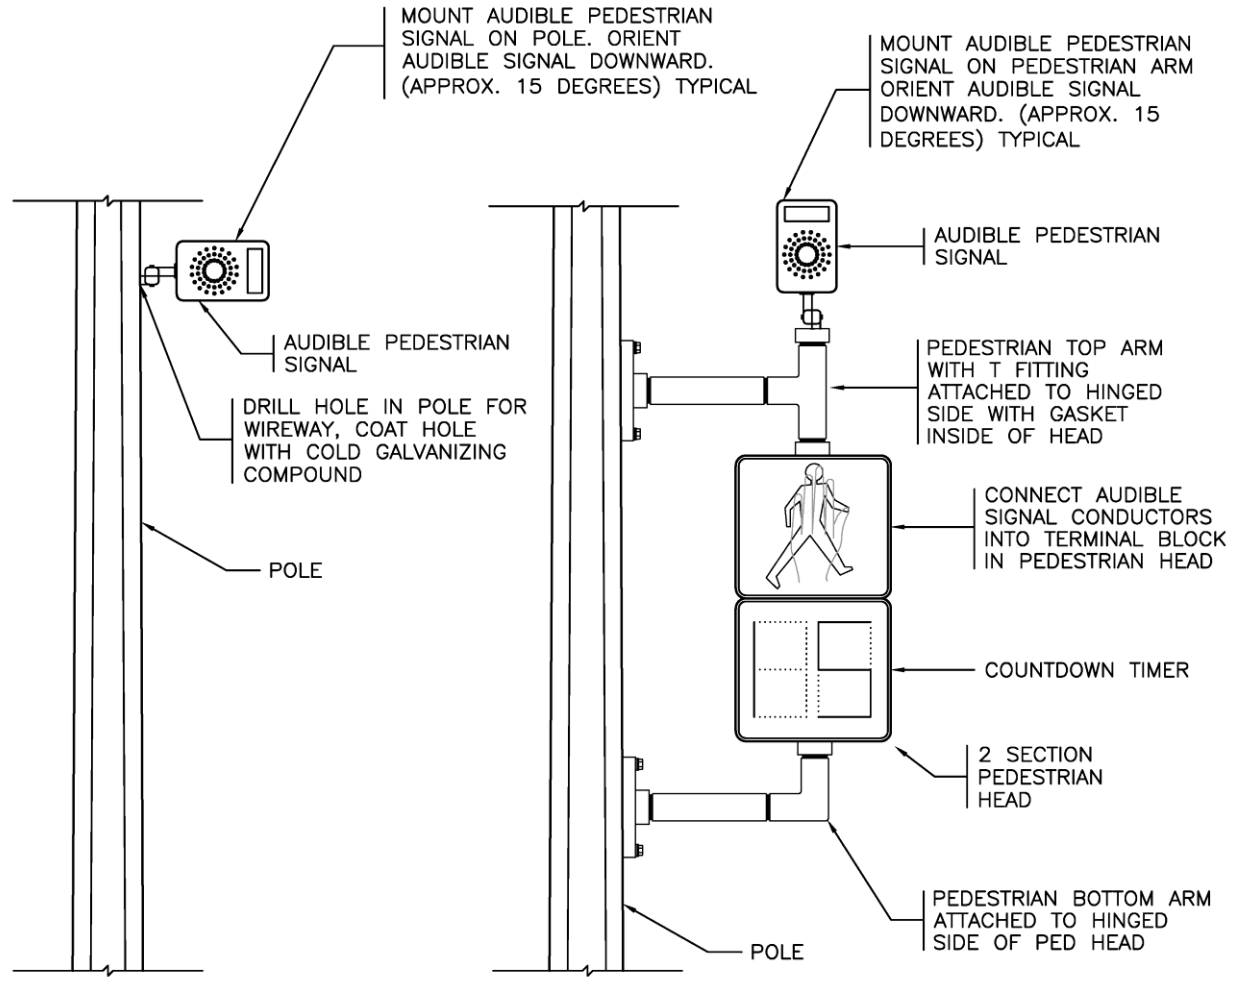

ELEVATIONS

NOTES

1. SEE STANDARD SPECIFICATIONS & SPECIAL PROVISIONS FOR ADDITIONAL INFORMATION.
2. AIM, ADJUST AND CONNECT AUDIBLE SIGNAL AS PER MANUFACTURERS INSTRUCTIONS TO THE SATISFACTION OF THE MINISTRY REPRESENTATIVE.

BRITISH COLUMBIA | Ministry of Transportation and Infrastructure


NOT TO SCALE

No.	Revision	Date
G	POLE AND T FITTING DETAILS	FEB 23
F	GENERAL REVISIONS	APR 17
E	GENERAL REVISIONS	OCT 03
D	ALTERNATE SINGLE SECTION LED PED. HEAD ADDED	NOV 01
C	NOTE 3 REVISED	NOV 98
B	NEW DRAWING NUMBER	OCT 97


AUDIBLE SIGNAL INSTALLATION DETAILS

Date: **21/11/94** Approved: **E.L.** **(Signature on File)** Chief Highway Engineer

SPECIFICATION DRAWING No. SP635–2.3.9

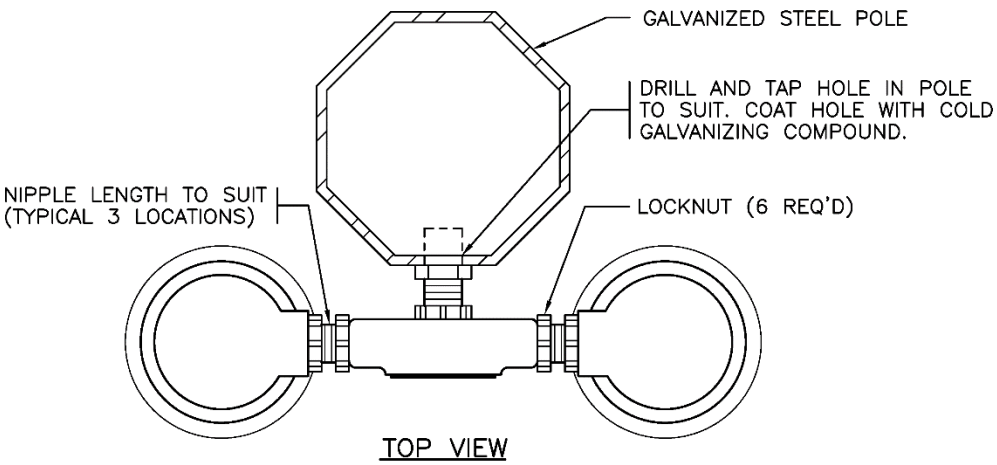

TOP VIEW

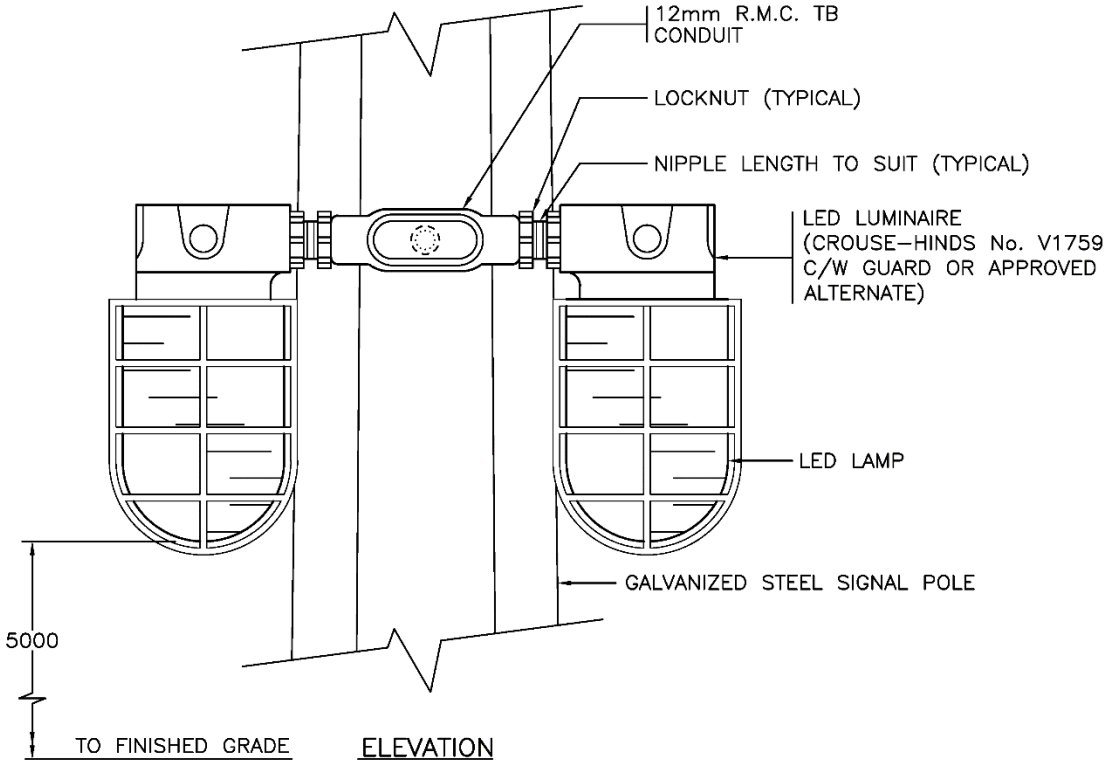

ELEVATION

NOTES

1. SEE STANDARD SPECIFICATIONS & SPECIAL PROVISIONS FOR ADDITIONAL INFORMATION.
2. ALL NUTS, WASHERS, NIPPLES & BUSHINGS SHALL BE GALVANIZED.
3. ORIENT FIRE LIGHTS ON POLE SO VISIBLE BY FIRE TRUCK DRIVER.

BRITISH COLUMBIA | Ministry of Transportation and Infrastructure


NOT TO SCALE

No.	Revision	Date
F		
E	LED LAMP	APR 20
D	GENERAL REVISIONS	APR 17
C	LUMINAIRE MODEL No. UPDATED	OCT 03
B	NEW DRAWING NUMBER	OCT 97
A	DRAWING NUMBER REVISED	AUG 95

FIRE SIGNAL INDICATION LIGHT INSTALLATION DETAIL

Date: **18/11/94** Approved: **E.L.** **(Signature on File)**
Chief Highway Engineer

SPECIFICATION DRAWING No.
SP635-2.3.10

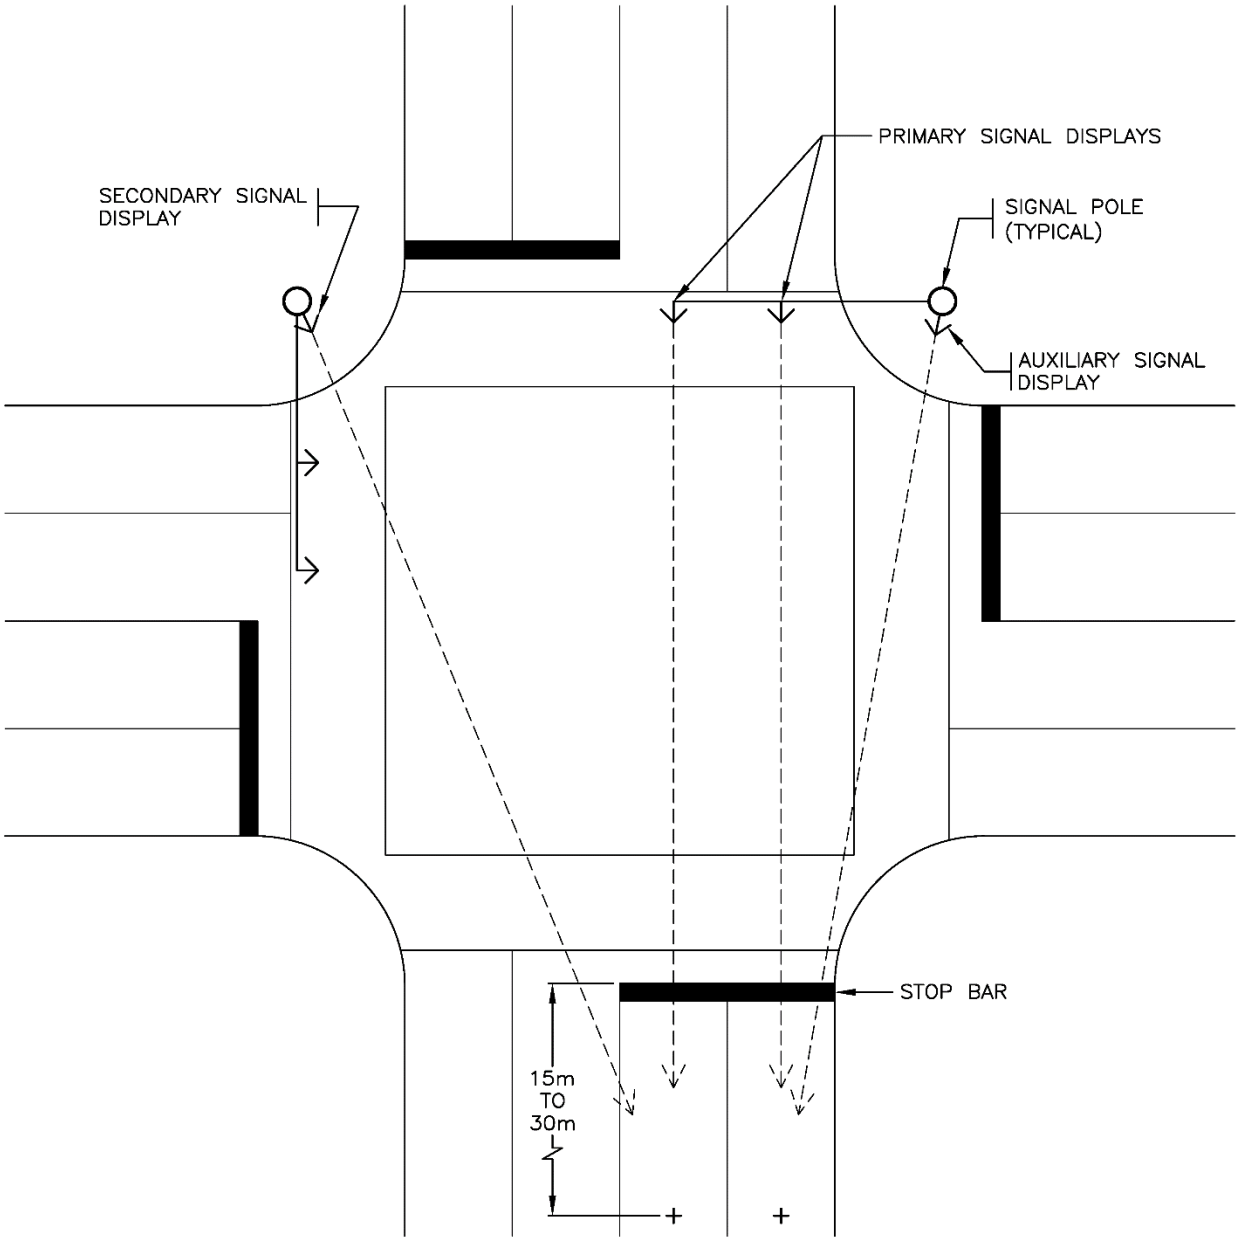

NOTES

1. DESIGNER SHALL REVIEW SIGNAL HEAD AIMING PRIOR TO SIGNAL START UP.
2. SIGNAL HEADS SHALL BE VISIBLE FROM THE MINIMUM DISTANCE SHOWN IN THE TAC MANUAL OF UNIFORM TRAFFIC CONTROL DEVICES.

NOT TO SCALE


BRITISH COLUMBIA Ministry of Transportation and Infrastructure

No.	Revision	Date
F		
E		
D		
C		
B	AUXILIARY SIGNAL HEAD	APR 20
A	GENERAL REVISIONS	APR 17

SIGNAL HEAD AIMING DIAGRAM

Date 14/11/03 Approved D.N. (Signature on File) Chief Engineer

SPECIFICATION DRAWING No. SP635-2.3.11

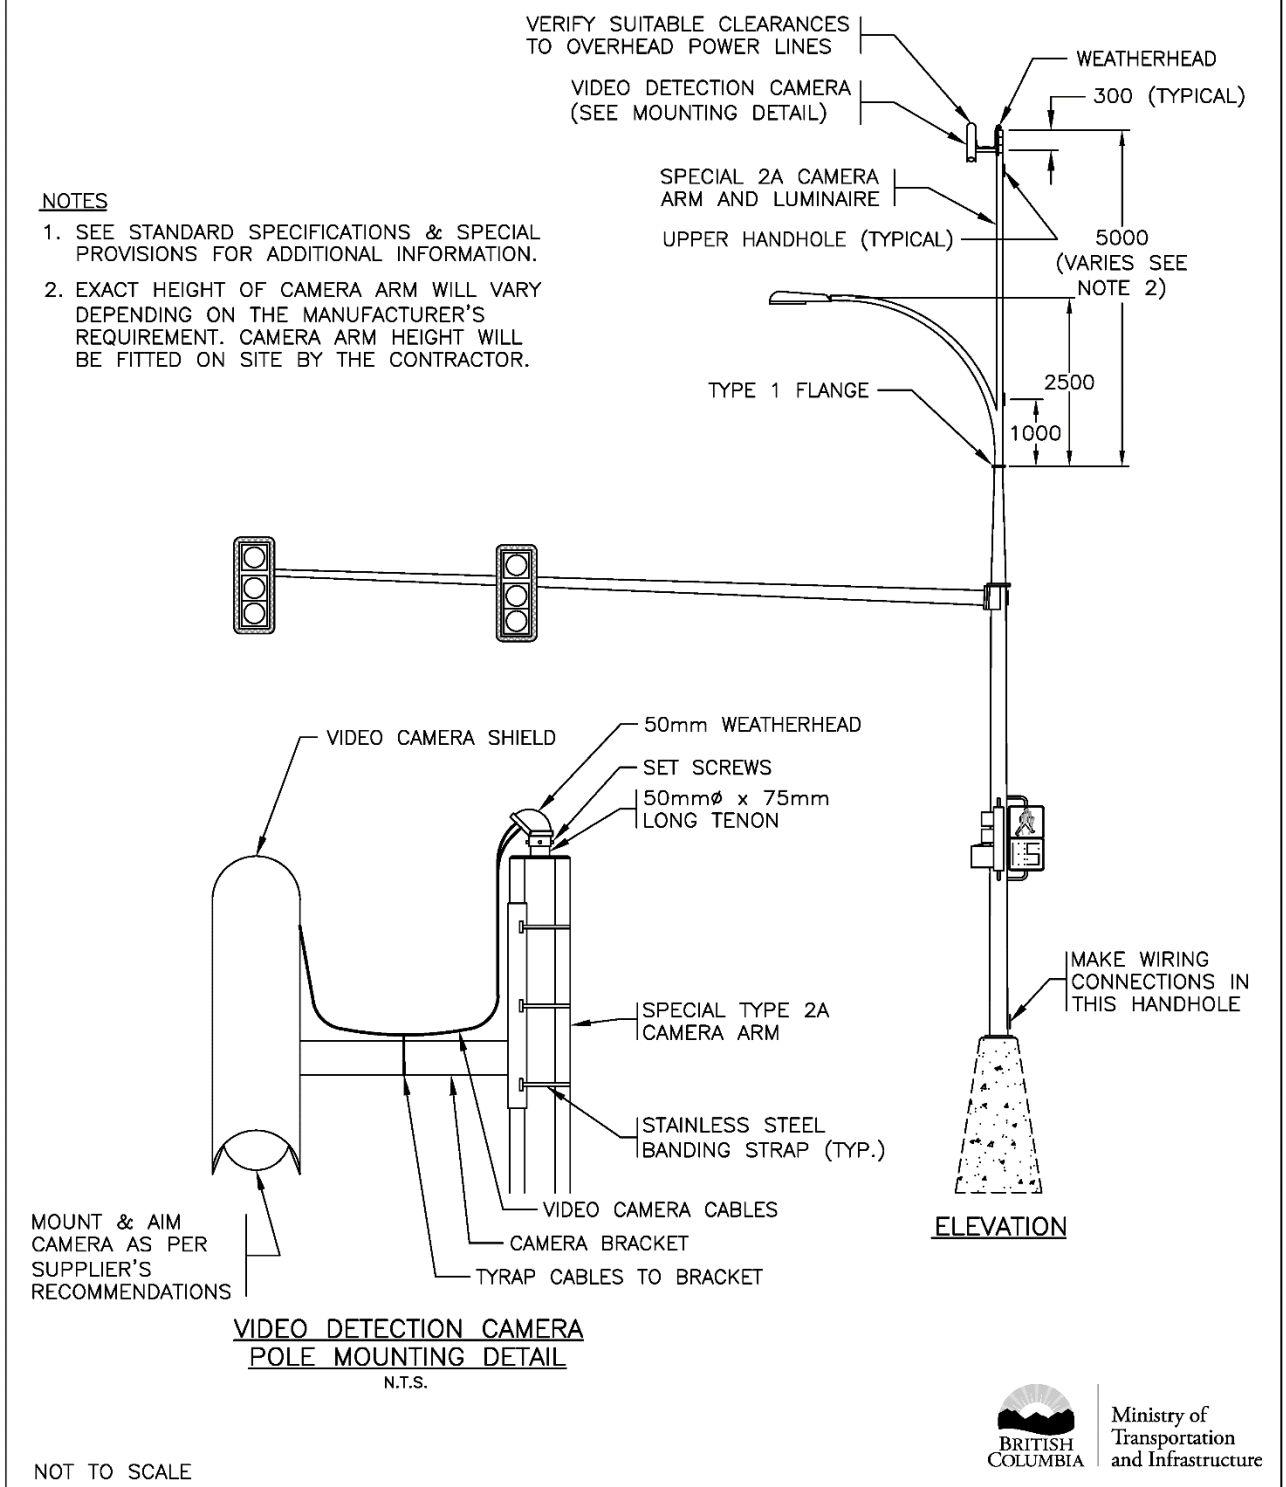

NOTES

1. SEE STANDARD SPECIFICATIONS & SPECIAL PROVISIONS FOR ADDITIONAL INFORMATION.
2. EXACT HEIGHT OF CAMERA ARM WILL VARY DEPENDING ON THE MANUFACTURER'S REQUIREMENT. CAMERA ARM HEIGHT WILL BE FITTED ON SITE BY THE CONTRACTOR.

VIDEO DETECTION CAMERA POLE MOUNTING DETAIL
N.T.S.

NOT TO SCALE

BRITISH COLUMBIA | Ministry of Transportation and Infrastructure

No.	Revision	Date
F		
E		
D		
C		
B	NOTE 2 REVISION	APR 20
A	GENERAL REVISIONS	APR 17

VIDEO DETECTION INSTALLATION DETAIL ON SPECIAL 2A ARM


Date Approved

14/11/03 **D.N. (Signature on File)**

Chief Engineer

SPECIFICATION DRAWING No.

SP635–2.3.12

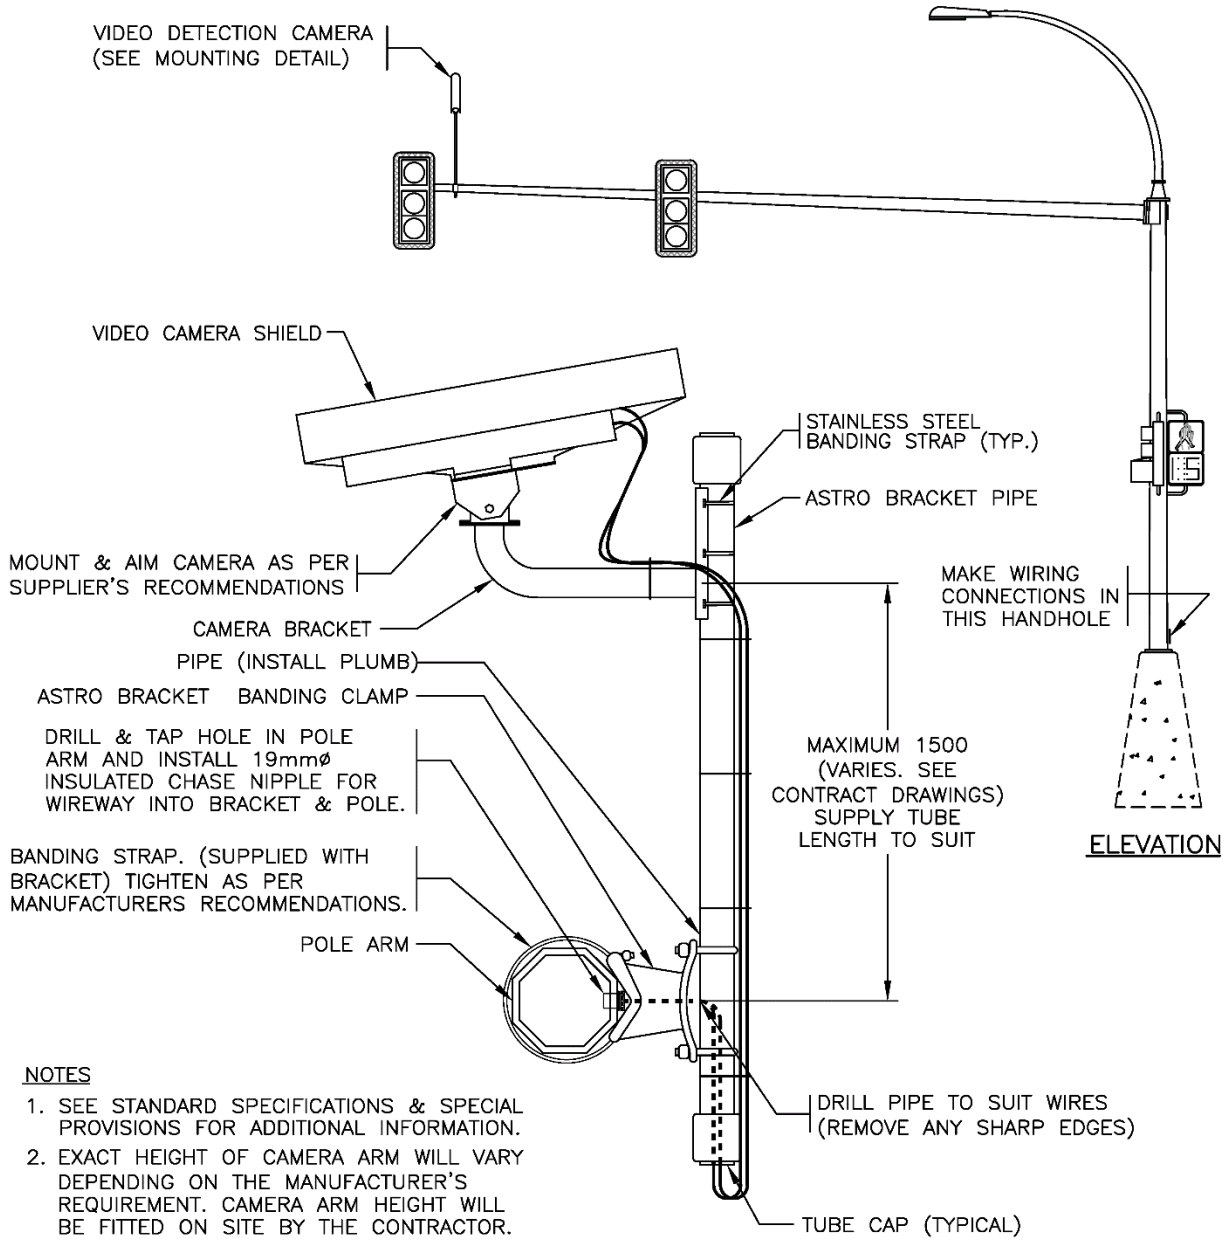

NOTES

1. SEE STANDARD SPECIFICATIONS & SPECIAL PROVISIONS FOR ADDITIONAL INFORMATION.
2. EXACT HEIGHT OF CAMERA ARM WILL VARY DEPENDING ON THE MANUFACTURER'S REQUIREMENT. CAMERA ARM HEIGHT WILL BE FITTED ON SITE BY THE CONTRACTOR.

VIDEO DETECTOR CAMERA SIGNAL ARM MOUNTING DETAIL

N.T.S.

BRITISH COLUMBIA | Ministry of Transportation and Infrastructure


NOT TO SCALE

No.	Revision	Date
F		
E		
D		
C		
B	NOTE 2 ADDED	APR 20
A	GENERAL REVISIONS	APR 17

VIDEO DETECTION INSTALLATION DETAIL ON SIGNAL ARM

Date: **14/11/03** Approved: **D.N. (Signature on File)** Chief Engineer

SPECIFICATION DRAWING No. SP635–2.3.13

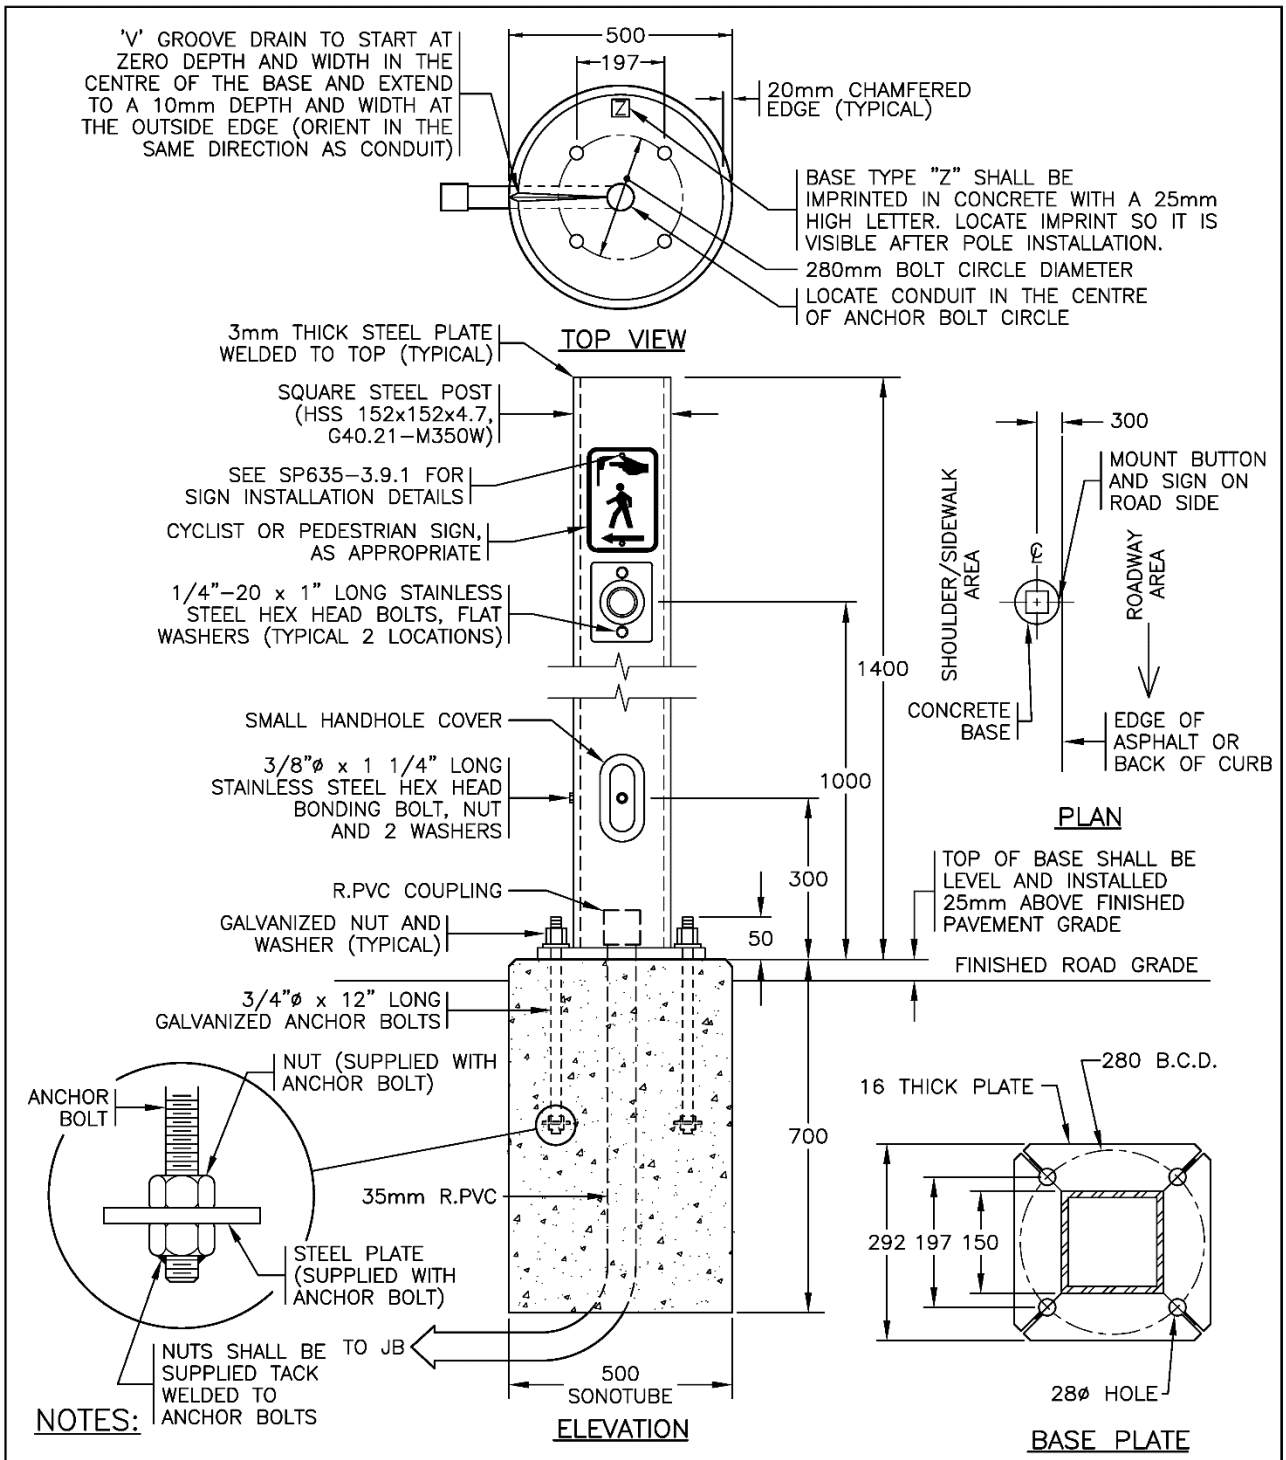

NOTES:

1. SEE STANDARD SPECIFICATIONS & SPECIAL PROVISIONS FOR ADDITIONAL INFORMATION.
2. POST TO BE HOT DIP GALVANIZED AFTER FABRICATION.
3. CONCRETE BASE TO BE 30MPa BEFORE POST INSTALLATION.
4. ALL DIMENSIONS ARE IN MILLIMETRES UNLESS OTHERWISE NOTED.

NOT TO SCALE

BRITISH COLUMBIA — Ministry of Transportation and Infrastructure

No.	Revision	Date
F		
E		
D		
C		
B	GENERAL REVISIONS	APR 20
A	GENERAL REVISIONS	APR 17

PUSHBUTTON POST INSTALLATION DETAILS

Date Approved

09/02/16 D.N. (Signature on File)

Chief Highway Engineer

SPECIFICATION DRAWING No.

SP635–2.3.14