

## BICYCLE MARKING PLACEMENT

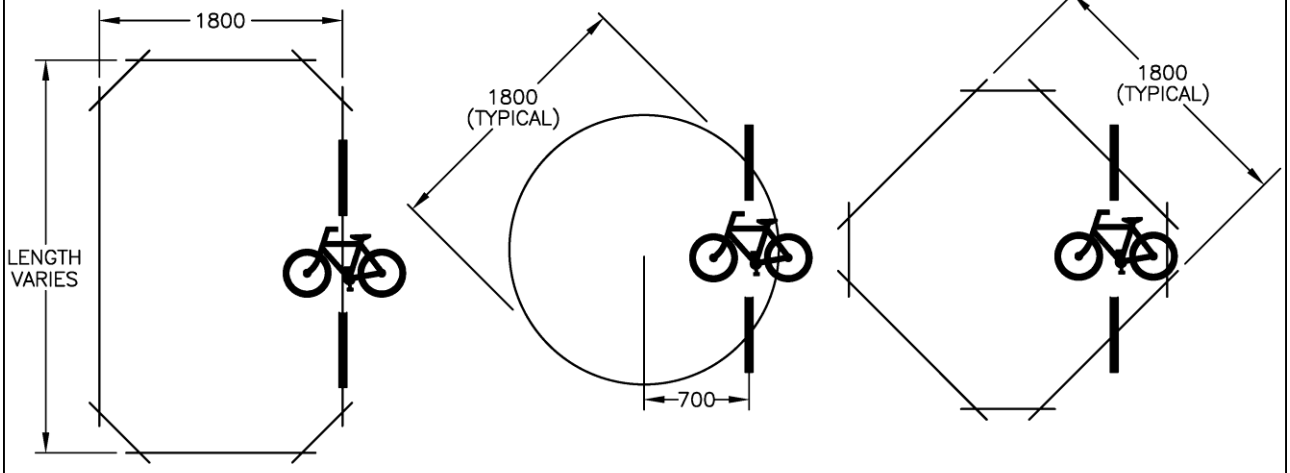


RECTANGLE ROUND DIAMOND

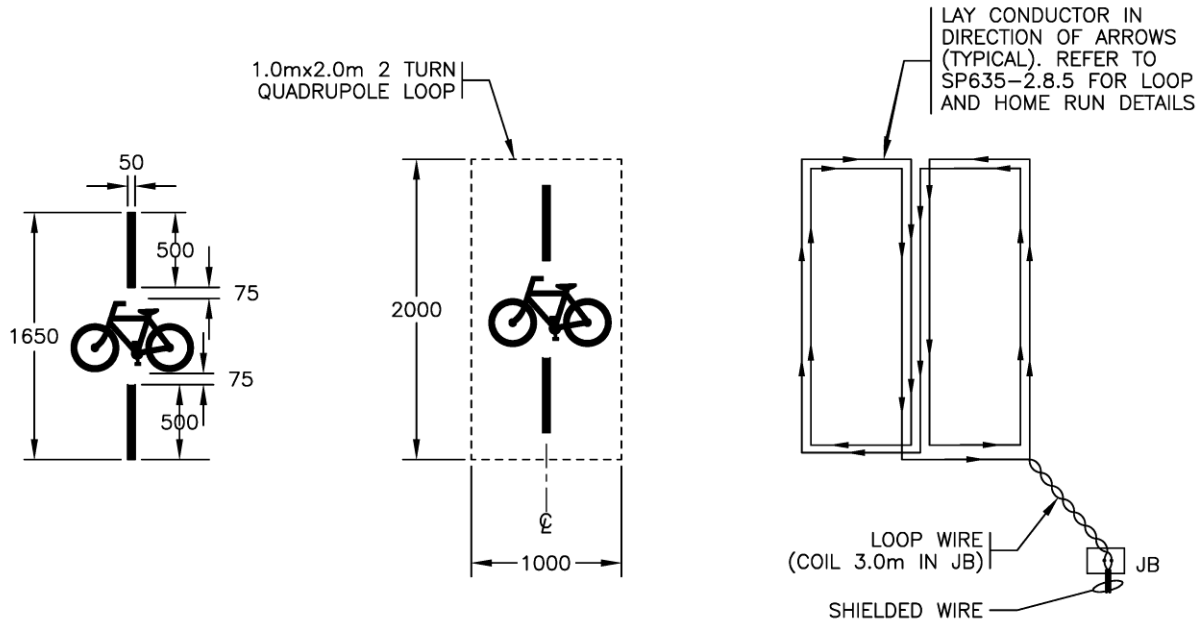


BICYCLE DETECTOR MARKINGS DIMENSIONS

BICYCLE DETECTOR LOOP WITH BICYCLE MARKING PLACEMENT

BICYCLE QUADRUPOLE LOOP WINDING DETAIL

NOTE

1. PAINT MARKING AND POSITIONING TO BE CONFIRMED WITH MINISTRY REPRESENTATIVE.

NOT TO SCALE

BRITISH COLUMBIA Ministry of Transportation and Infrastructure

| No. | Revision | Date |
|---|---|---|
| F | | |
| E | | |
| D | | |
| C | | |
| B | | |
| A | | |

BICYCLE DETECTOR LOOPS AND MARKINGS


Date Approved

09/02/16 D.N. (Signature on File)

Chief Highway Engineer

SPECIFICATION DRAWING No.

SP635–2.3.15

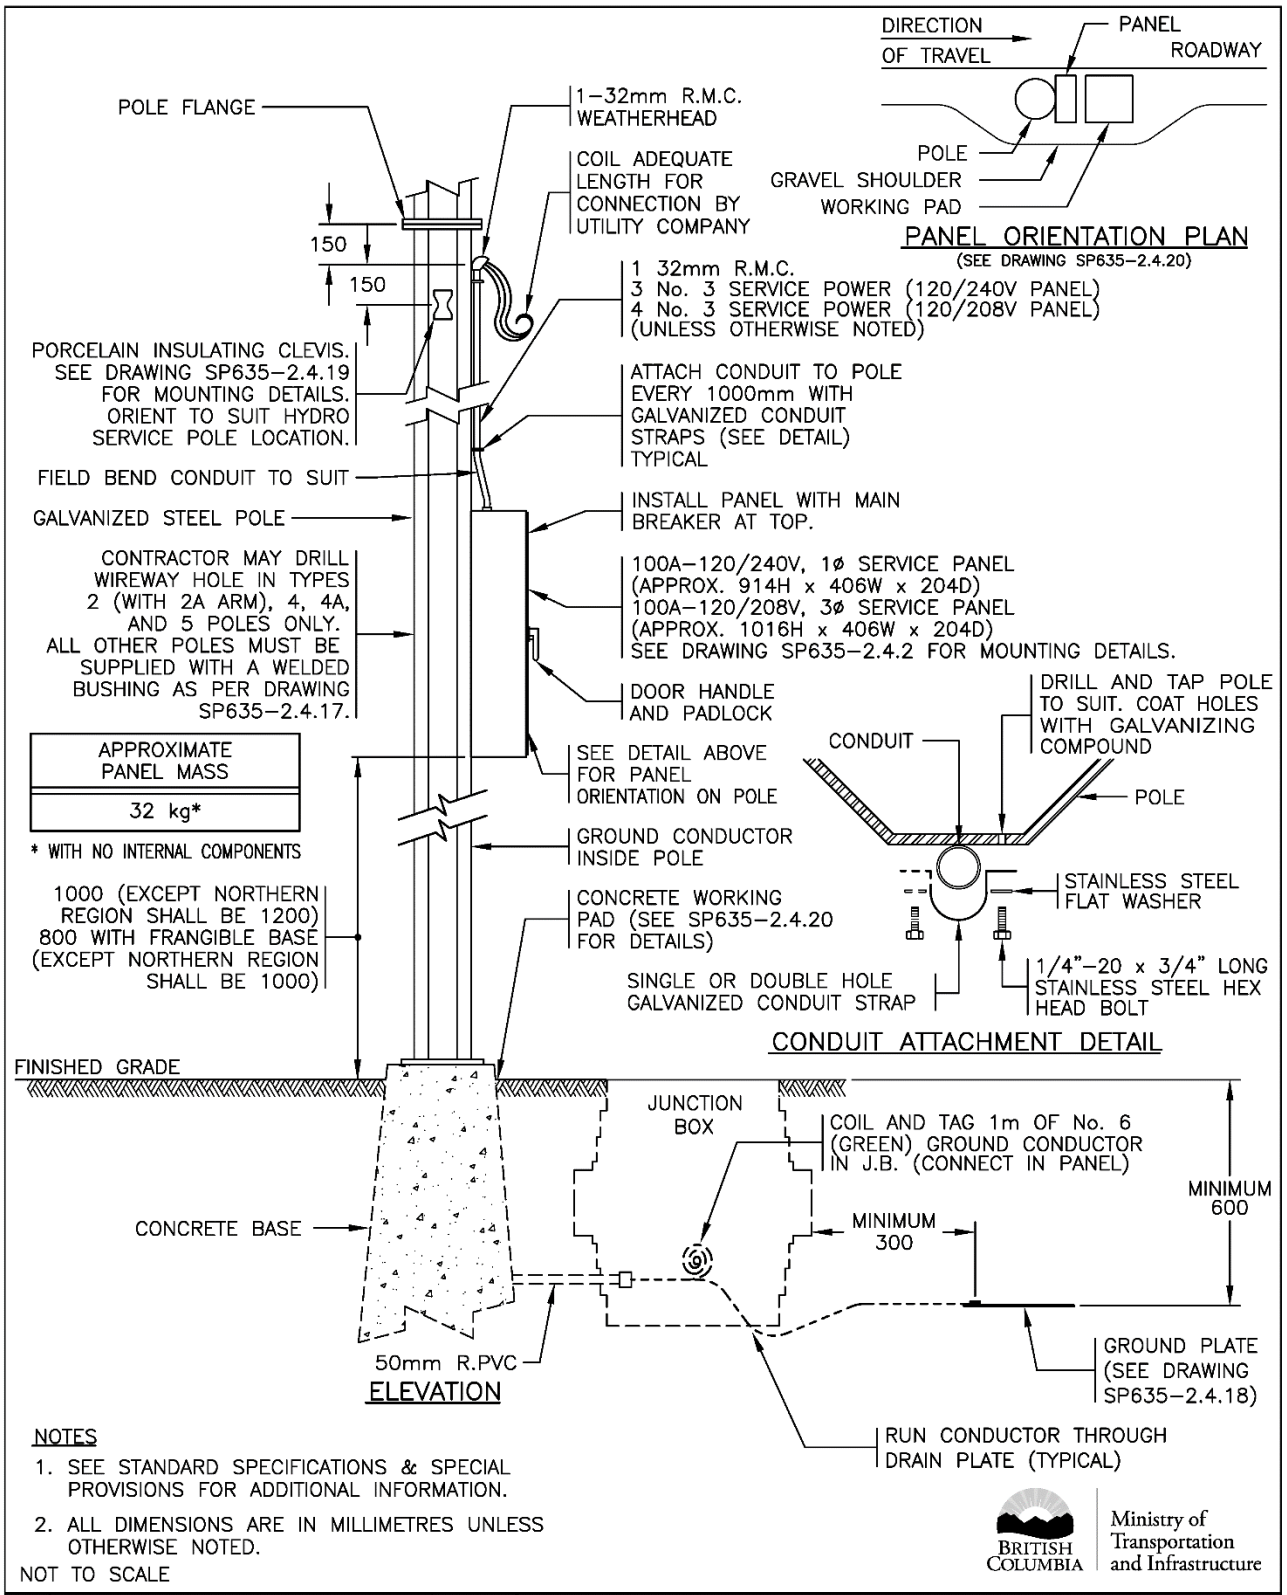


NOTES

1. SEE STANDARD SPECIFICATIONS & SPECIAL PROVISIONS FOR ADDITIONAL INFORMATION.
2. ALL DIMENSIONS ARE IN MILLIMETRES UNLESS OTHERWISE NOTED.

NOT TO SCALE

BRITISH COLUMBIA — Ministry of Transportation and Infrastructure

| No. | Revision | Date |
|---|---|---|
| G | GENERAL REVISIONS | APR 20 |
| F | GENERAL REVISIONS | APR 17 |
| E | GENERAL REVISIONS | FEB 16 |
| D | MOUNTING HEIGHT REVISED | AUG 99 |
| C | MOUNTING HEIGHT CHANGED TO FINISHED GRADE & PANEL ORIENTATION DETAIL ADDED | NOV 98 |

# 100A – OVERHEAD SERVICE INSTALLATION DETAILS


Date Approved

**05/02/16 D.N. (Signature on File)**

Chief Highway Engineer

SPECIFICATION DRAWING No.

SP635-2.4.1

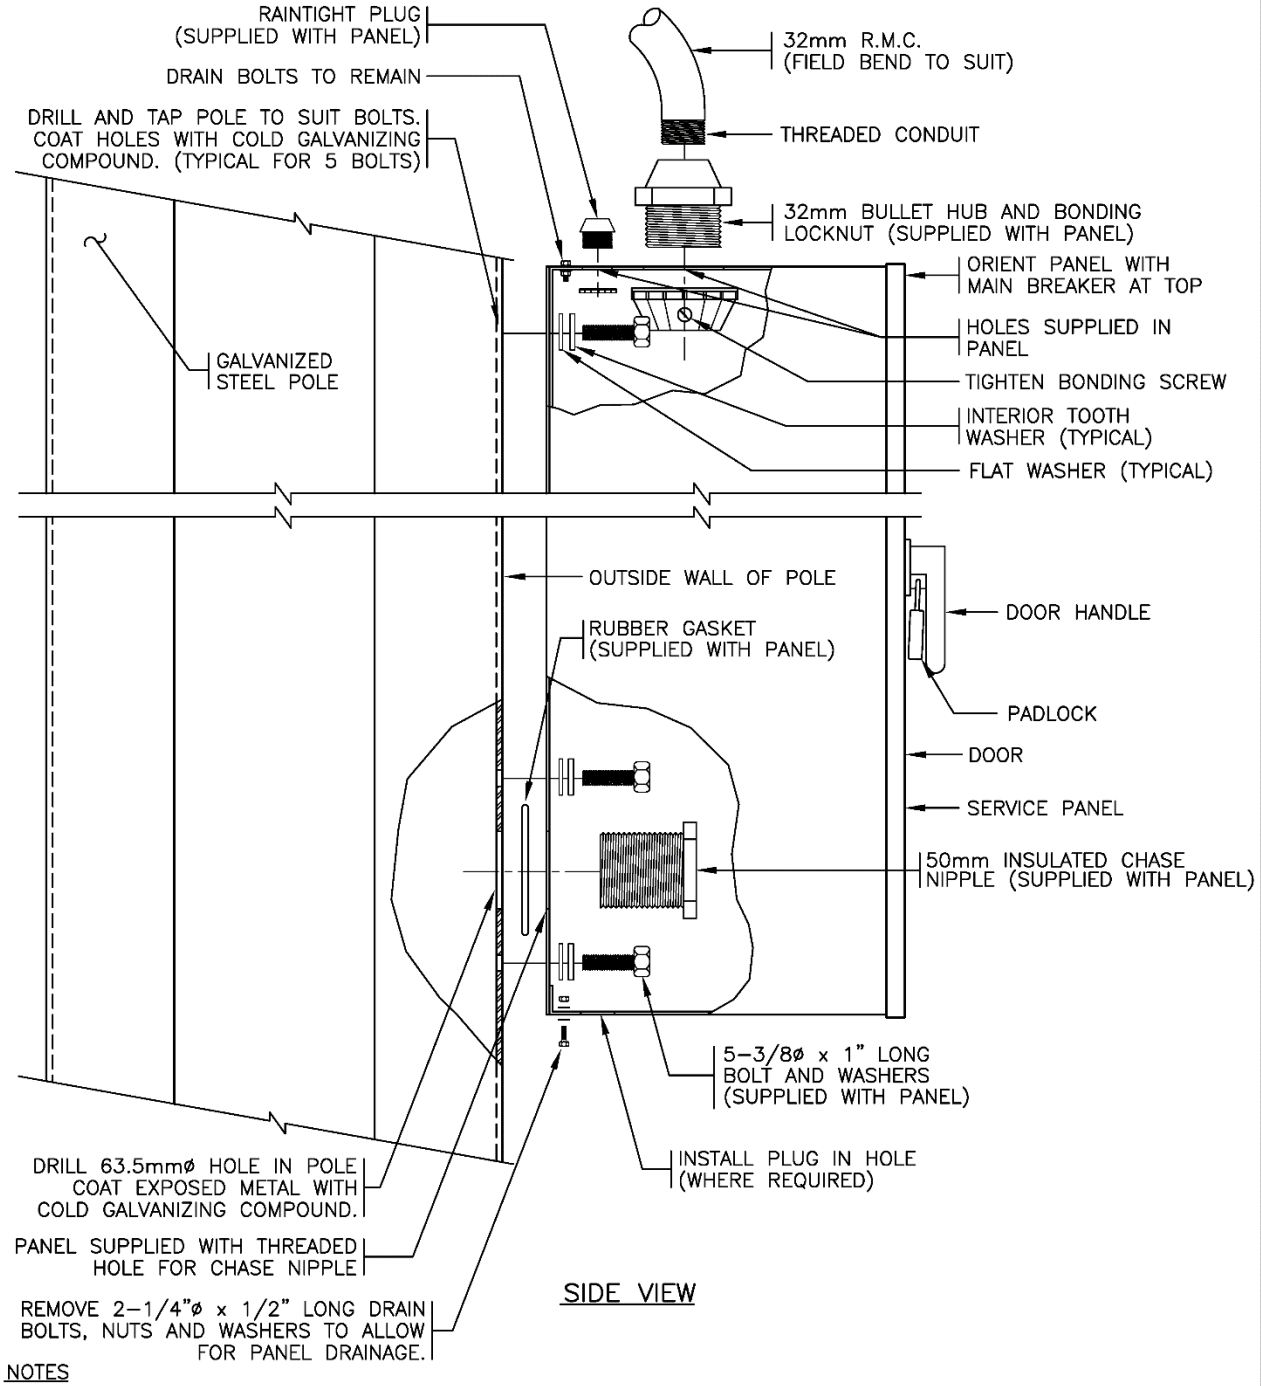


NOTES

1. SEE STANDARD SPECIFICATIONS & SPECIAL PROVISIONS FOR ADDITIONAL INFORMATION.
2. ALL DIMENSIONS ARE IN MILLIMETRES UNLESS OTHERWISE NOTED.
3. PANEL ASSEMBLY AND INSTALLATION INSTRUCTIONS SUPPLIED WITH PANEL.

NOT TO SCALE

BRITISH COLUMBIA Ministry of Transportation and Infrastructure

| No. | Revision | Date |
|---|---|---|
| F | | |
| E | | |
| D | GENERAL REVISIONS | FEB 16 |
| C | BONDING LOCKNUT ADDED | AUG 96 |
| B | GROUND CONDUIT DELETED | AUG 95 |
| A | GENERAL REVISIONS | AUG 94 |

# 100A – OVERHEAD SERVICE PANEL INSTALLATION DETAILS


Date Approved

**05/02/16 D.N. (Signature on File)**

Chief Highway Engineer

SPECIFICATION DRAWING No.

SP635-2.4.2

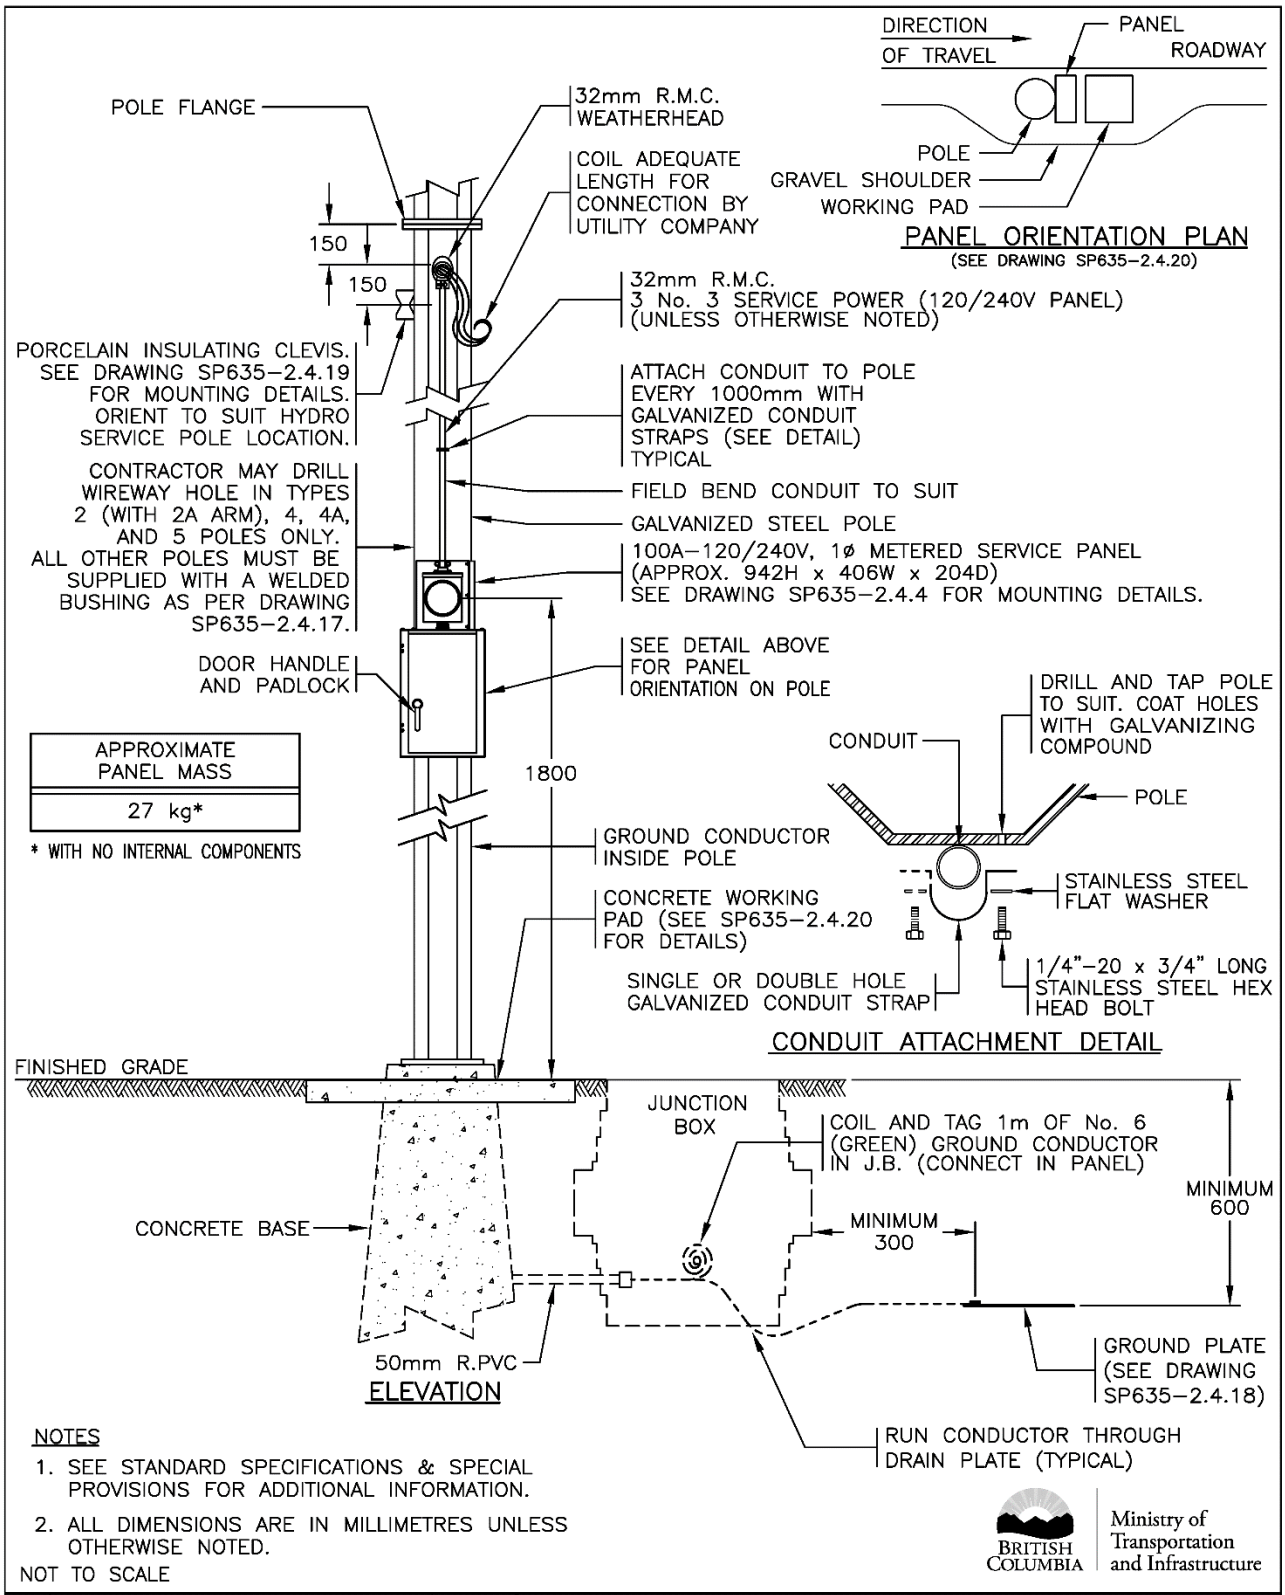


NOTES

1. SEE STANDARD SPECIFICATIONS & SPECIAL PROVISIONS FOR ADDITIONAL INFORMATION.
2. ALL DIMENSIONS ARE IN MILLIMETRES UNLESS OTHERWISE NOTED.

NOT TO SCALE

BRITISH COLUMBIA — Ministry of Transportation and Infrastructure

| No. | Revision | Date |
|---|---|---|
| E | | |
| D | | |
| C | GENERAL REVISIONS | APR 20 |
| B | GENERAL REVISIONS | APR 17 |
| A | DRAWING REVISED TO OVERHEAD 120/240V SINGLE PHASE SERVICE (METERED) | FEB 16 |

# 100A – 120/240V SINGLE PHASE OVERHEAD SERVICE INSTALLATION DETAILS (METERED)


Date Approved

**05/02/16 D.N. (Signature on File)**

Chief Highway Engineer

SPECIFICATION DRAWING No.

SP635-2.4.3

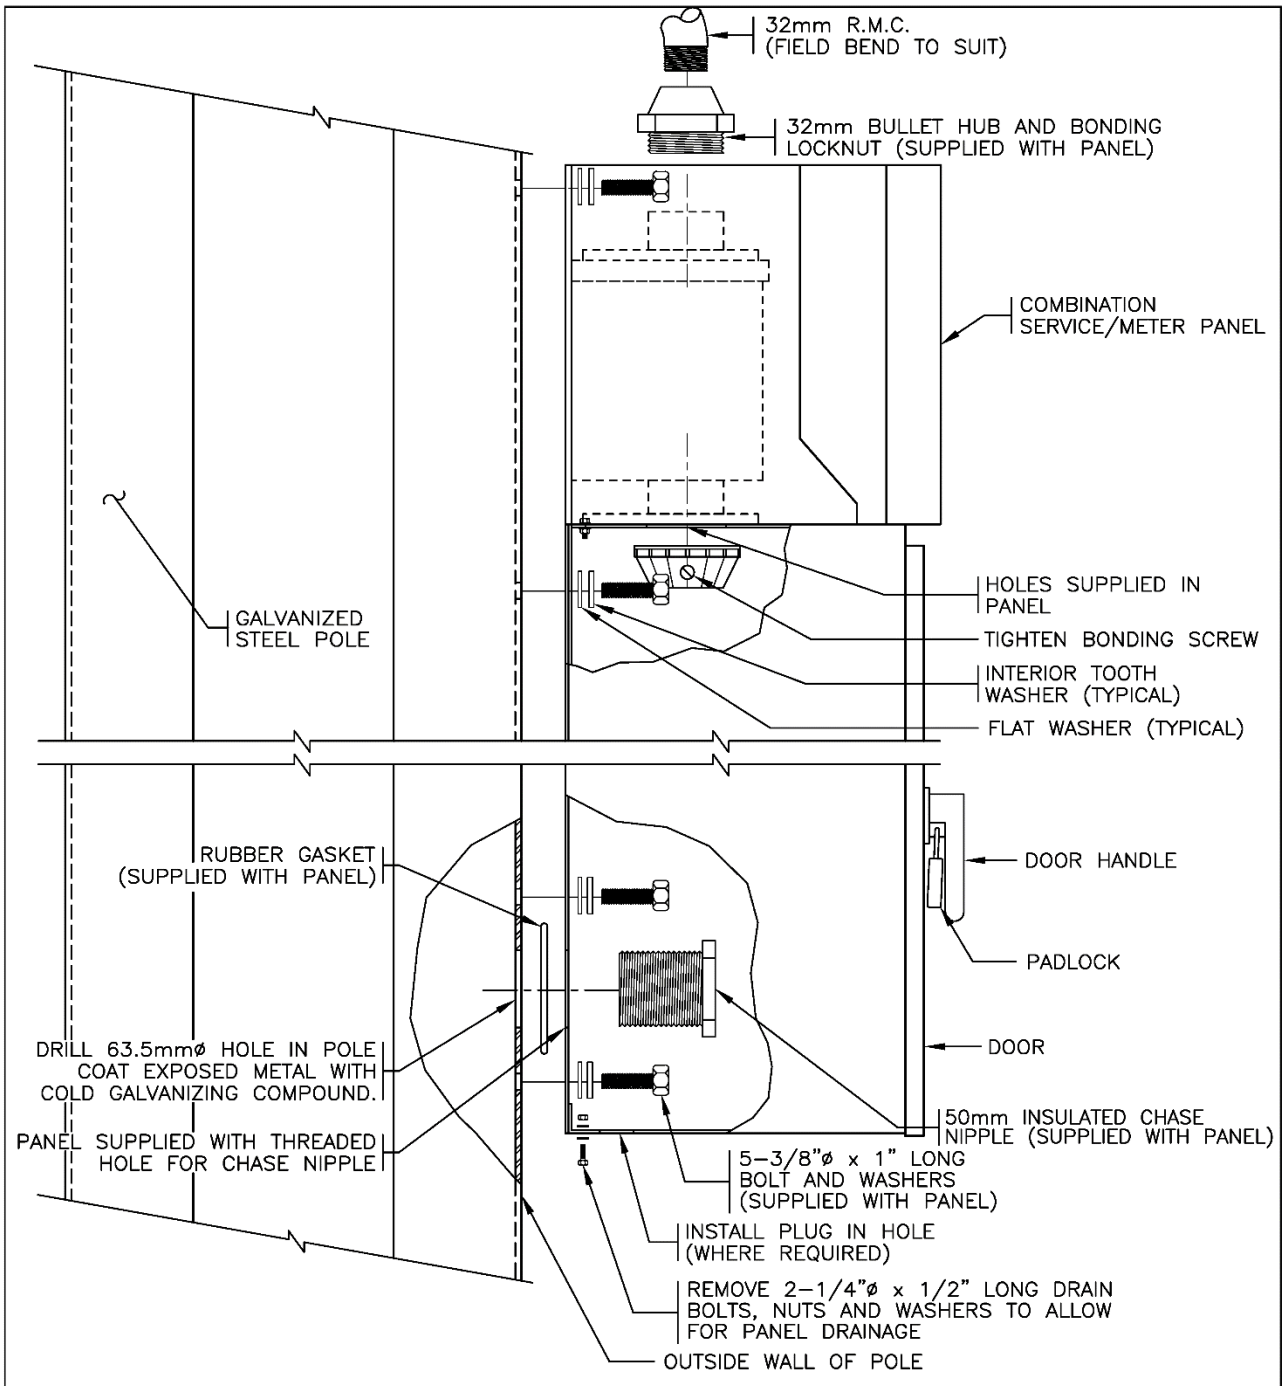


SIDE VIEW

NOTES

1. SEE STANDARD SPECIFICATIONS & SPECIAL PROVISIONS FOR ADDITIONAL INFORMATION.
2. ALL DIMENSIONS ARE IN MILLIMETRES UNLESS OTHERWISE NOTED.
3. PANEL ASSEMBLY AND INSTALLATION INSTRUCTIONS SUPPLIED WITH PANEL.

NOT TO SCALE

BRITISH COLUMBIA Ministry of Transportation and Infrastructure


| No. | Revision | Date |
|---|---|---|
| E | | |
| D | | |
| C | | |
| B | | |
| A | DRAWING REVISED TO OVERHEAD 120/240V SINGLE PHASE SERVICE (METERED) | FEB 16 |

# 100A – 120/240V SINGLE PHASE OVERHEAD SERVICE PANEL INSTALLATION DETAILS (METERED)

Date Approved

**05/02/16 D.N. (Signature on File)**
Chief Highway Engineer

SPECIFICATION DRAWING No.
SP635–2.4.4

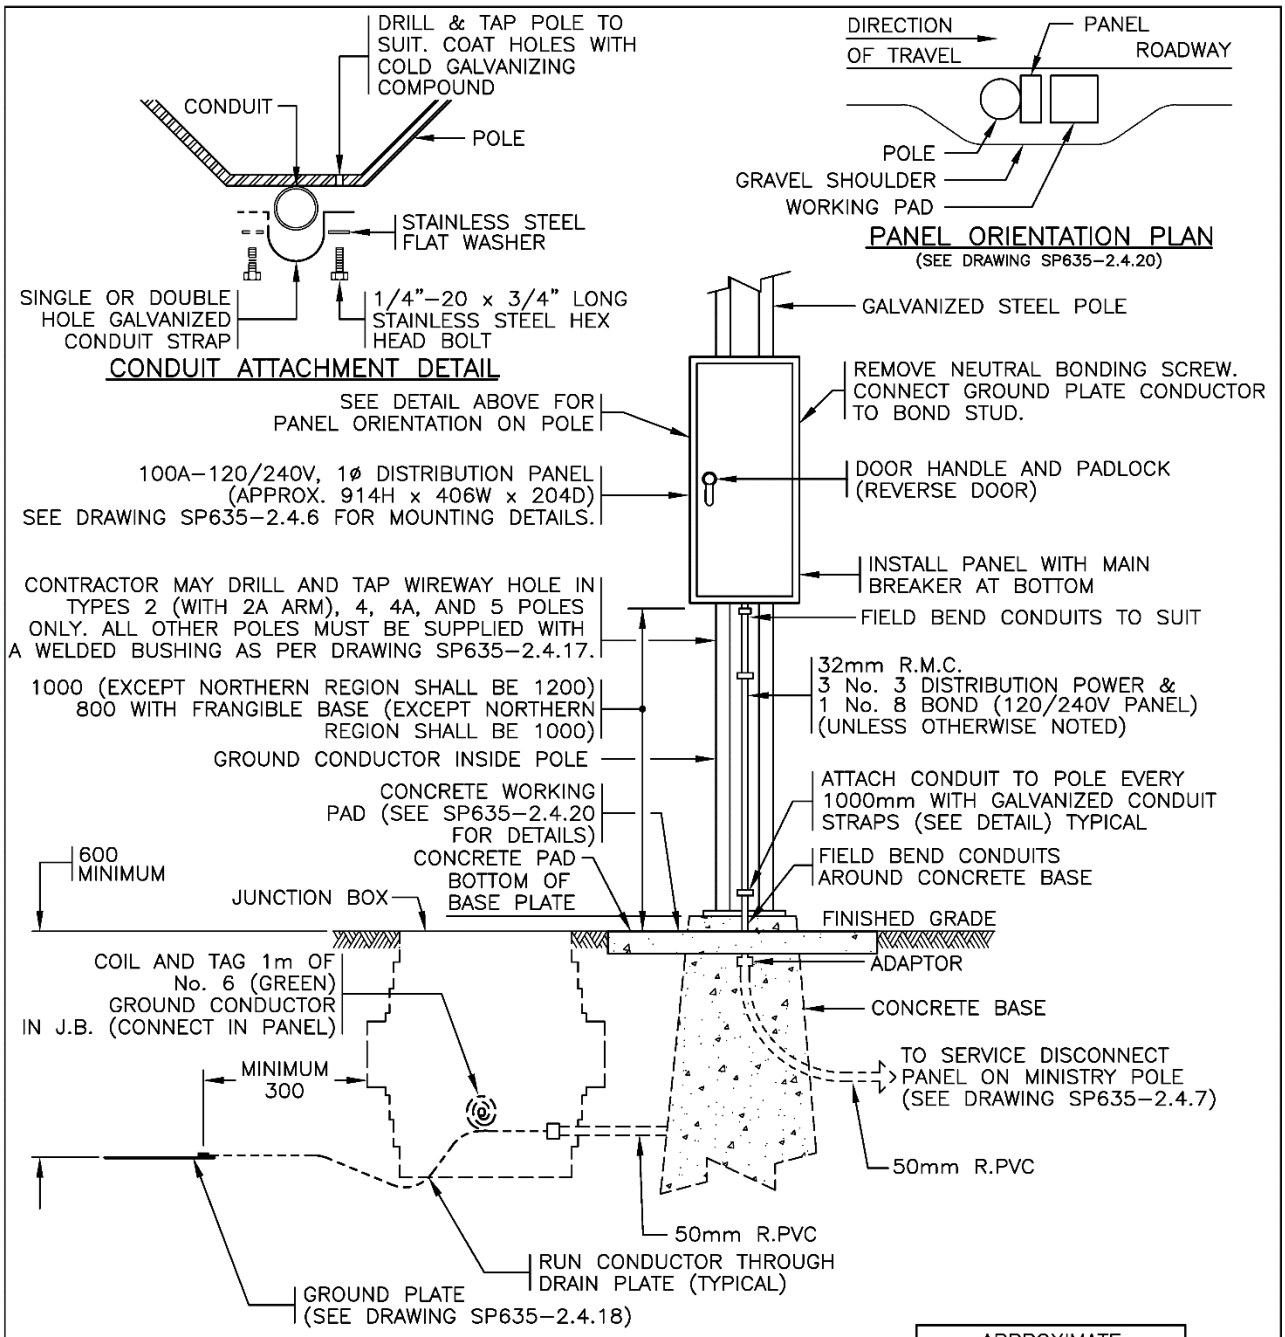


| APPROXIMATE PANEL MASS |
|---|
| 30 kg* |

* WITH NO INTERNAL COMPONENTS

NOTES

1. SEE STANDARD SPECIFICATIONS & SPECIAL PROVISIONS FOR ADDITIONAL INFORMATION.
2. ALL DIMENSIONS ARE IN MILLIMETRES UNLESS OTHERWISE NOTED.

NOT TO SCALE

BRITISH COLUMBIA Ministry of Transportation and Infrastructure

| No. | Revision | Date |
|---|---|---|
| G | GENERAL REVISIONS | APR 20 |
| E | GENERAL REVISIONS | FEB 16 |
| D | BOND CONDUCTOR & GROUND PLATE CONDUCTOR CONNECTION CLARIFIED, MOUNTING HEIGHT REVISED | AUG 99 |
| C | MOUNTING HEIGHT CHANGED TO FINISHED GRADE & PANEL ORIENTATION DETAIL ADDED | NOV 98 |

# 100A – UNDERGOUND DISTRIBUTION INSTALLATION DETAILS


Date Approved

**05/02/16 D.N. (Signature on File)**

Chief Highway Engineer

SPECIFICATION DRAWING No.

SP635–2.4.5

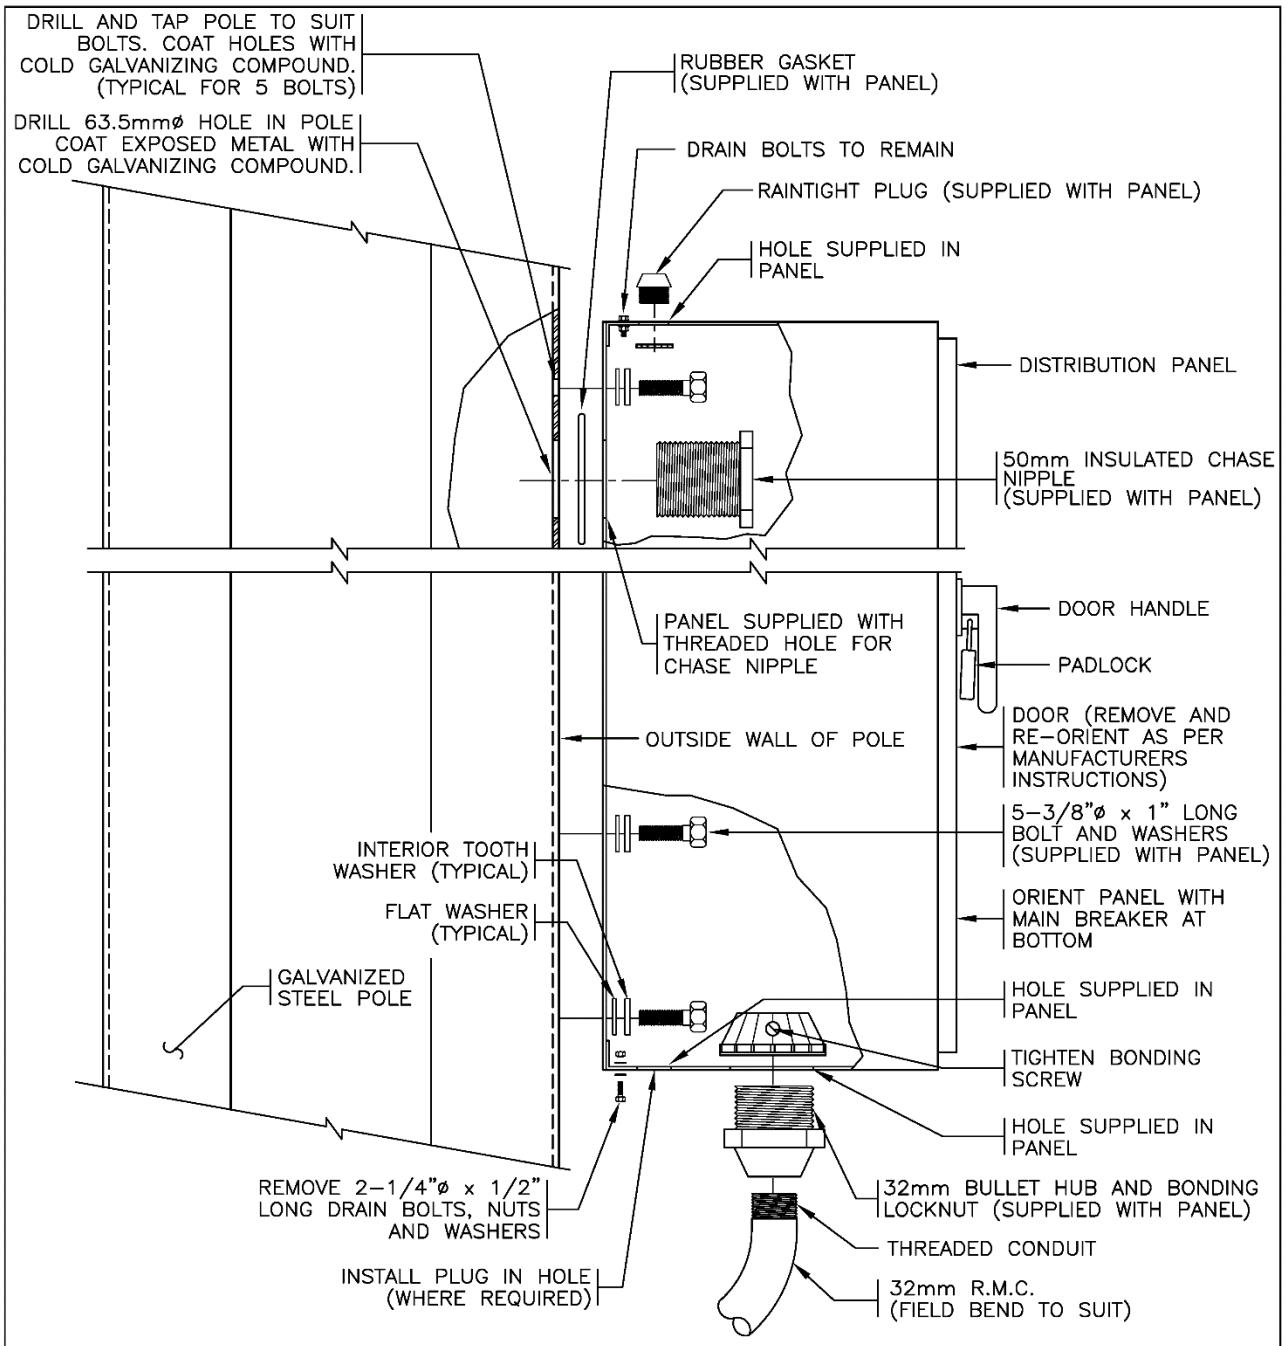


NOTES

1. SEE STANDARD SPECIFICATIONS & SPECIAL PROVISIONS FOR ADDITIONAL INFORMATION.
2. ALL DIMENSIONS ARE IN MILLIMETRES UNLESS OTHERWISE NOTED.
3. PANEL ASSEMBLY AND INSTALLATION INSTRUCTIONS SUPPLIED WITH PANEL.

SIDE VIEW

NOT TO SCALE

BRITISH COLUMBIA | Ministry of Transportation and Infrastructure

| No. | Revision | Date |
|---|---|---|
| F | | |
| E | | |
| D | GENERAL REVISIONS | FEB 16 |
| C | BONDING LOCKNUT ADDED | AUG 96 |
| B | GROUND CONDUIT DELETED | AUG 95 |
| A | GENERAL REVISIONS | AUG 94 |

# 100A – UNDERGROUND DISTRIBUTION PANEL INSTALLATION DETAILS


Date Approved

**05/02/16 D.N. (Signature on File)**

Chief Highway Engineer

SPECIFICATION DRAWING No.

SP635-2.4.6

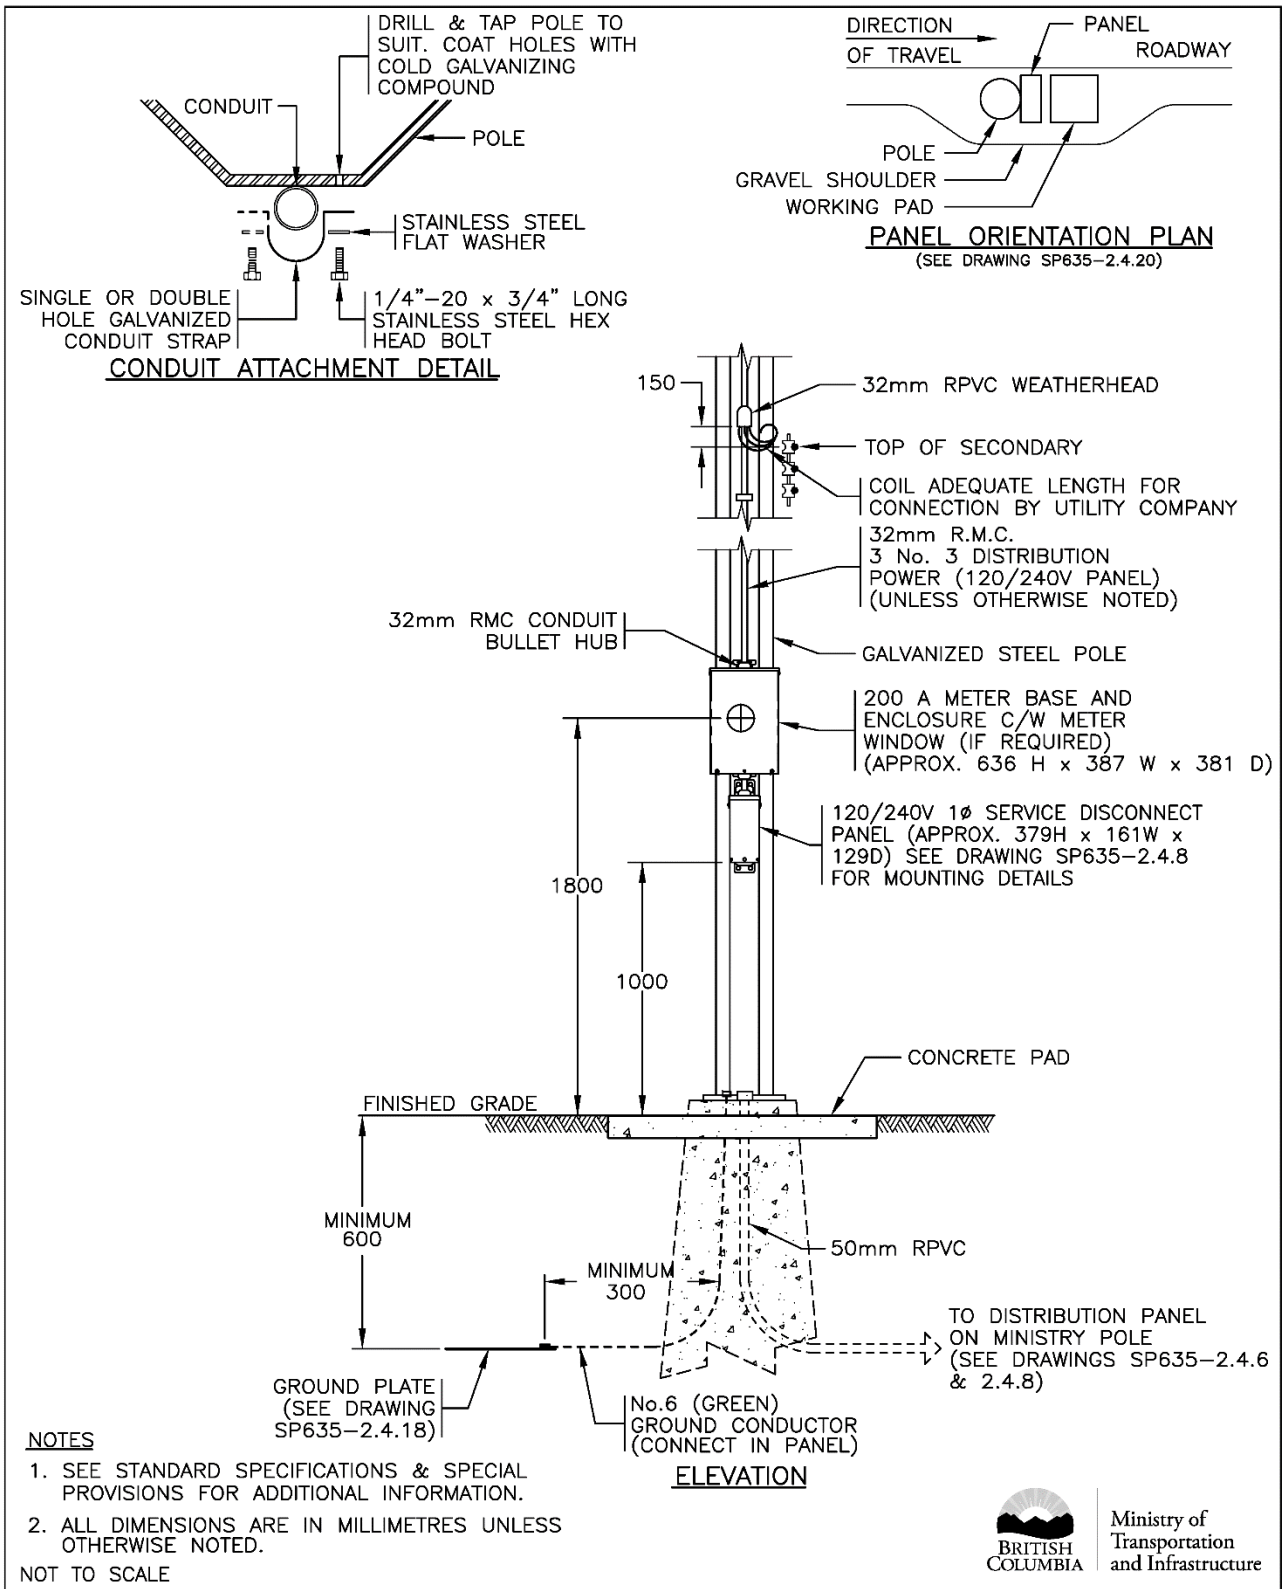


NOTES

1. SEE STANDARD SPECIFICATIONS & SPECIAL PROVISIONS FOR ADDITIONAL INFORMATION.
2. ALL DIMENSIONS ARE IN MILLIMETRES UNLESS OTHERWISE NOTED.

NOT TO SCALE

BRITISH COLUMBIA — Ministry of Transportation and Infrastructure

| No. | Revision | Date |
|---|---|---|
| F | GENERAL REVISION | APR 20 |
| E | WOOD UTILITY POLE REPLACED WITH STEEL POLE METER ENCLOSURE ADDED | FEB 16 |
| D | CONDUIT AND WEATHERHEAD RPVC | APR 05 |
| C | BOND CONDUCTORS ADDED | AUG 99 |
| B | GROUND PLATE ADDED | AUG 95 |

# 100A – DIP SERVICE DISCONNECT INSTALLATION DETAILS (METERED)


Date Approved

**05/02/16 D.N. (Signature on File)**

Chief Highway Engineer

SPECIFICATION DRAWING No.

SP635–2.4.7

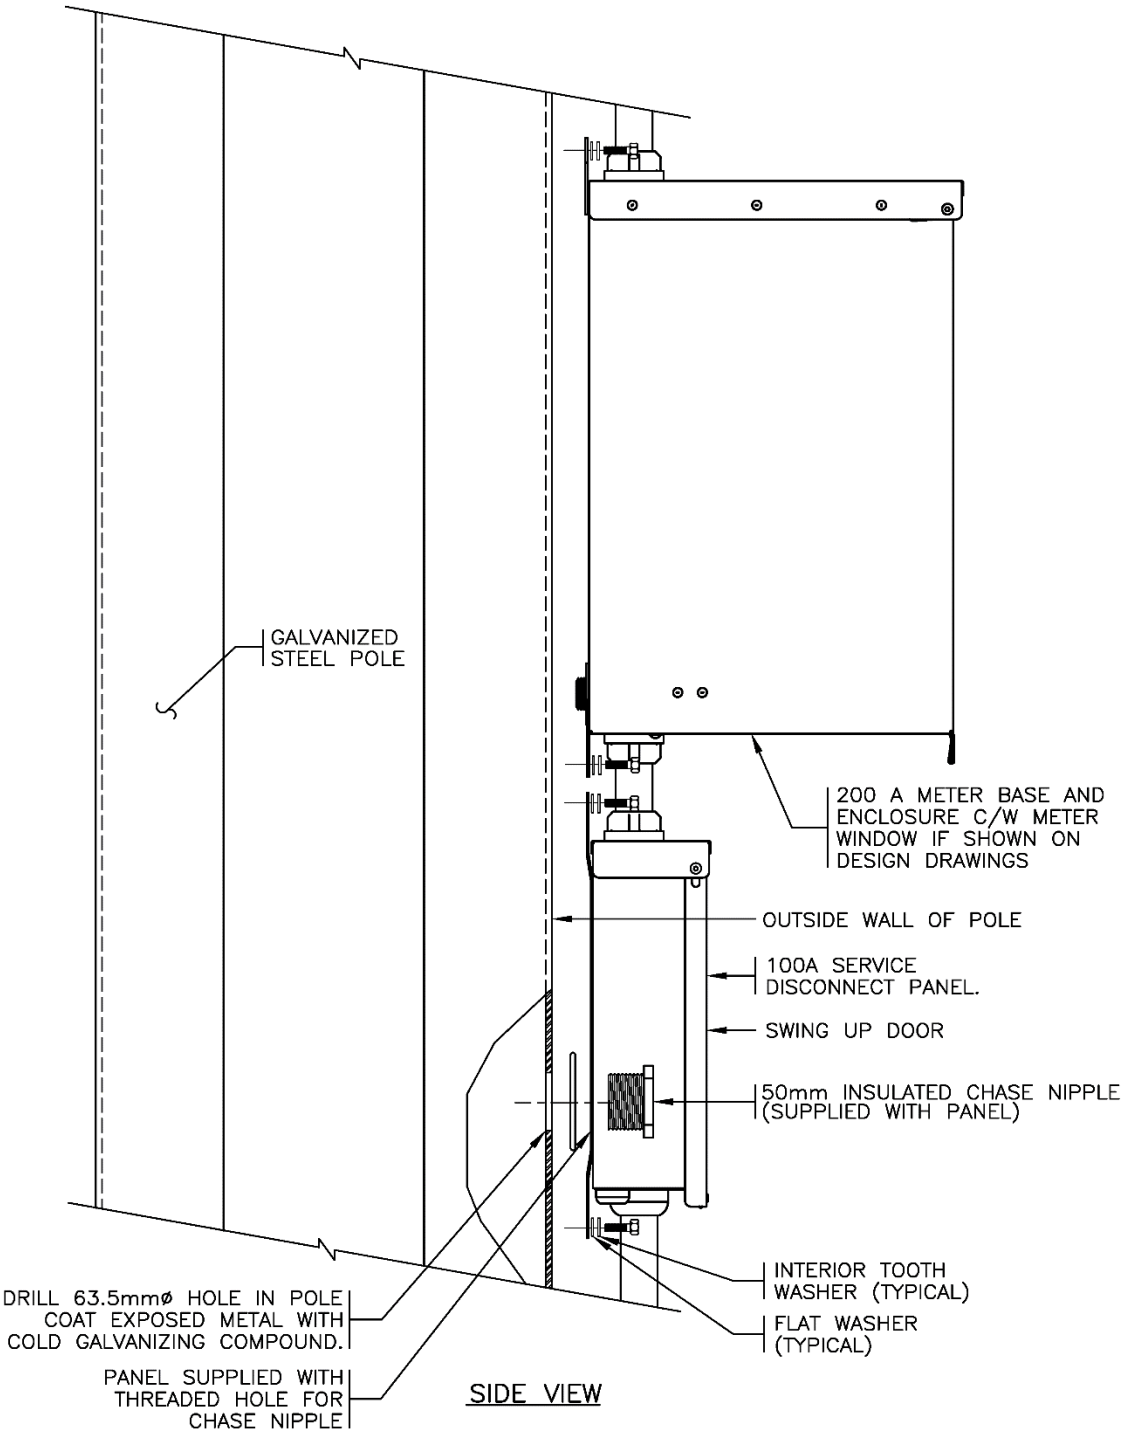


NOTES

1. SEE STANDARD SPECIFICATIONS & SPECIAL PROVISIONS FOR ADDITIONAL INFORMATION.

NOT TO SCALE

BRITISH COLUMBIA | Ministry of Transportation and Infrastructure

| No. | Revision | Date |
|---|---|---|
| E | | |
| D | WOOD UTILITY POLE REPLACED WITH STEEL POLE METER ENCLOSURE ADDED | FEB 16 |
| C | RPVC CONDUIT/ADAPTER ADDED | APR 05 |
| B | BONDING LOCKNUT ADDED | AUG 96 |
| A | GENERAL REVISIONS | AUG 94 |

# 100A – DIP SERVICE DISCONNECT & METER INSTALLATION DETAILS


Date Approved

**05/02/16 D.N. (Signature on File)**


Chief Highway Engineer

SPECIFICATION DRAWING No.


SP635–2.4.8

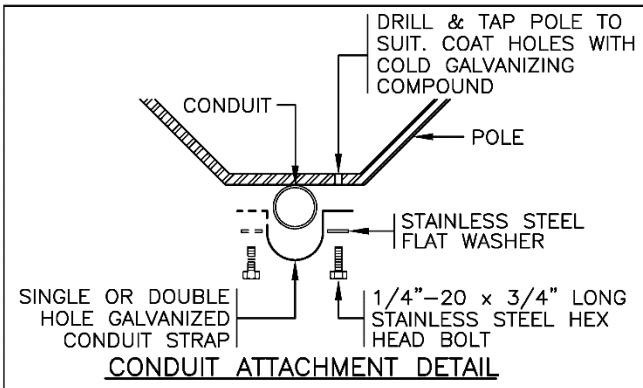


CONDUIT ATTACHMENT DETAIL

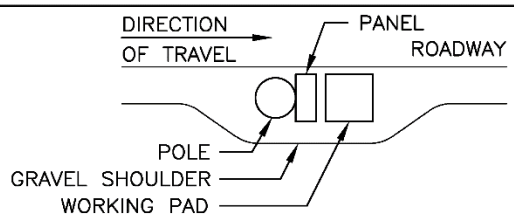


PANEL ORIENTATION PLAN
(SEE DRAWING SP635–2.4.20)

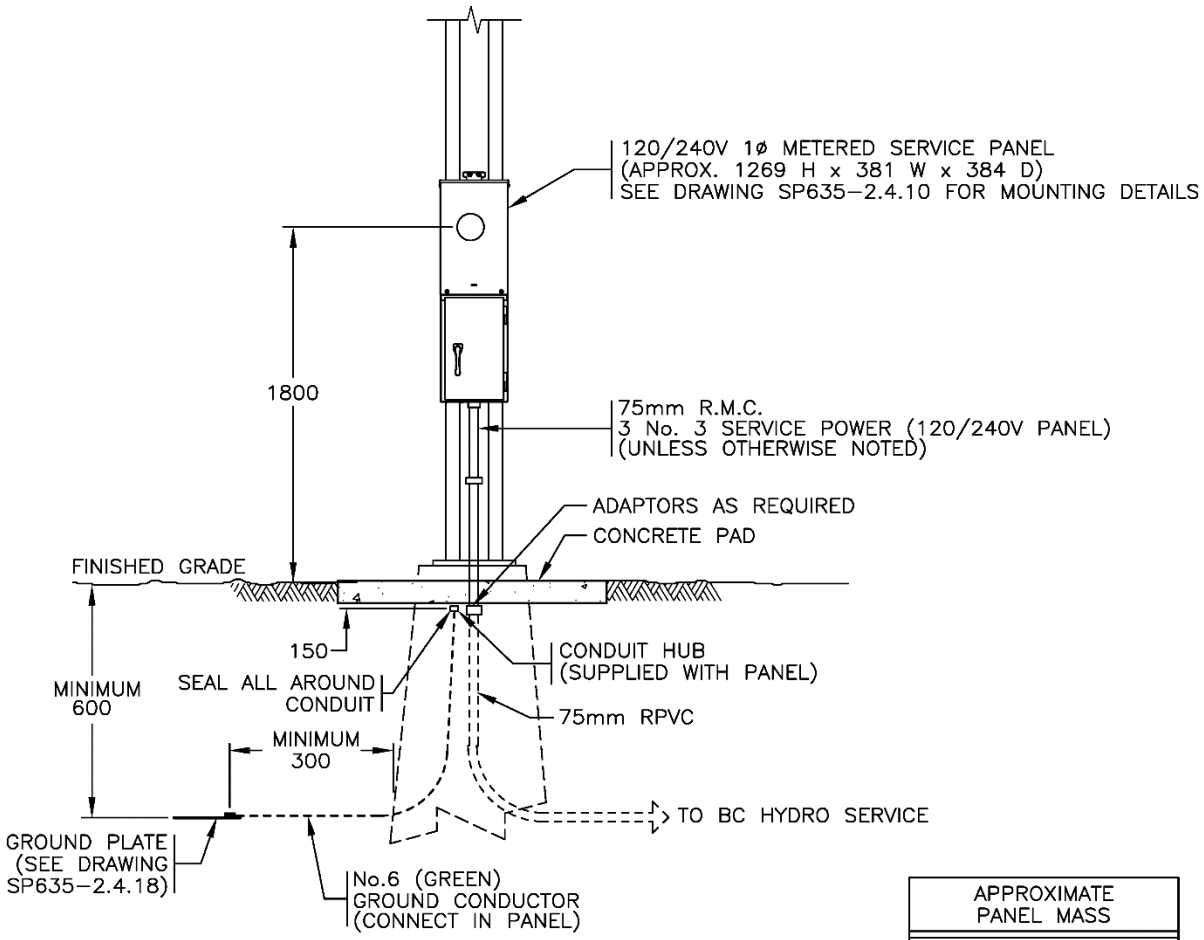


| APPROXIMATE PANEL MASS |
|---|
| 51 kg* |

* WITH NO INTERNAL COMPONENTS

NOTES

1. SEE STANDARD SPECIFICATIONS & SPECIAL PROVISIONS FOR ADDITIONAL INFORMATION.
2. ALL DIMENSIONS ARE IN MILLIMETRES UNLESS OTHERWISE NOTED.

NOT TO SCALE


BRITISH COLUMBIA Ministry of Transportation and Infrastructure

| No. | Revision | Date |
|---|---|---|
| G | GENERAL REVISIONS | APR 20 |
| F | GENERAL REVISIONS | APR 17 |
| E | DRAWINGS REVISED TO UNDERGROUND METERED SERVICE | FEB 16 |
| D | CONDUIT AND WEATHERHEAD RPVC | APR 05 |
| C | BOND CONDUCTORS ADDED | AUG 99 |
| B | GROUND PLATE ADDED | AUG 95 |

# 100A – UNDERGROUND SERVICE INSTALLATION DETAILS (METERED)

Date: **05/02/16** Approved: **D.N.** (Signature on File)
Chief Highway Engineer

SPECIFICATION DRAWING No.
SP635–2.4.9

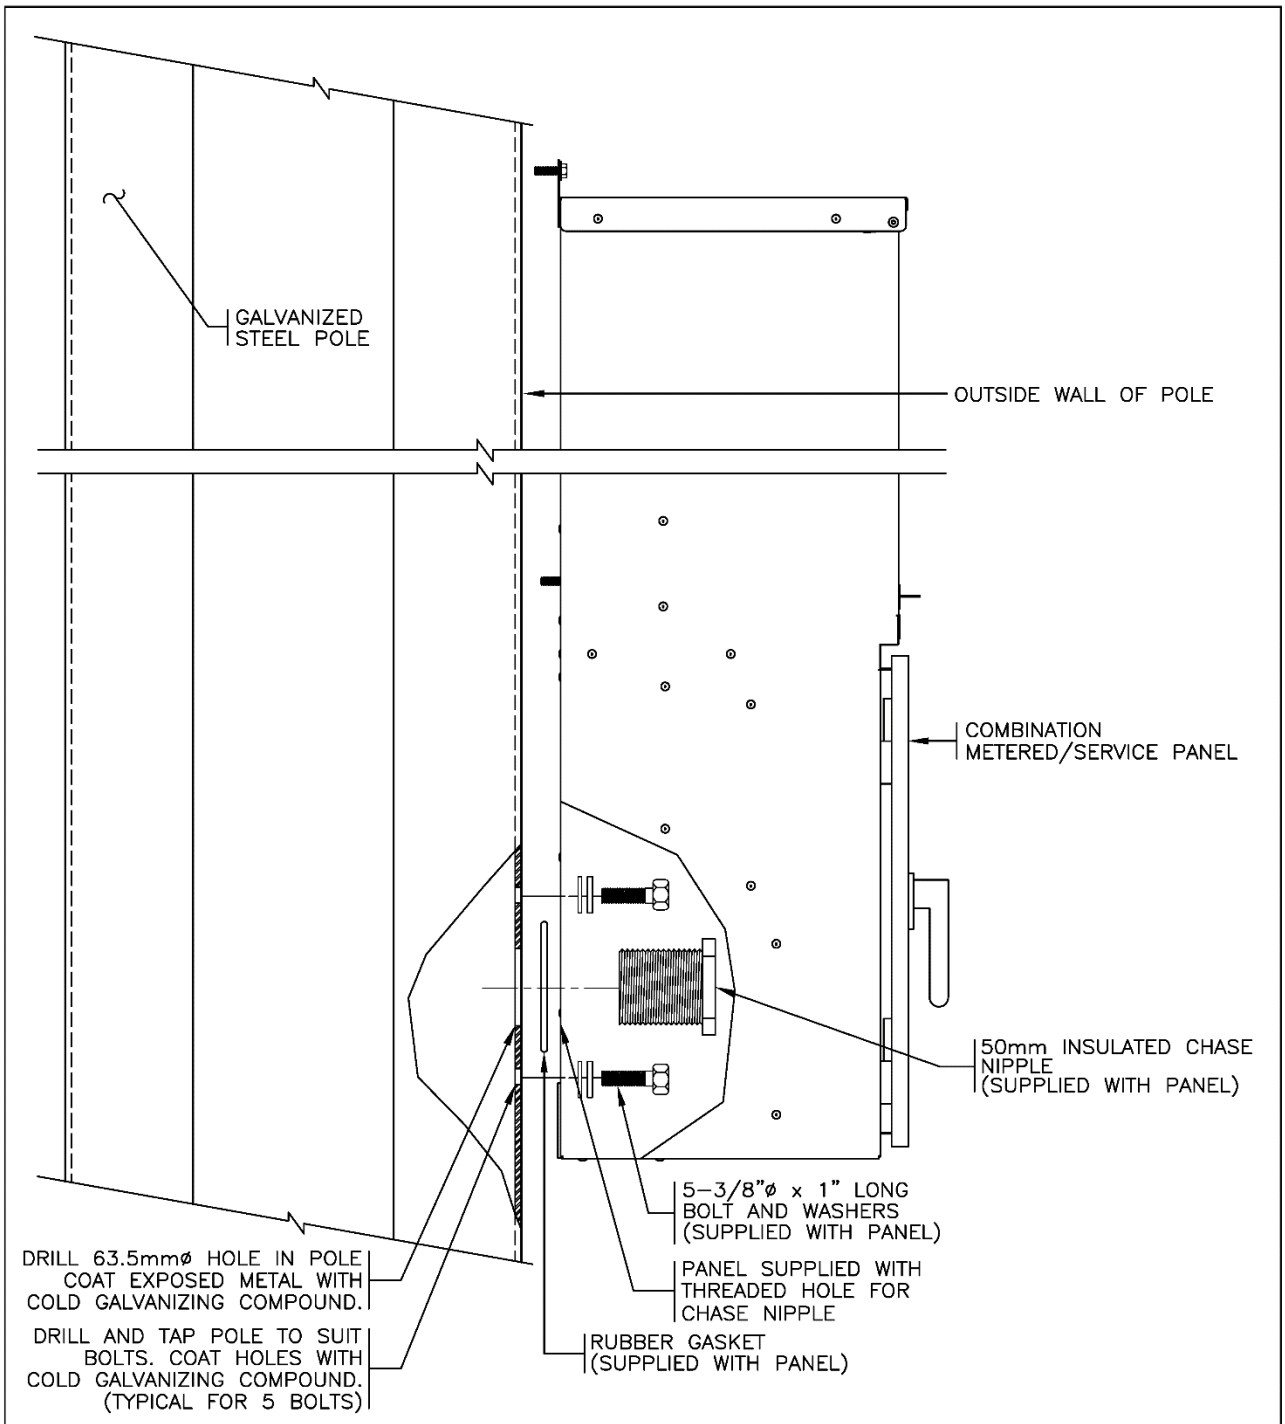


SIDE VIEW

NOTES

1. SEE STANDARD SPECIFICATIONS & SPECIAL PROVISIONS FOR ADDITIONAL INFORMATION.

NOT TO SCALE

BRITISH COLUMBIA | Ministry of Transportation and Infrastructure

| No. | Revision | Date |
|---|---|---|
| F | | |
| E | | |
| D | DRAWINGS REVISED TO UNDERGROUND METERED SERVICE | FEB 16 |
| C | RPVC CONDUIT/ADAPTER ADDED | APR 05 |
| B | BONDING LOCKNUT ADDED | AUG 96 |
| A | GENERAL REVISIONS | AUG 94 |

# 100A – UNDERGROUND SERVICE & METER PANEL INSTALLATION DETAILS


Date Approved

**05/02/16 D.N. (Signature on File)**

Chief Highway Engineer

SPECIFICATION DRAWING No.

SP635–2.4.10

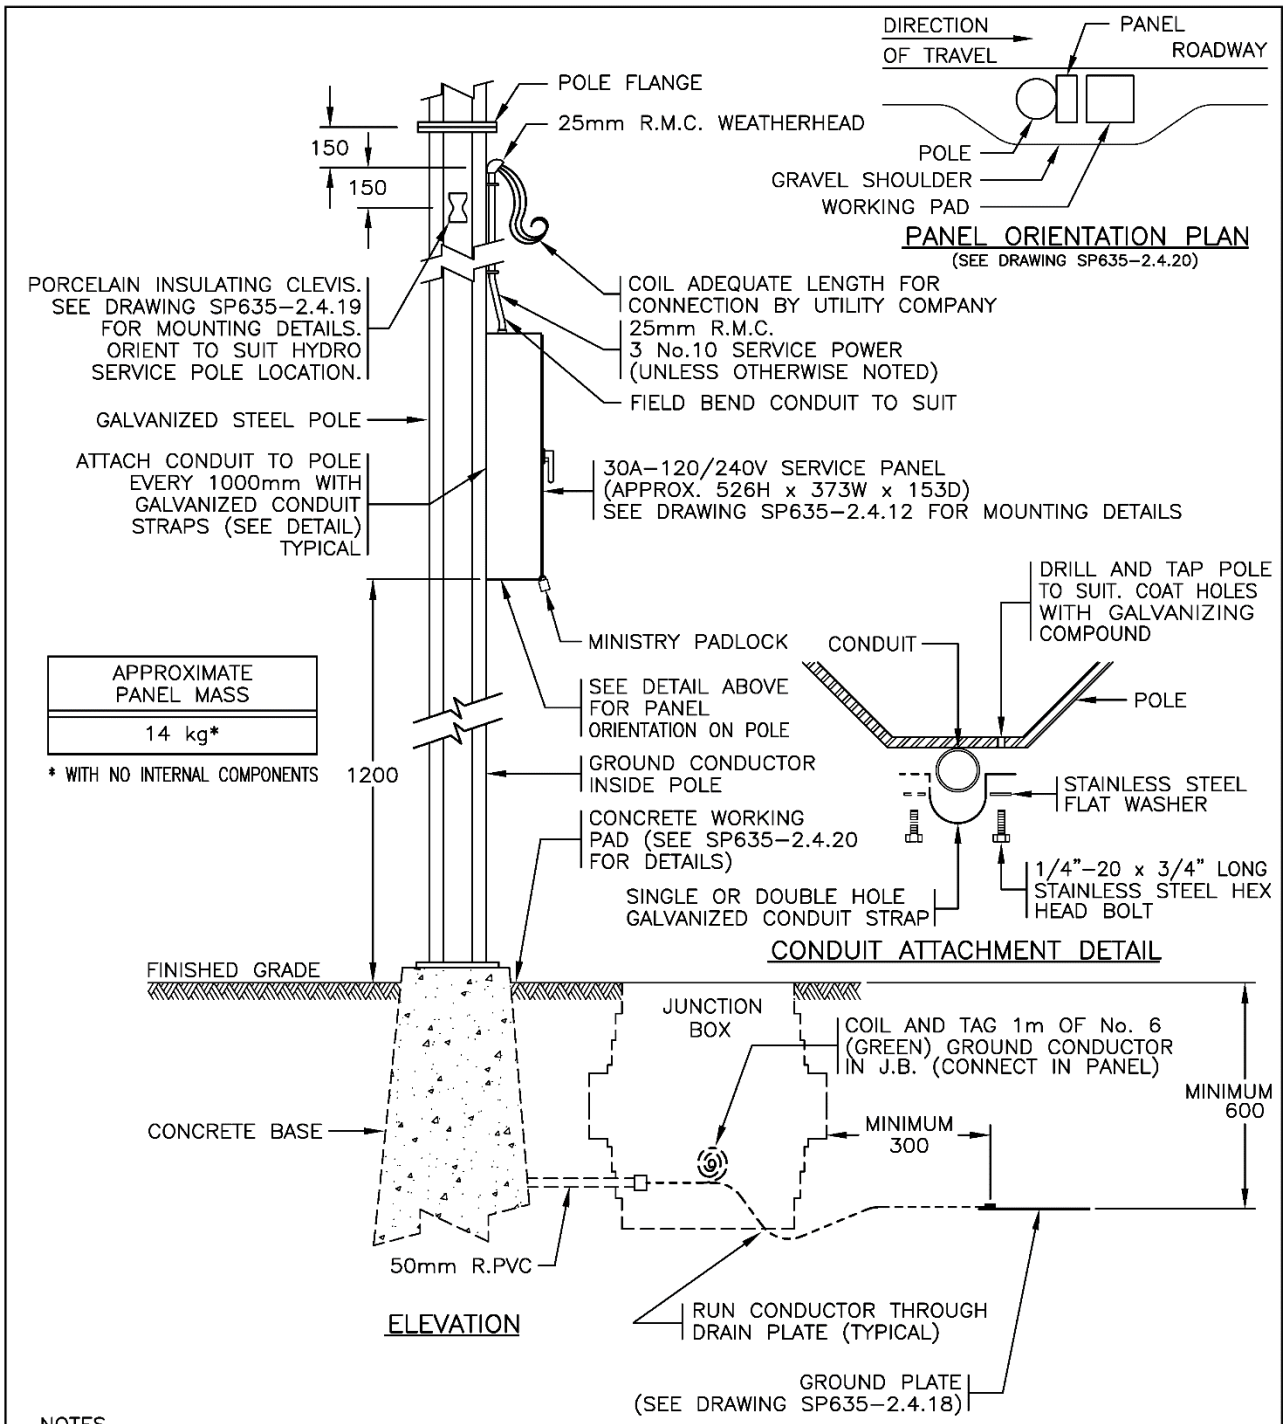


NOTES

1. SEE STANDARD SPECIFICATIONS & SPECIAL PROVISIONS FOR ADDITIONAL INFORMATION.
2. ALL DIMENSIONS ARE IN MILLIMETRES UNLESS OTHERWISE NOTED.

NOT TO SCALE


BRITISH COLUMBIA | Ministry of Transportation and Infrastructure

| No. | Revision | Date |
|---|---|---|
| E | GENERAL REVISIONS | APR 20 |
| D | GENERAL REVISIONS | APR 17 |
| C | GENERAL REVISIONS – DRAWING RENUMBERED PREVIOUSLY 2.4.7 | FEB 16 |
| B | MOUNTING HEIGHT CHANGED TO FINISHED GRADE & PANEL ORIENTATION DETAIL ADDED | NOV 98 |

# 30A – OVERHEAD SERVICE INSTALLATION DETAILS

Date: **05/02/16** Approved: **D.N.** (Signature on File)
Chief Highway Engineer

SPECIFICATION DRAWING No.
SP635-2.4.11

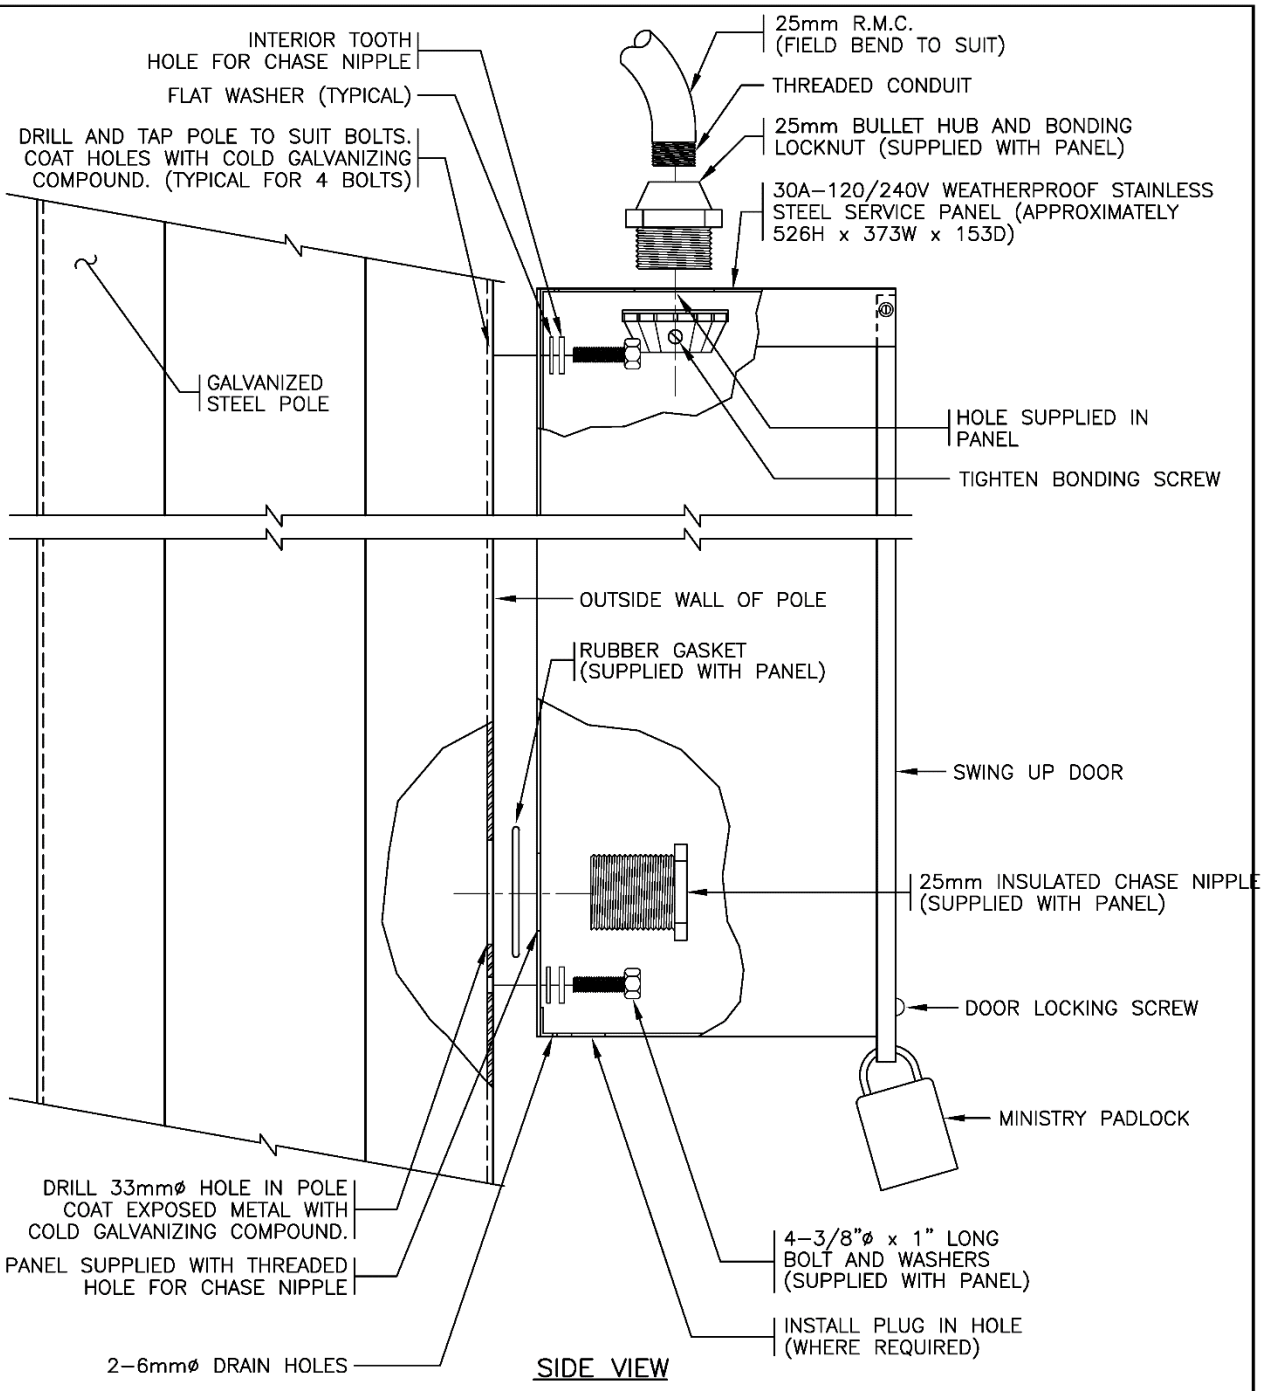


NOTES

1. SEE STANDARD SPECIFICATIONS & SPECIAL PROVISIONS FOR ADDITIONAL INFORMATION.
2. ALL DIMENSIONS ARE IN MILLIMETRES UNLESS OTHERWISE NOTED.

NOT TO SCALE

BRITISH COLUMBIA Ministry of Transportation and Infrastructure

| No. | Revision | Date |
|---|---|---|
| E | | |
| D | | |
| C | GENERAL REVISIONS – DRAWING RENUMBERED PREVIOUSLY 2.4.8 | FEB 16 |
| B | BONDING LOCKNUT ADDED | AUG 96 |
| A | GROUND CONDUIT DELETED | AUG 95 |

# 30A – OVERHEAD SERVICE PANEL INSTALLATION DETAILS


Date Approved

**05/02/16 D.N. (Signature on File)**

Chief Highway Engineer

SPECIFICATION DRAWING No.

SP635–2.4.12

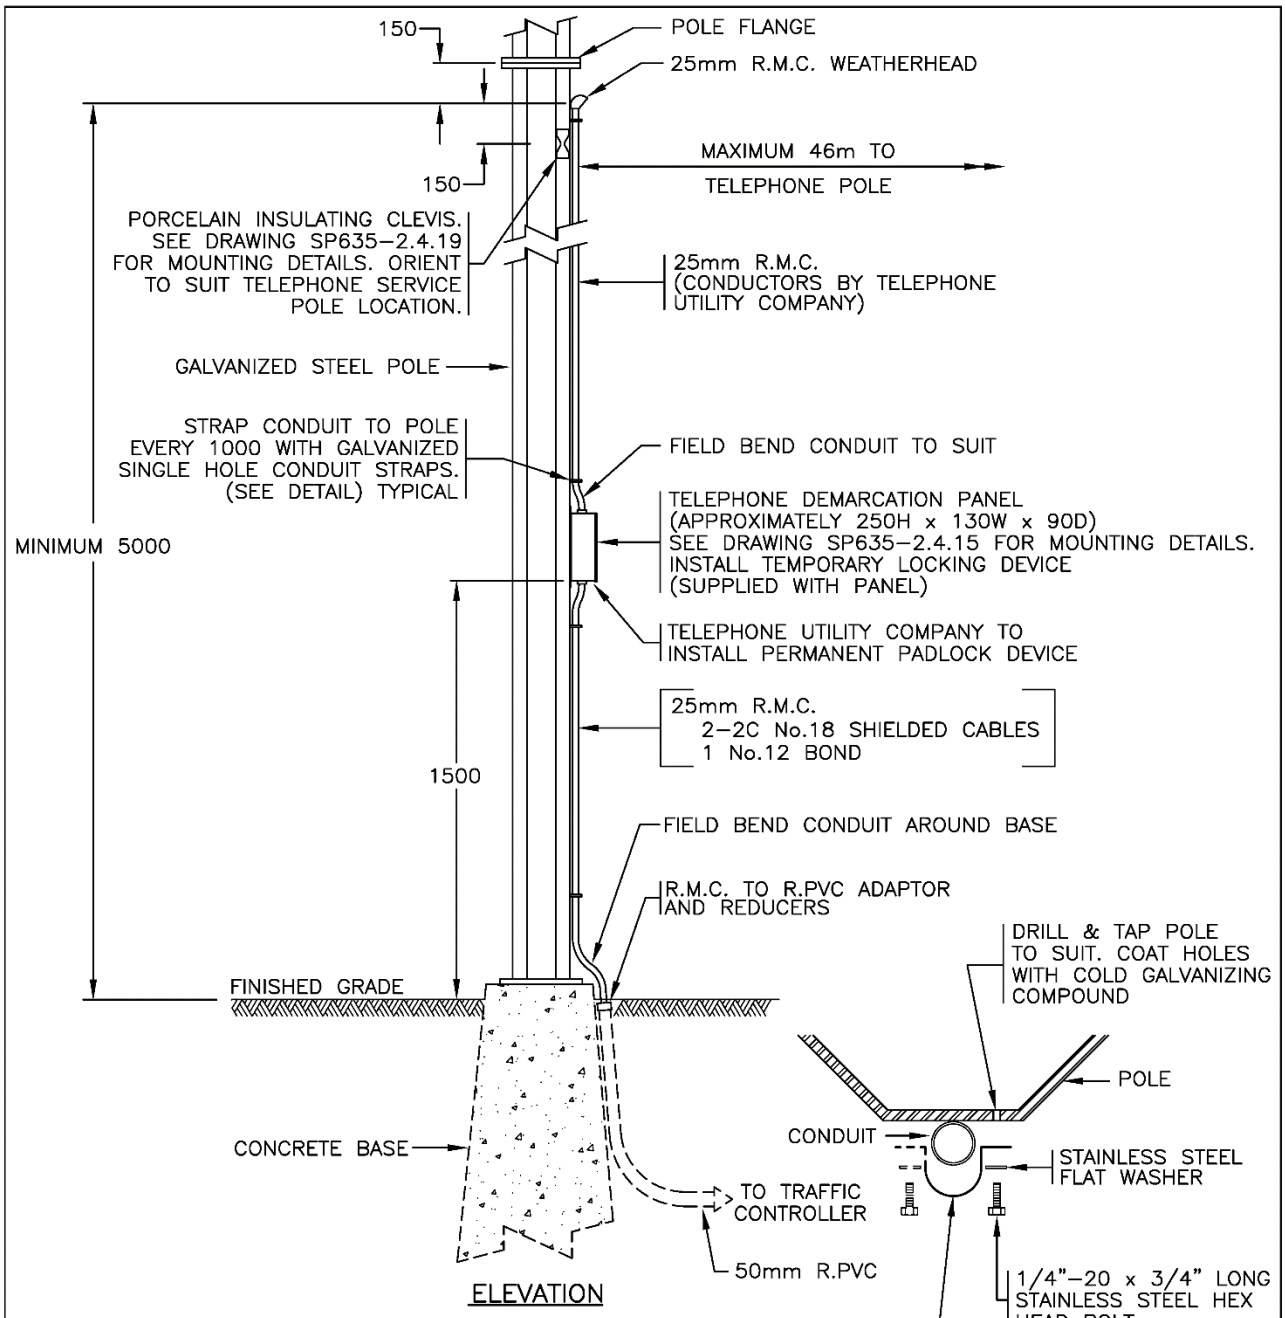


NOTES

1. SEE STANDARD SPECIFICATIONS AND SPECIAL PROVISIONS FOR ADDITIONAL INFORMATION.
2. ALL DIMENSIONS ARE IN MILLIMETRES UNLESS OTHERWISE NOTED.
3. WHERE PANEL AND CONDUITS ARE TO BE INSTALLED ON A TELEPHONE/POWER POLE THE INSTALLATION SHALL BE CARRIED OUT BY THE TELEPHONE UTILITY COMPANY.

NOT TO SCALE


BRITISH COLUMBIA — Ministry of Transportation and Infrastructure

| No. | Revision | Date |
|---|---|---|
| F | GENERAL REVISIONS | APR 20 |
| E | GENERAL REVISIONS | APR 17 |
| D | NEW DRAWING NUMBER - PREVIOUSLY NUMBERED 2.4.9 | FEB 16 |
| C | TEMPORARY LOCKING DEVICE NOTE ADDED | SEPT 00 |
| B | MOUNTING HEIGHT CHANGED TO FINISHED GRADE | NOV 98 |
| A | PANEL SIZE & STOCK NUMBER REVISED | AUG 96 |

# TELEPHONE OVERHEAD DROP SERVICE INSTALLATION DETAILS

Date: **05/02/16** Approved: **D.N.** **(Signature on File)**
Chief Highway Engineer

SPECIFICATION DRAWING No.
SP635-2.4.13

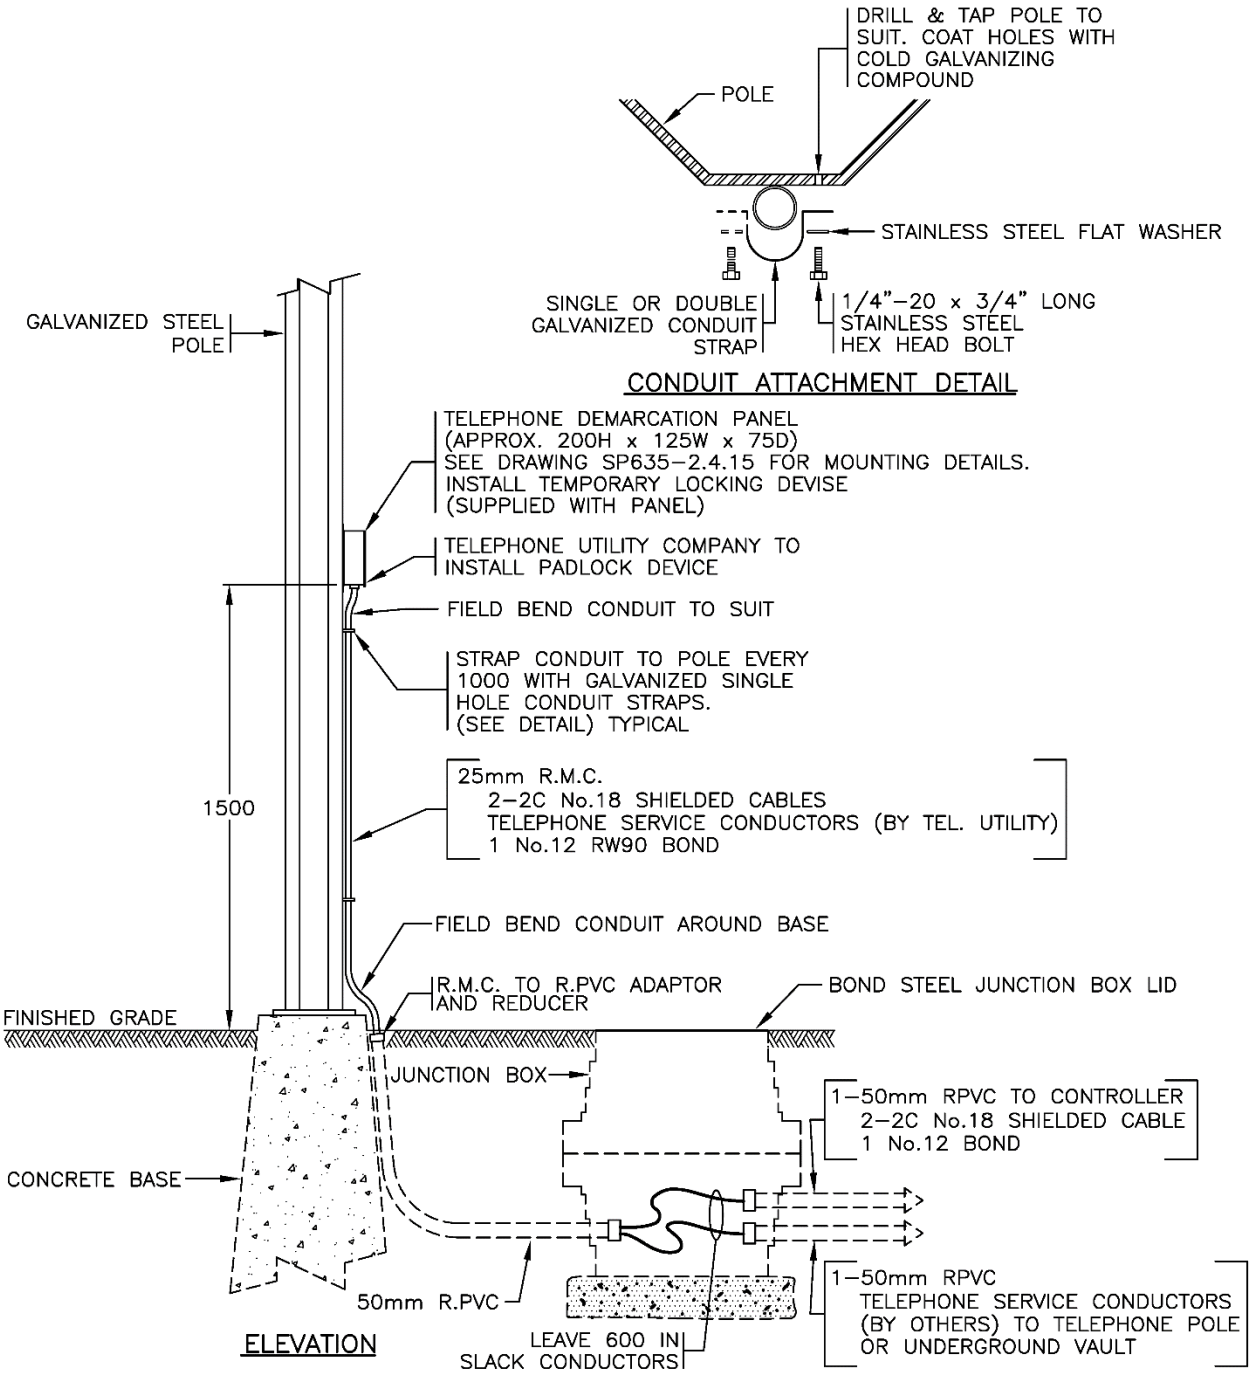


NOTES

1. SEE STANDARD SPECIFICATIONS AND SPECIAL PROVISIONS FOR ADDITIONAL INFORMATION.
2. ALL DIMENSIONS ARE IN MILLIMETRES UNLESS OTHERWISE NOTED.

NOT TO SCALE


BRITISH COLUMBIA | Ministry of Transportation and Infrastructure

| No. | Revision | Date |
|---|---|---|
| F | | |
| E | | |
| D | GENERAL REVISIONS | APR 20 |
| C | NEW DRAWING NUMBER – PREVIOUSLY NUMBERED 2.4.10 | FEB 16 |
| B | TEMPORARY LOCKING DEVICE NOTE ADDED | SEPT 00 |
| A | MOUNTING HEIGHT CHANGED TO FINISHED GRADE | NOV 98 |

# TELEPHONE UNDERGROUND SERVICE INSTALLATION DETAILS

Date: **05/02/16** Approved: **D.N.** **(Signature on File)**
Chief Highway Engineer

SPECIFICATION DRAWING No.
SP635–2.4.14

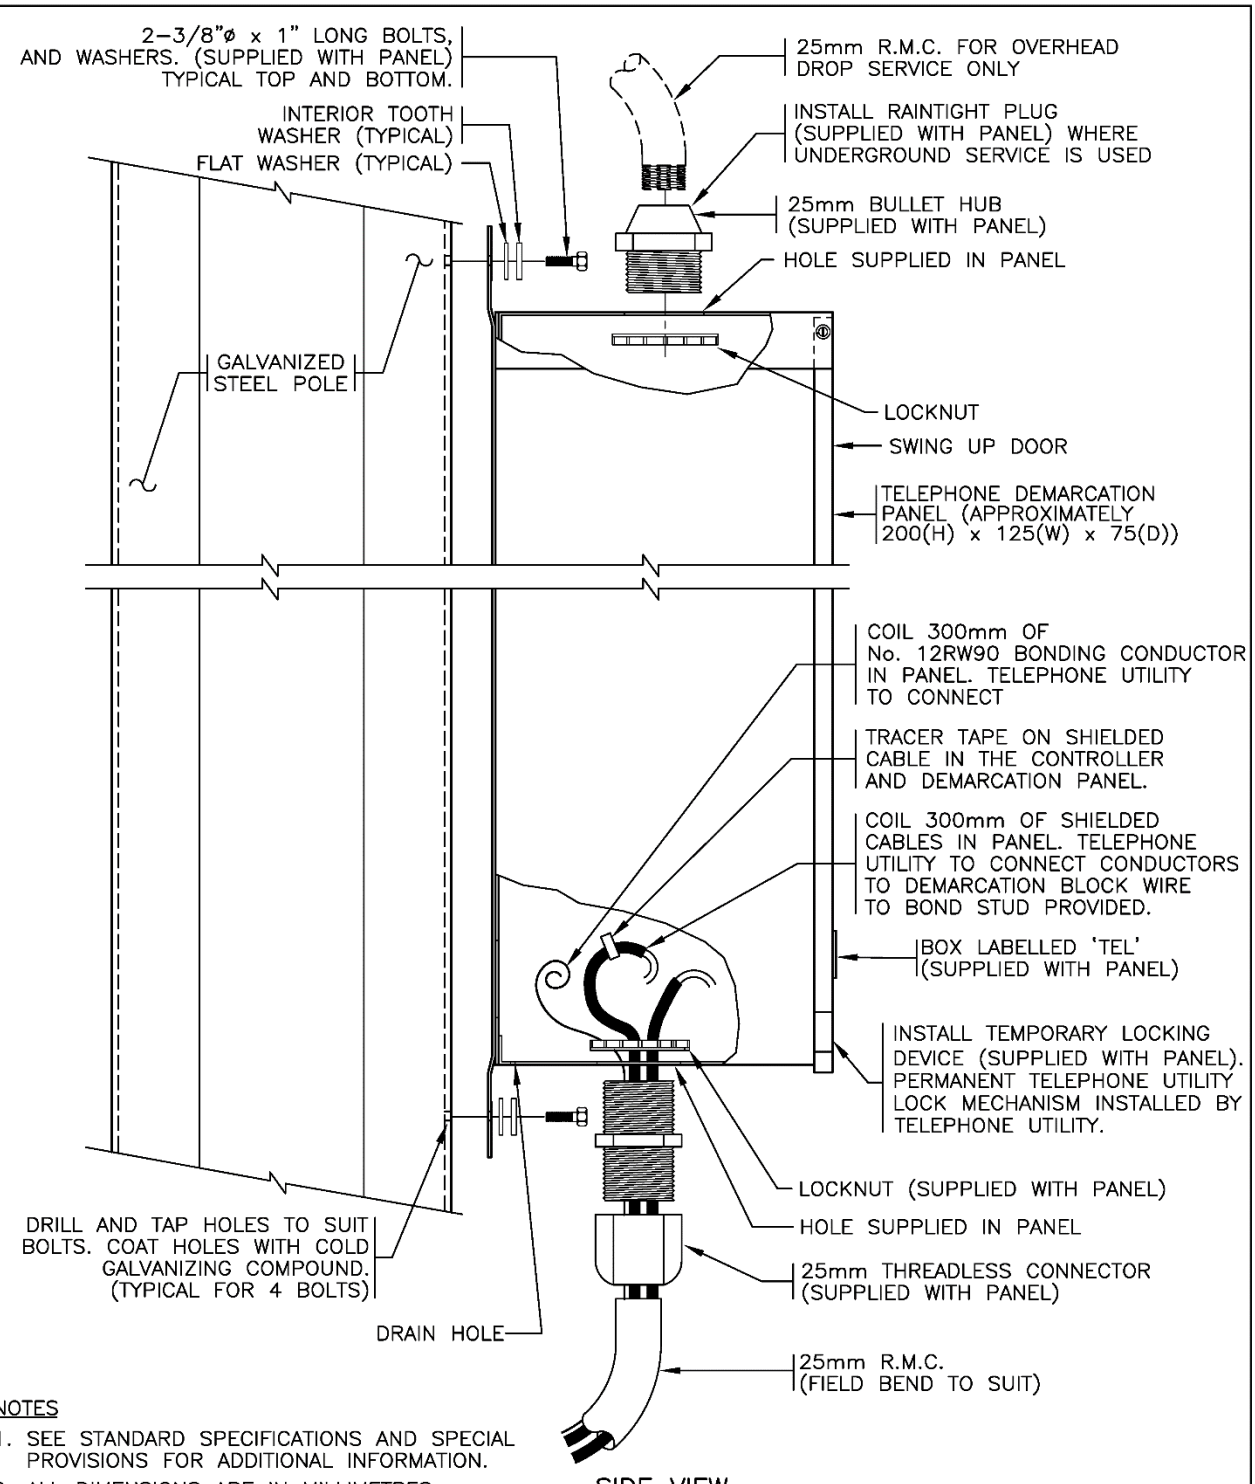


SIDE VIEW

NOTES

1. SEE STANDARD SPECIFICATIONS AND SPECIAL PROVISIONS FOR ADDITIONAL INFORMATION.
2. ALL DIMENSIONS ARE IN MILLIMETRES UNLESS OTHERWISE NOTED.

NOT TO SCALE

BRITISH COLUMBIA Ministry of Transportation and Infrastructure

| No. | Revision | Date |
|---|---|---|
| F | | |
| E | | |
| D | | |
| C | | |
| B | NEW DRAWING NUMBER – PREVIOUSLY NUMBERED 2.4.11 | FEB 16 |
| A | TEMPORARY LOCKING DEVICE NOTE ADDED | SEPT 00 |

# TELEPHONE DEMARCATION PANEL INSTALLATION DETAILS


Date Approved

**05/02/16 D.N. (Signature on File)**


Chief Highway Engineer

SPECIFICATION DRAWING No.

SP635–2.4.15

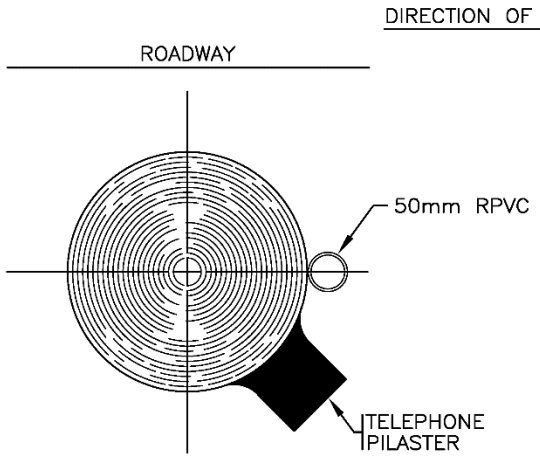



CONDUIT ON TELEPHONE POLE

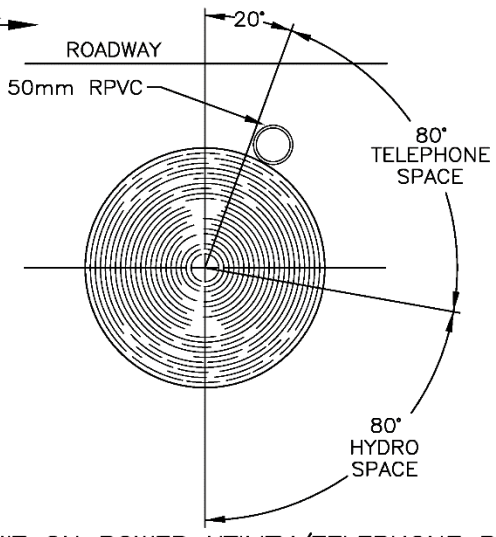



CONDUIT ON POWER UTILITY/TELEPHONE POLE


## PLAN VIEWS

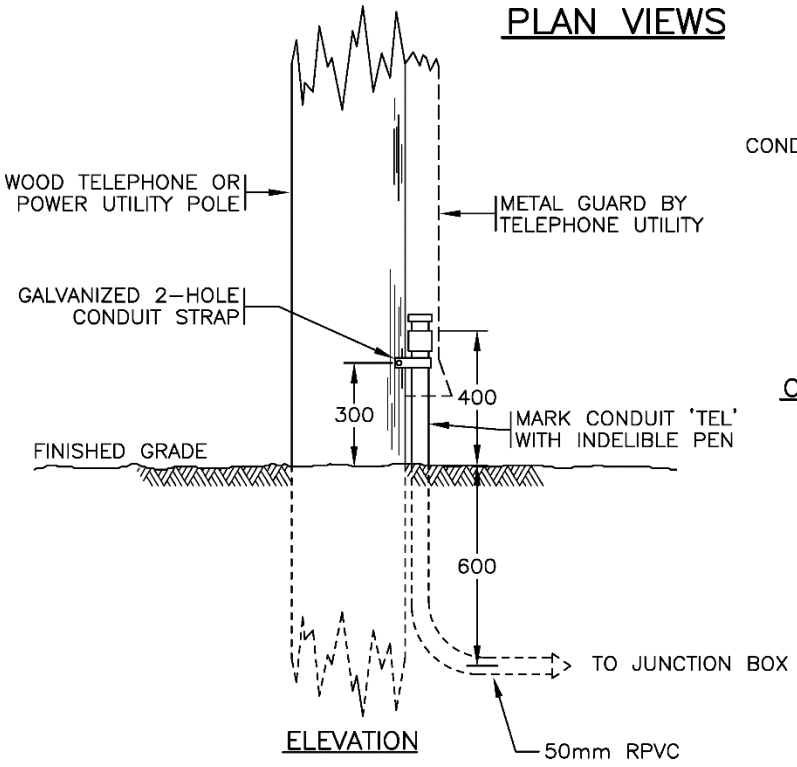


ELEVATION

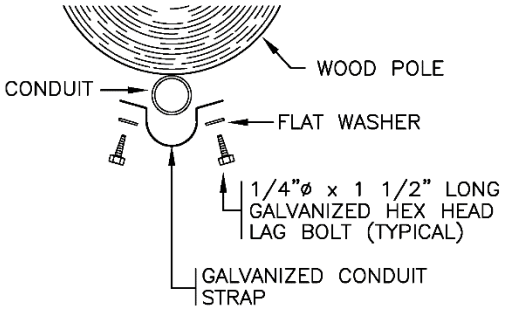


CONDUIT ATTACHMENT DETAIL

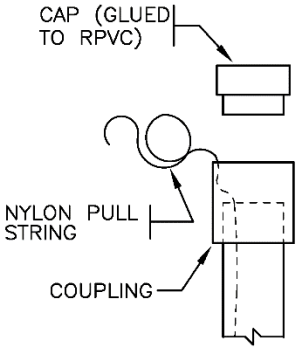


CAP DETAIL

NOTES

1. SEE STANDARD SPECIFICATIONS AND SPECIAL PROVISIONS FOR ADDITIONAL INFORMATION.
2. ALL DIMENSIONS ARE IN MILLIMETRES UNLESS OTHERWISE NOTED.

NOT TO SCALE

BRITISH COLUMBIA Ministry of Transportation and Infrastructure

| No. | Revision | Date |
|---|---|---|
| F | | |
| E | | |
| D | | |
| C | | |
| B | GENERAL REVISIONS | APR 17 |
| A | NEW DRAWING NUMBER – PREVIOUSLY NUMBERED 2.4.12 | FEB 16 |

# TELEPHONE CONDUIT INSTALLATION DETAILS (WOOD POLE)


Date Approved

**05/02/16 D.N. (Signature on File)**


Chief Highway Engineer

SPECIFICATION DRAWING No.

SP635–2.4.16

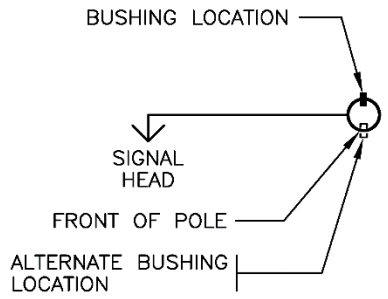


BUSHING ORIENTATION

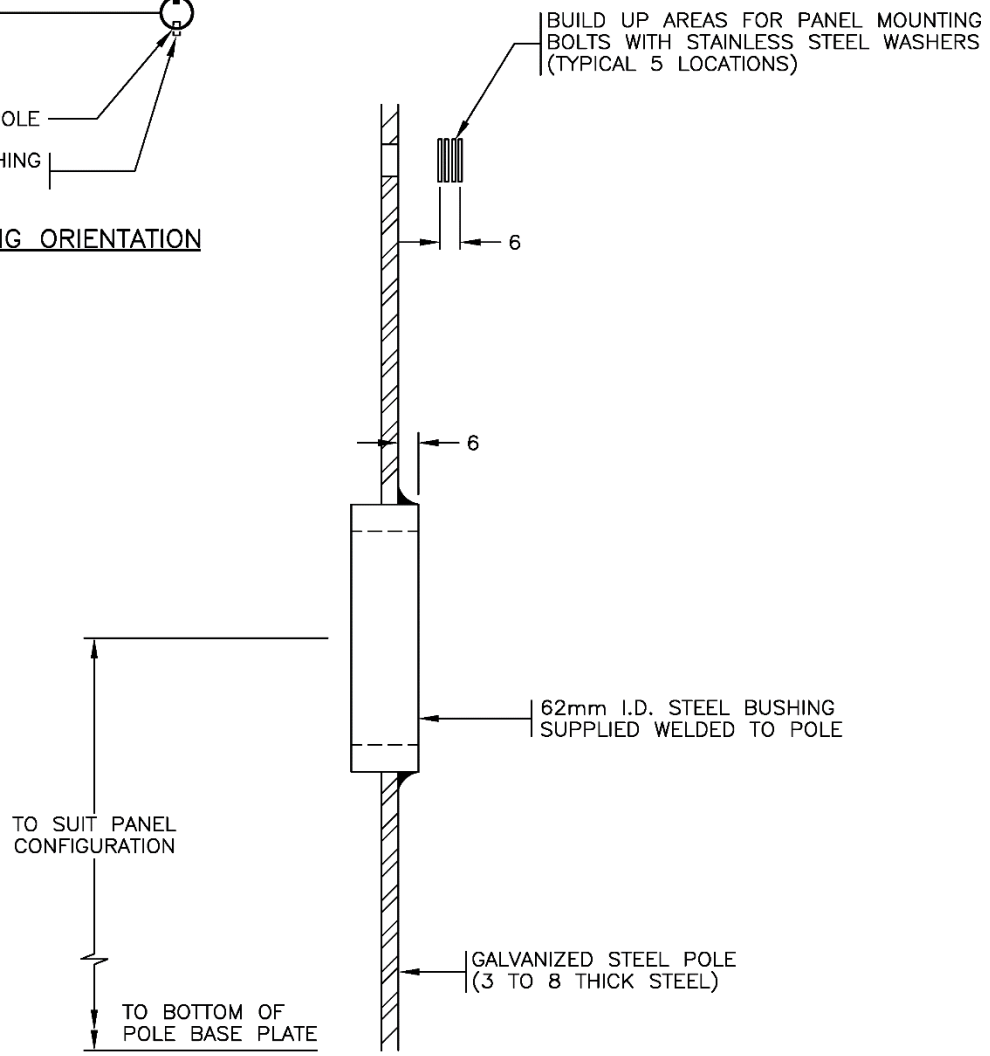


POLE SHALL BE SUPPLIED WITH BUSHING INSTALLED, UNLESS OTHERWISE NOTED

NOTES

1. SEE STANDARD SPECIFICATIONS AND SPECIAL PROVISIONS FOR ADDITIONAL INFORMATION.
2. ALL DIMENSIONS ARE IN MILLIMETRES.

NOT TO SCALE

BRITISH COLUMBIA | Ministry of Transportation and Infrastructure

| No. | Revision | Date |
|---|---|---|
| F | | |
| E | NEW DRAWING NUMBER – PREVIOUSLY NUMBERED 2.4.13 | FEB 16 |
| D | REGION 4 CHANGED TO 3 | OCT 03 |
| C | BUSHING LOCATION REVISED | AUG 99 |
| B | BUSHING LOCATION REVISED | AUG 96 |
| A | BUSHING ORIENTATION & MOUNTING HEIGHTS ADDED | AUG 95 |

SERVICE PANEL BUSHING DETAIL


Date Approved

05/02/16 D.N. (Signature on File)

Chief Highway Engineer

SPECIFICATION DRAWING No.

SP635–2.4.17

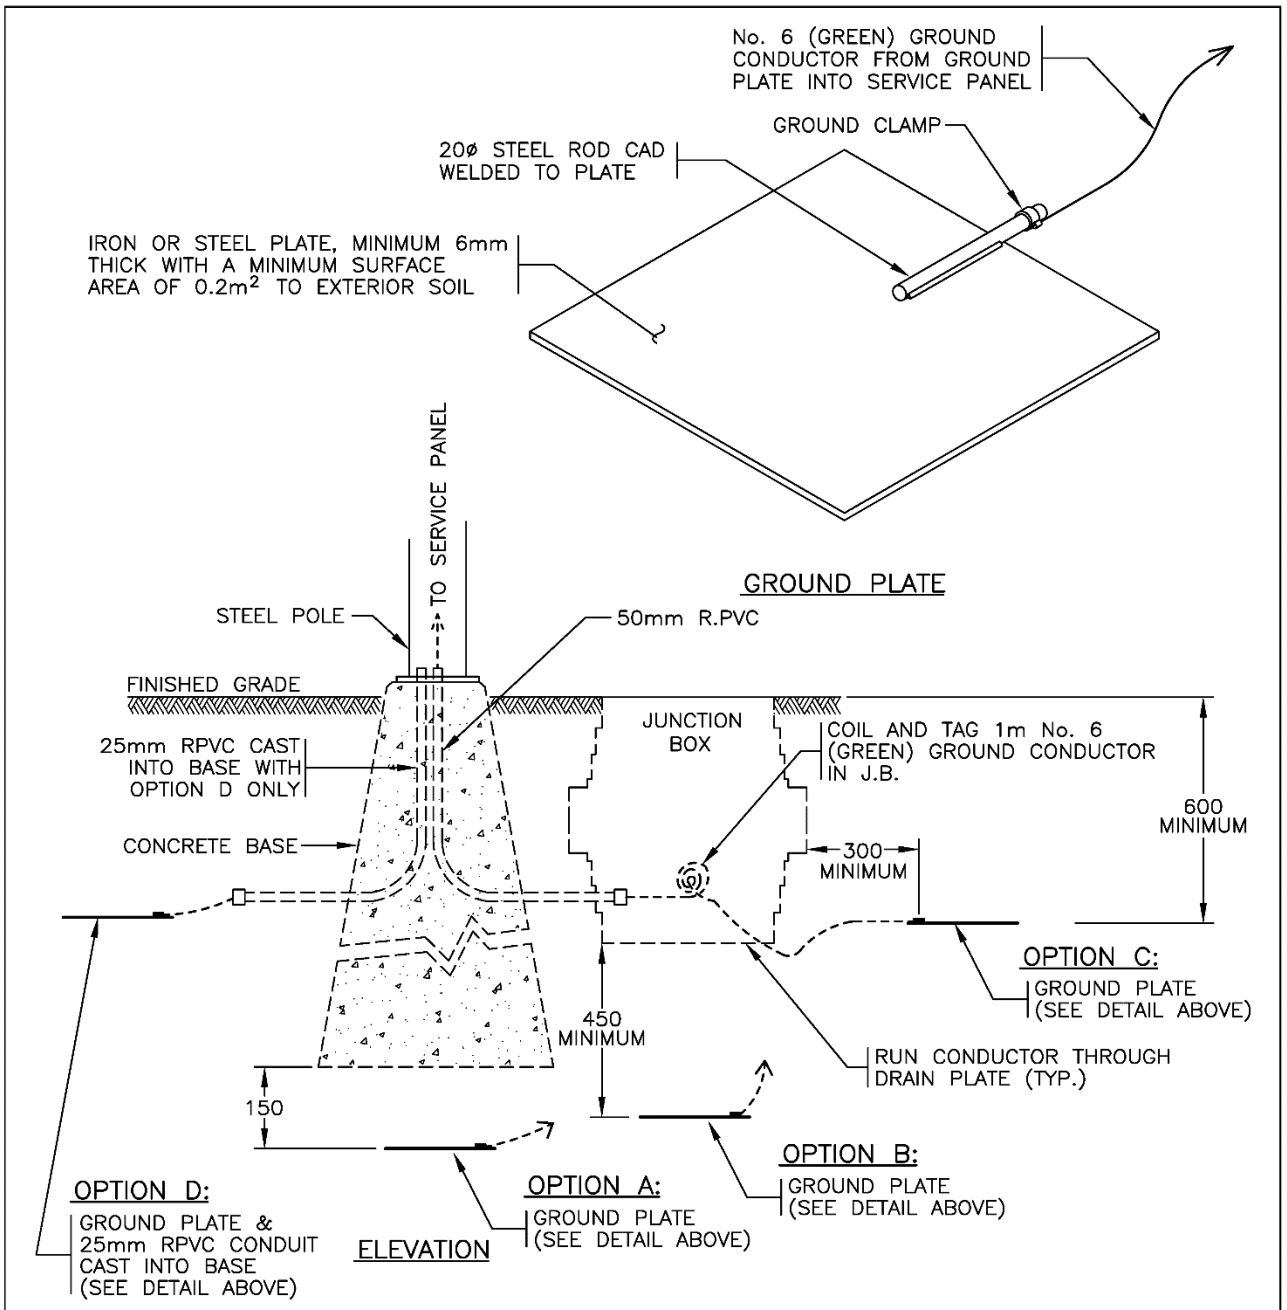


NOTES

1. SEE STANDARD SPECIFICATIONS & SPECIAL PROVISIONS FOR ADDITIONAL INFORMATION.
2. ALL DIMENSIONS ARE IN MILLIMETRES UNLESS OTHERWISE NOTED.
3. WHERE PLATE CAN NOT BE INSTALLED UNDER THE BASE IT SHALL BE INSTALLED AT A MINIMUM DEPTH OF 600mm BELOW FINISHED GRADE, BESIDE THE BASE

NOT TO SCALE


BRITISH COLUMBIA | Ministry of Transportation and Infrastructure

| No. | Revision | Date |
|---|---|---|
| F | | |
| E | GENERAL REVISION | APR 20 |
| D | NEW DRAWING NUMBER – PREVIOUSLY NUMBERED 2.4.14 | FEB 16 |
| C | GROUND PLATE REVISED | OCT 03 |
| B | OPTION D ADDED | AUG 96 |
| A | GENERAL REVISION | OCT 95 |

## GROUND PLATE INSTALLATION DETAIL

Date: **05/02/16** Approved: **D.N.** **(Signature on File)**
Chief Highway Engineer

SPECIFICATION DRAWING No.
SP635–2.4.18

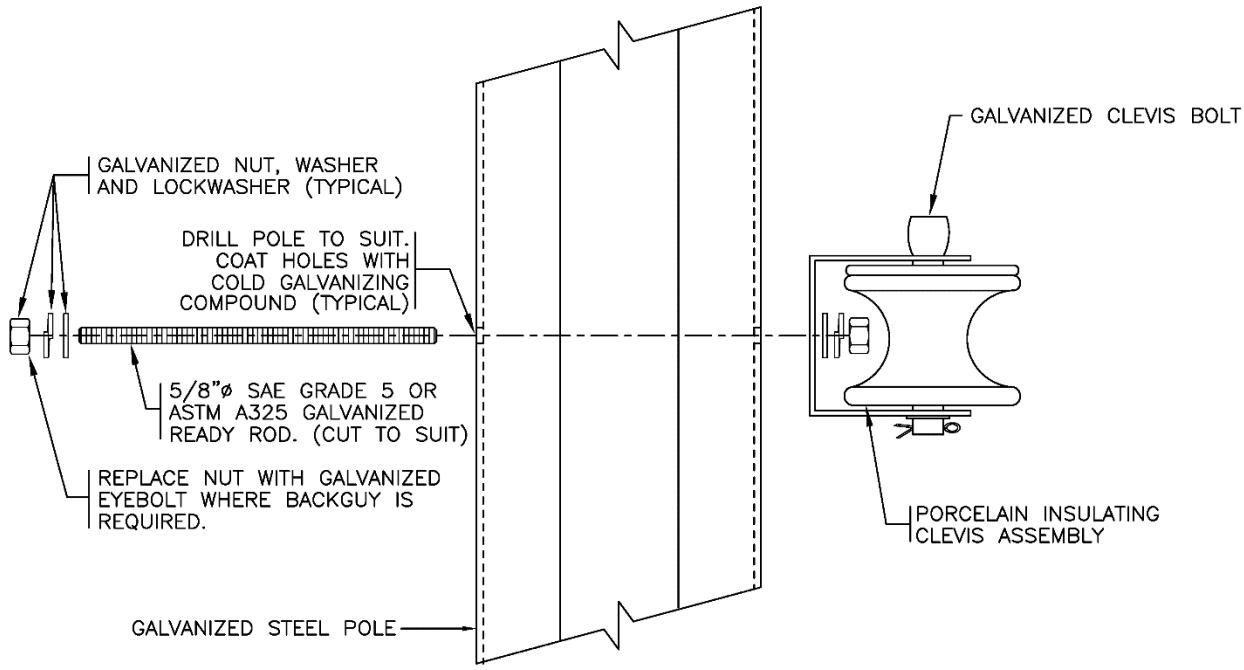


ELEVATION

NOTES

1. SEE STANDARD SPECIFICATIONS & SPECIAL PROVISIONS FOR ADDITIONAL INFORMATION.

NOT TO SCALE

BRITISH COLUMBIA | Ministry of Transportation and Infrastructure

| No. | Revision | Date |
|---|---|---|
| F | | |
| E | | |
| D | | |
| C | | |
| B | NEW DRAWING NUMBER – PREVIOUSLY NUMBERED 2.4.15 | FEB 16 |
| A | GENERAL REVISIONS | AUG 94 |

# INSULATING CLEVIS INSTALLATION DETAILS


Date Approved

**05/02/16 D.N. (Signature on File)**

Chief Highway Engineer

SPECIFICATION DRAWING No.

SP635–2.4.19

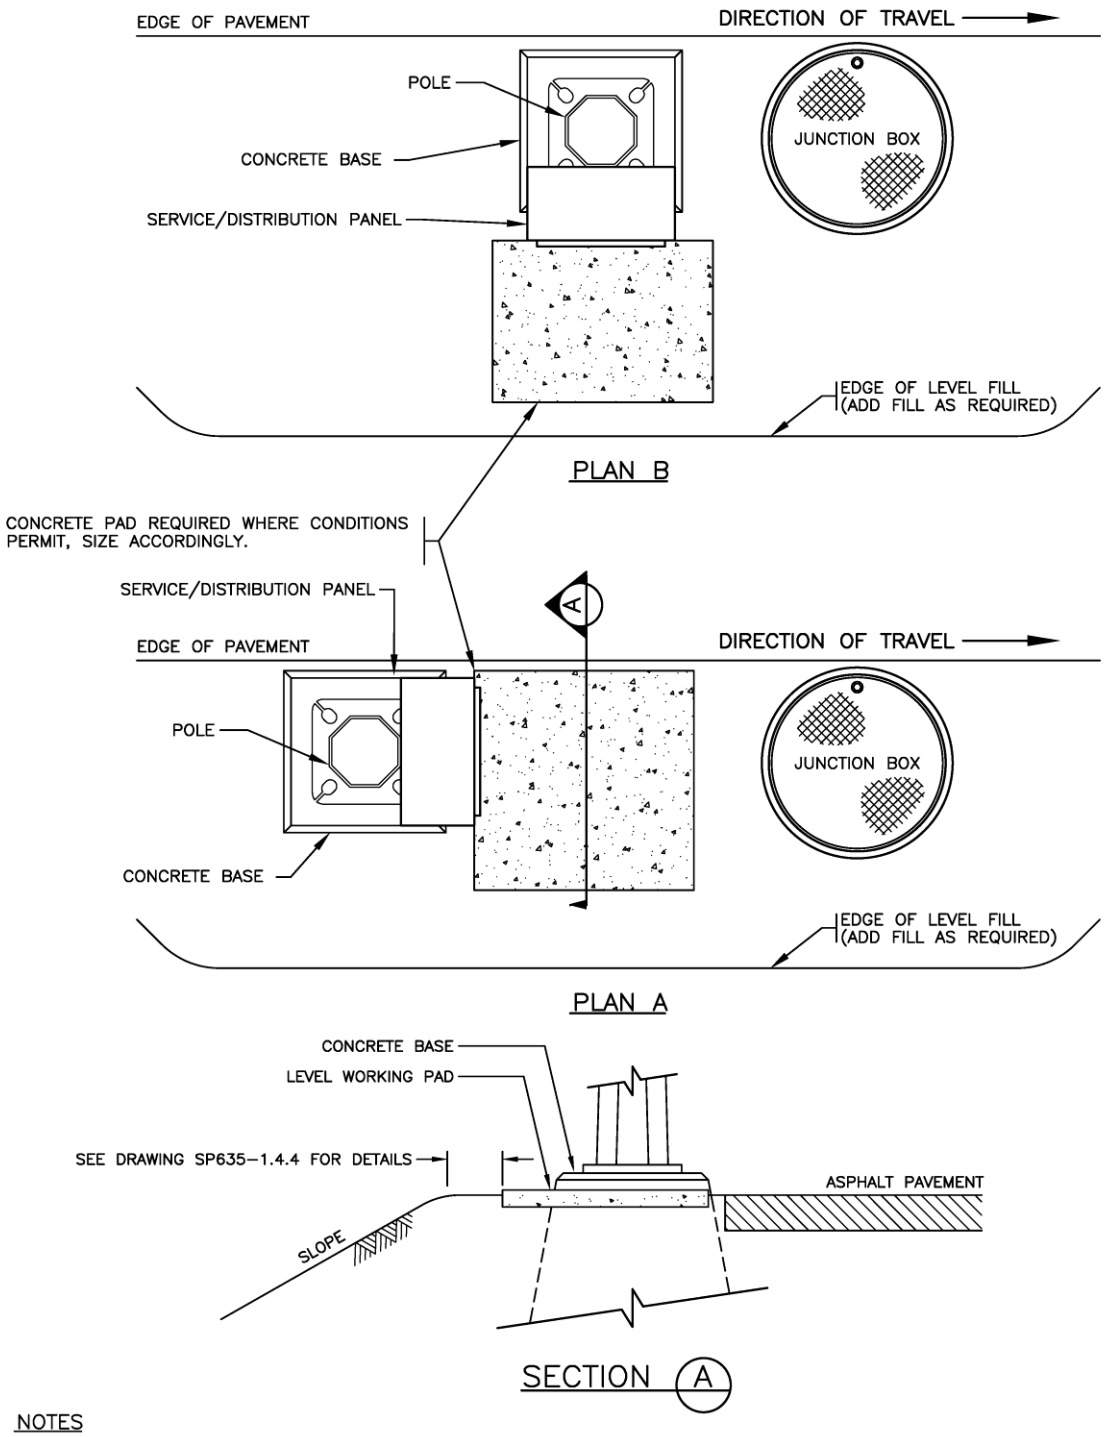


NOTES

1. SEE STANDARD SPECIFICATIONS & SPECIAL PROVISIONS FOR ADDITIONAL INFORMATION.
2. ALL DIMENSIONS ARE IN MILLIMETRES UNLESS OTHERWISE NOTED.

NOT TO SCALE


BRITISH COLUMBIA | Ministry of Transportation and Infrastructure

| No. | Revision | Date |
|---|---|---|
| F | GENERAL REVISION | APR 20 |
| E | JUNCTION BOX MOVED TO DOWNSTREAM SIDE | APR 16 |
| D | NEW DRAWING NUMBER - PREVIOUSLY NUMBERED 2.4.16 | FEB 16 |
| C | JUNCTION BOX LOCATION REVISED | FEB 12 |
| B | PLAN B ADDED | MAR 11 |
| A | ORIENTATION REVISED | SEPT 00 |

# SERVICE PANEL WORKING PAD DETAIL

Date: **05/02/16** Approved: **D.N. (Signature on File)**
Chief Highway Engineer

SPECIFICATION DRAWING No.
SP635-2.4.20

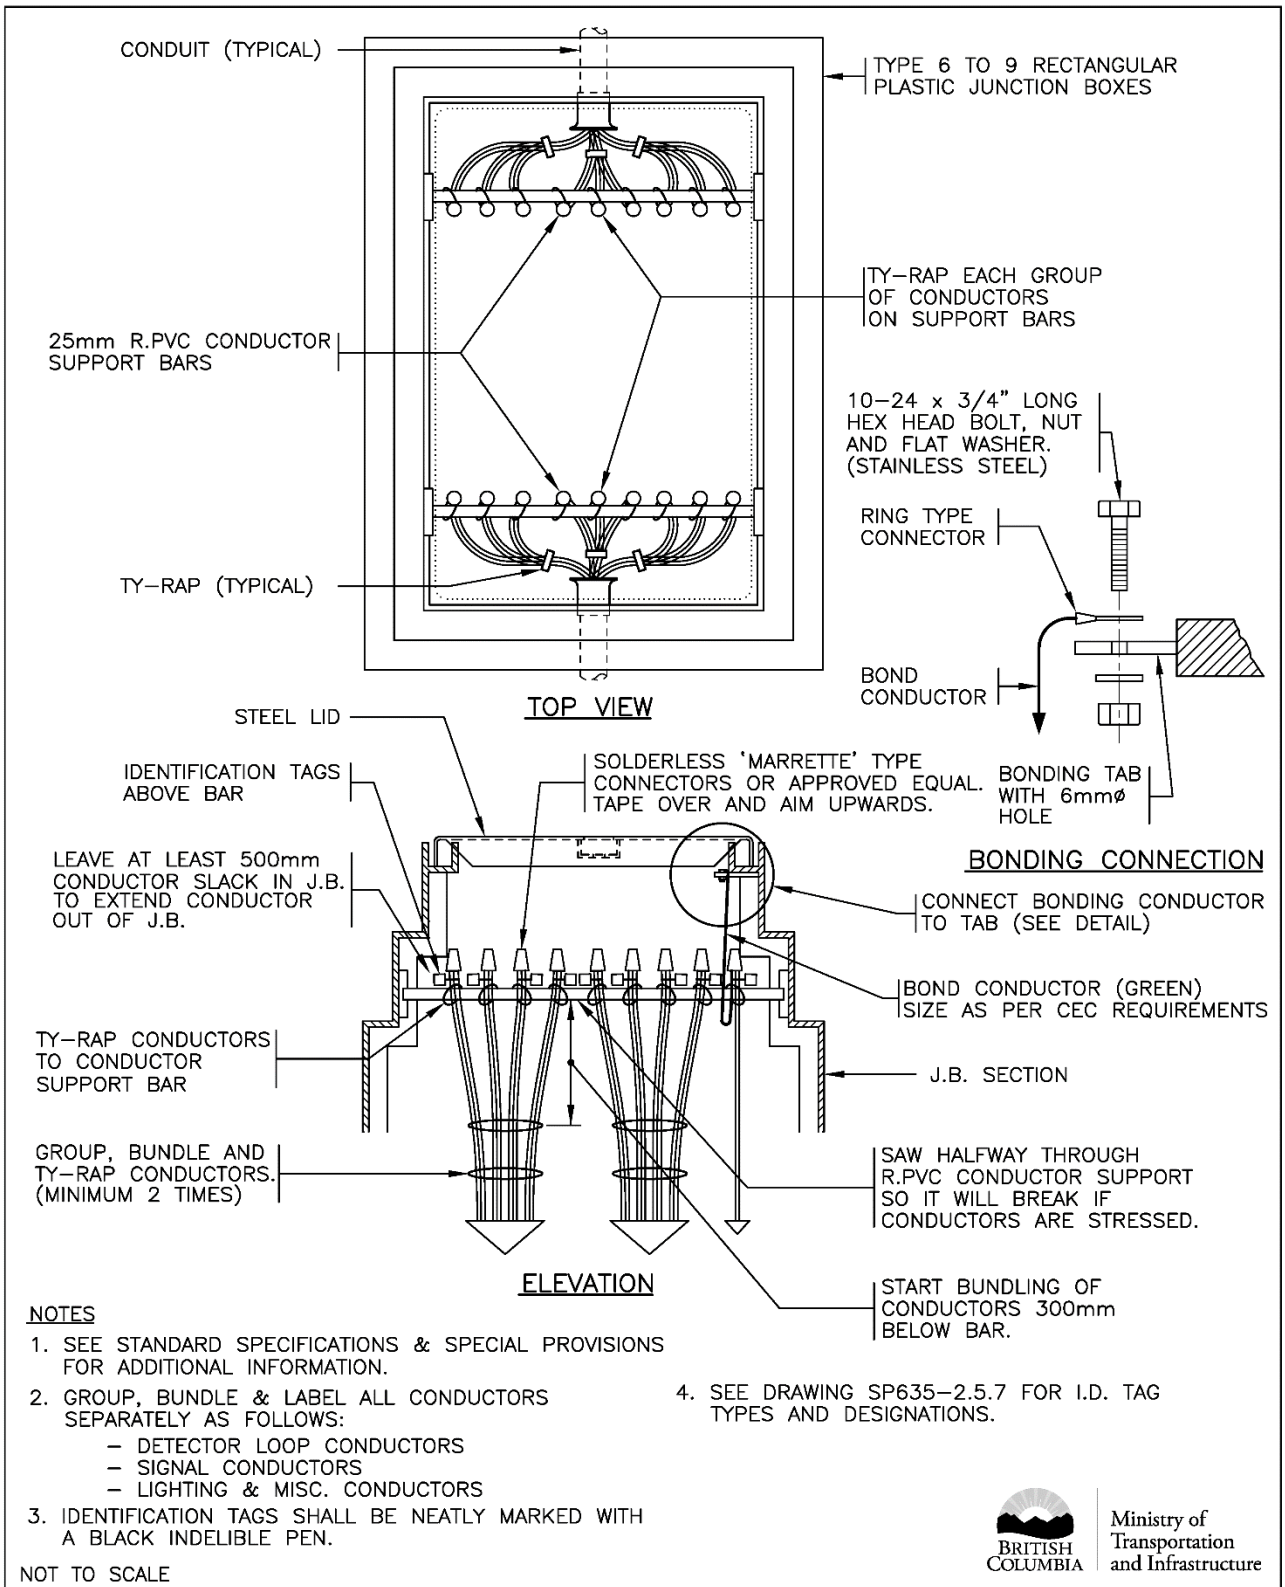


NOTES

1. SEE STANDARD SPECIFICATIONS & SPECIAL PROVISIONS FOR ADDITIONAL INFORMATION.
2. GROUP, BUNDLE & LABEL ALL CONDUCTORS SEPARATELY AS FOLLOWS:
   - DETECTOR LOOP CONDUCTORS
   - SIGNAL CONDUCTORS
   - LIGHTING & MISC. CONDUCTORS
3. IDENTIFICATION TAGS SHALL BE NEATLY MARKED WITH A BLACK INDELIBLE PEN.
4. SEE DRAWING SP635–2.5.7 FOR I.D. TAG TYPES AND DESIGNATIONS.

NOT TO SCALE

BRITISH COLUMBIA — Ministry of Transportation and Infrastructure

| No. | Revision | Date |
|---|---|---|
| F | | |
| E | | |
| D | GENERAL REVISION | APR 20 |
| C | No. 12 BOND REFERENCE REMOVED | JAN 19 |
| B | GENERAL REVISIONS | APR 17 |
| A | GENERAL REVISIONS | AUG 94 |

# WIRING INSIDE TYPES 6 TO 9 RECTANGULAR PLASTIC JUNCTION BOXES


Date Approved

**30/09/93 E.L. (Signature on File)**

Chief Highway Engineer

SPECIFICATION DRAWING No.

SP635–2.5.1

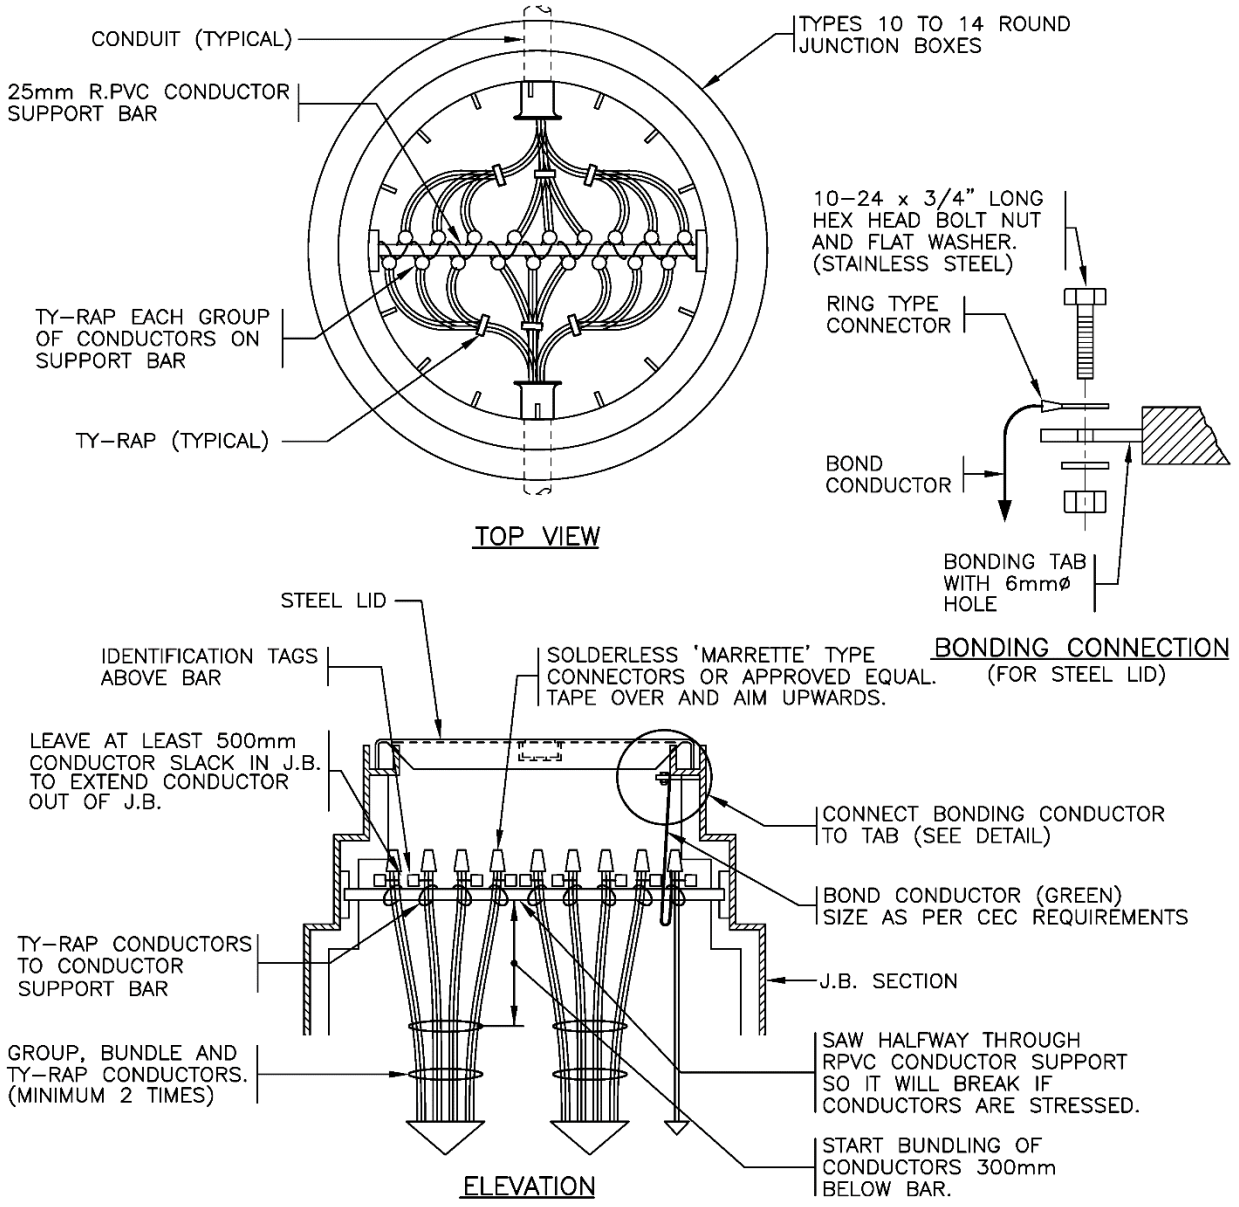


NOTES

1. SEE STANDARD SPECIFICATIONS & SPECIAL PROVISIONS FOR ADDITIONAL INFORMATION.
2. GROUP, BUNDLE AND LABEL ALL CONDUCTORS SEPARATELY AS FOLLOWS:
   - DETECTOR LOOP CONDUCTORS
   - SIGNAL CONDUCTORS
   - LIGHTING & MISC. CONDUCTORS
3. IDENTIFICATION TAGS SHALL BE NEATLY MARKED WITH A BLACK INDELIBLE PEN.
4. SEE DRAWING SP635–2.5.7 FOR I.D. TAG TYPES AND DESIGNATIONS.

NOT TO SCALE

BRITISH COLUMBIA Ministry of Transportation and Infrastructure

| No. | Revision | Date |
|---|---|---|
| F | | |
| E | | |
| D | | |
| C | GENERAL REVISIONS | APR 20 |
| B | GENERAL REVISIONS | APR 17 |
| A | GENERAL REVISIONS | AUG 94 |

# WIRING INSIDE TYPES 10 TO 14 ROUND PLASTIC JUNCTION BOXES


Date Approved


**30/09/93 E.L. (Signature on File)**

Chief Highway Engineer

SPECIFICATION DRAWING No.

SP635–2.5.2

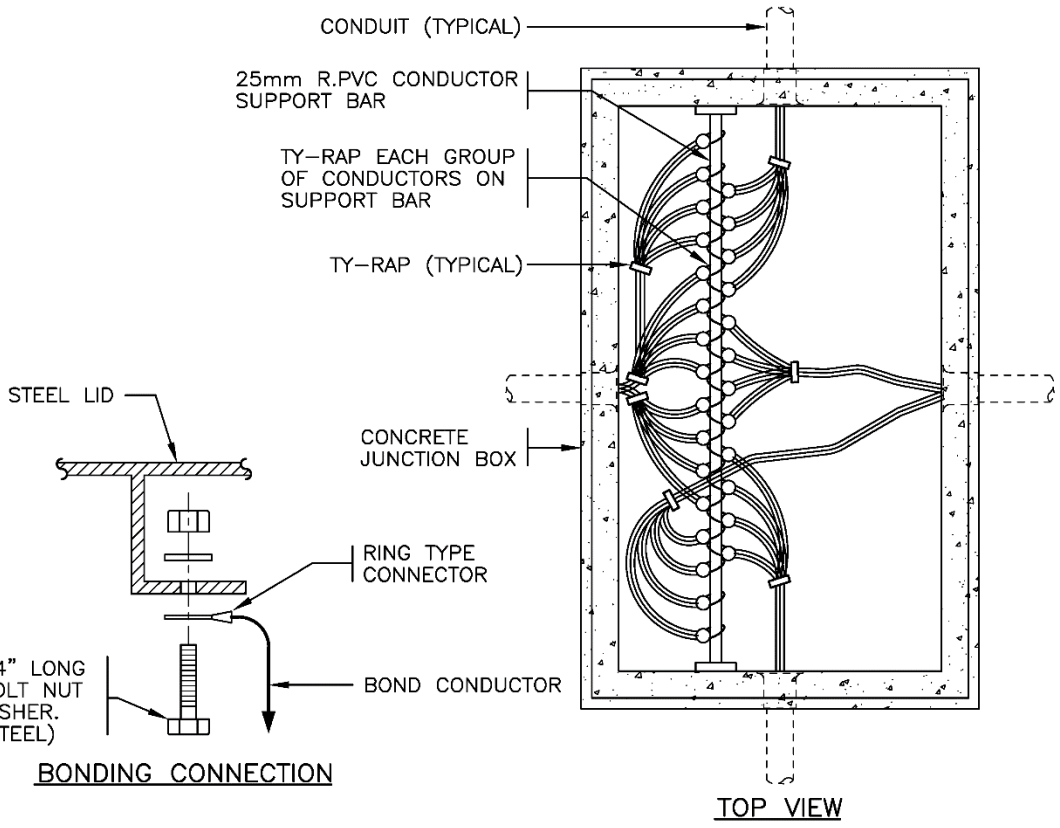

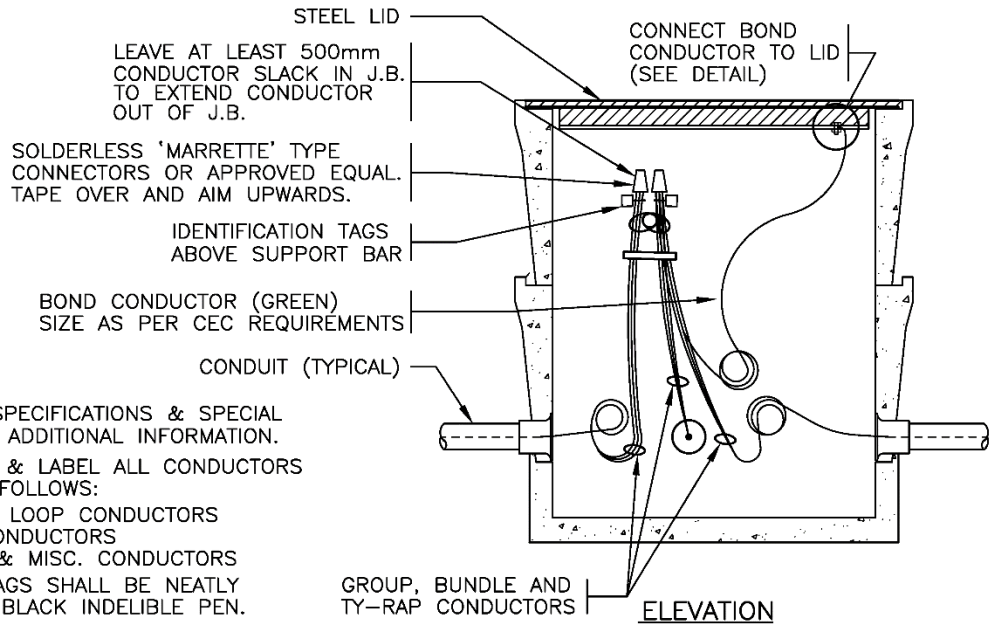
NOTES

1. SEE STANDARD SPECIFICATIONS & SPECIAL PROVISIONS FOR ADDITIONAL INFORMATION.
2. GROUP, BUNDLE & LABEL ALL CONDUCTORS SEPARATELY AS FOLLOWS:
   - DETECTOR LOOP CONDUCTORS
   - SIGNAL CONDUCTORS
   - LIGHTING & MISC. CONDUCTORS
3. IDENTIFICATION TAGS SHALL BE NEATLY MARKED WITH A BLACK INDELIBLE PEN.
4. SEE DRAWING SP635–2.5.7 FOR I.D. TAG TYPES AND DESIGNATIONS.

BRITISH COLUMBIA | Ministry of Transportation and Infrastructure

NOT TO SCALE

| No. | Revision | Date |
|---|---|---|
| F | | |
| E | | |
| D | | |
| C | | |
| B | GENERAL REVISIONS | APR 20 |
| A | GENERAL REVISIONS | APR 17 |

# WIRING INSIDE CONCRETE JUNCTION BOX


Date Approved

**21/11/94 E.L. (Signature on File)**


Chief Highway Engineer

SPECIFICATION DRAWING No.

SP635–2.5.3

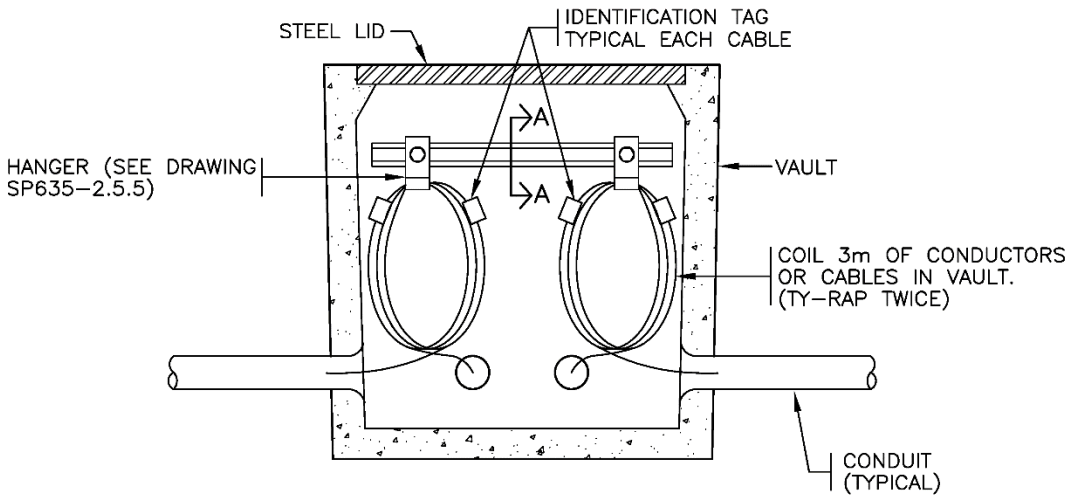


DETAIL OF CONDUCTORS OR CABLES THROUGH VAULTS
(TYPICAL 2 SIDES OF VAULT)

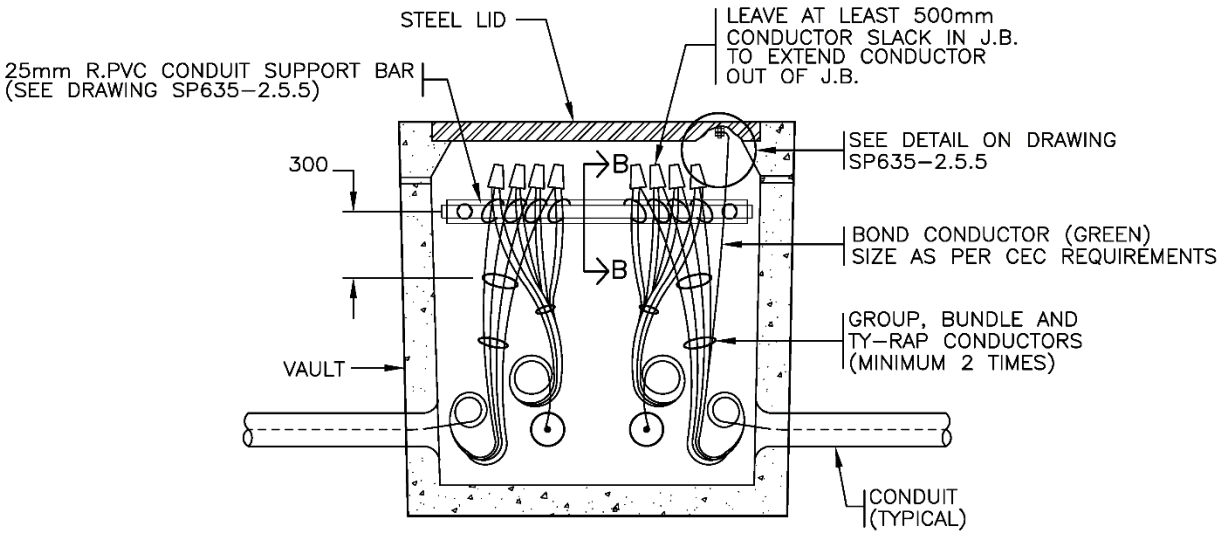


DETAIL OF CONDUCTOR SPLICES IN VAULTS
(TYPICAL 2 SIDES OF VAULT)

NOTES

1. SEE STANDARD SPECIFICATIONS & SPECIAL PROVISIONS FOR ADDITIONAL INFORMATION.
2. SEE DRAWING SP635–2.5.5 FOR ADDITIONAL NOTES AND DETAILS.
3. GROUP & BUNDLE ALL CONDUCTORS SEPARATELY AS FOLLOWS:
   - DETECTOR LOOP CONDUCTORS
   - SIGNAL CONDUCTORS
   - LIGHTING & MISC. CONDUCTORS
4. IDENTIFICATION TAGS SHALL BE NEATLY MARKED WITH A BLACK INDELIBLE PEN.
5. ALL DIMENSIONS ARE IN MILLIMETRES UNLESS OTHERWISE NOTED.
6. SEE DRAWING SP635–2.5.7 FOR I.D. TAG TYPES AND DESIGNATIONS.

BRITISH COLUMBIA Ministry of Transportation and Infrastructure

NOT TO SCALE

| No. | Revision | Date |
|---|---|---|
| F | | |
| E | | |
| D | | |
| C | GENERAL REVISIONS | APR 20 |
| B | GENERAL REVISIONS | APR 17 |
| A | GENERAL REVISIONS | AUG 94 |

WIRING INSIDE CONCRETE VAULTS

Date Approved
**30/09/93 E.L. (Signature on File)**
Chief Highway Engineer

SPECIFICATION DRAWING No.
SP635–2.5.4