
TYPE LB SIGN ARM AND BRACKETS NOT SHOWN (SEE DRAWINGS SP635–3.3.1 AND 3.3.2)

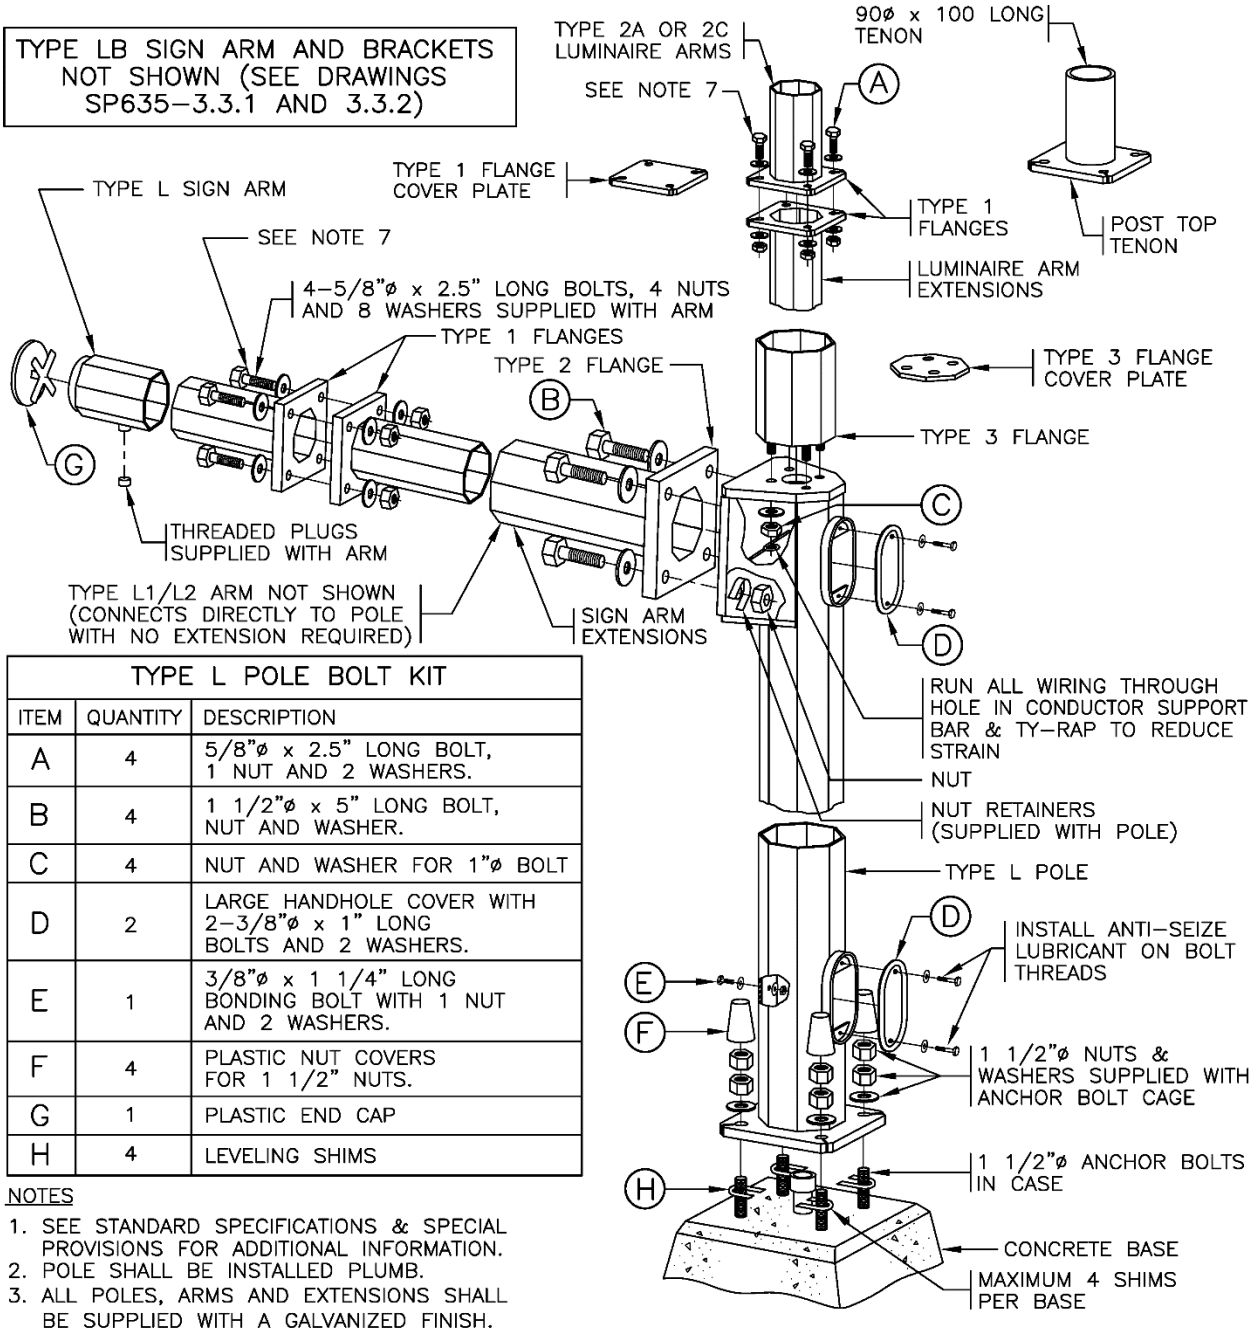

POLE ASSEMBLY DETAIL

TYPE L POLE BOLT KIT		
ITEM	QUANTITY	DESCRIPTION
A	4	5/8"ø x 2.5" LONG BOLT, 1 NUT AND 2 WASHERS.
B	4	1 1/2"ø x 5" LONG BOLT, NUT AND WASHER.
C	4	NUT AND WASHER FOR 1"ø BOLT
D	2	LARGE HANDHOLE COVER WITH 2–3/8"ø x 1" LONG BOLTS AND 2 WASHERS.
E	1	3/8"ø x 1 1/4" LONG BONDING BOLT WITH 1 NUT AND 2 WASHERS.
F	4	PLASTIC NUT COVERS FOR 1 1/2" NUTS.
G	1	PLASTIC END CAP
H	4	LEVELING SHIMS

NOTES

1. SEE STANDARD SPECIFICATIONS & SPECIAL PROVISIONS FOR ADDITIONAL INFORMATION.
2. POLE SHALL BE INSTALLED PLUMB.
3. ALL POLES, ARMS AND EXTENSIONS SHALL BE SUPPLIED WITH A GALVANIZED FINISH.
4. APPLY GREASE TO ANCHOR BOLT THREADS.
5. TOUCH UP ANY SCRATCHES IN GALVANIZED SURFACES WITH COLD GALVANIZING COMPOUND.
6. ALL DIMENSIONS ARE IN MILLIMETERS UNLESS OTHERWISE NOTED.
7. BOLT, WASHERS, AND SINGLE NUT SHALL CONFORM TO ASTM F3125 GRADE A325. GRADE SAE 5 BOLTS WITH THE FOLLOWING SPECIFICATIONS MAY BE SUBSTITUTED: 5/8" DIAMETER, 3" LENGTH, 2 WASHERS, AND 2 NUTS. CONNECTION INSTALLATION TO BE IN ACCORDANCE WITH "TURN–OF–NUT" METHOD SPECIFIED IN CSA S6.

NOT TO SCALE

BRITISH COLUMBIA | Ministry of Transportation and Infrastructure

No.	Revision	Date
G	GENERAL REVISIONS AND NEW DRAWING NUMBER	APR 20
F	GENERAL REVISIONS	APR 17
E	TYPE 1 & ARM FLANGE BOLTS CHANGED TO A325	DEC 10
D	ANTI–SEIZING LUBRICANT NOTED ON HANDHOLE BOLT	NOV 98
C	SIGN ARM & DRAWING NUMBERS REVISED	AUG 96

TYPE L SIGN POLE INSTALLATION DETAILS


Date Approved

30/09/93 E.L. (Signature on File)

Chief Highway Engineer

SPECIFICATION DRAWING No.

SP635–3.1.15

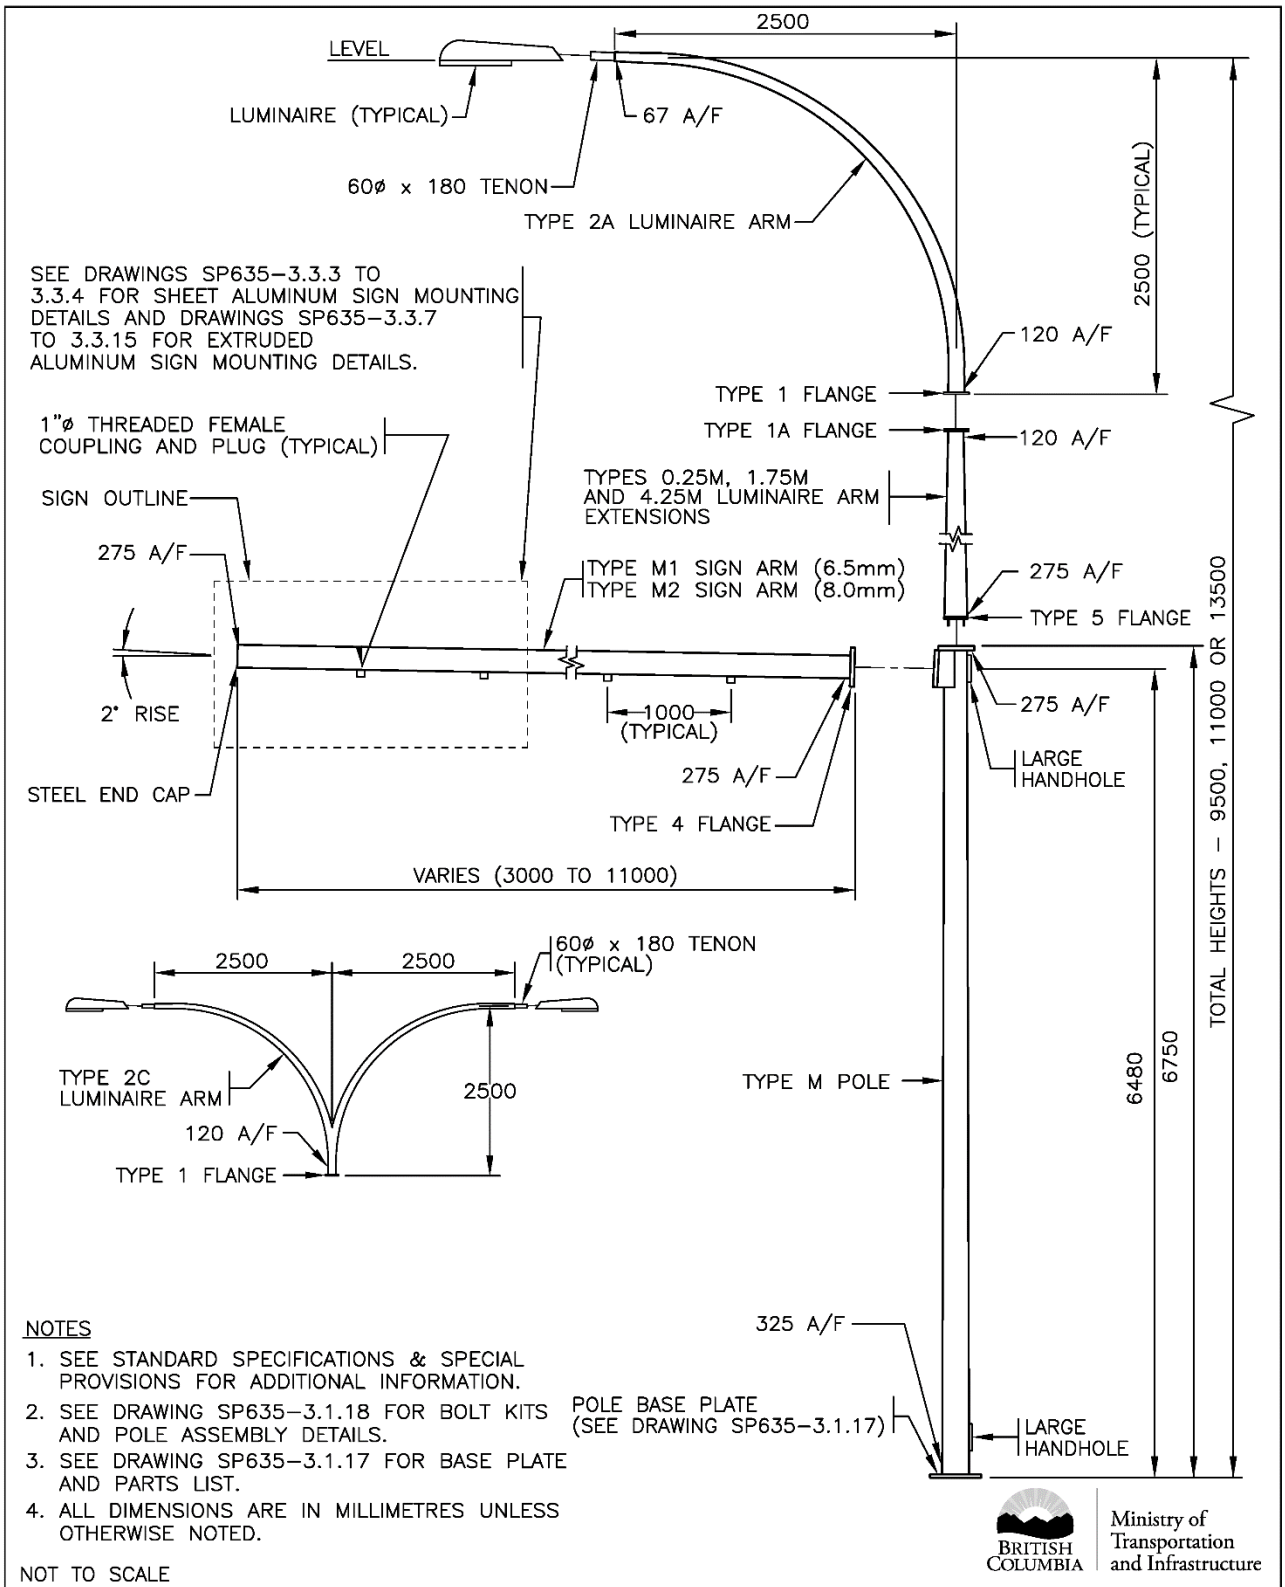

NOTES

1. SEE STANDARD SPECIFICATIONS & SPECIAL PROVISIONS FOR ADDITIONAL INFORMATION.
2. SEE DRAWING SP635-3.1.18 FOR BOLT KITS AND POLE ASSEMBLY DETAILS.
3. SEE DRAWING SP635-3.1.17 FOR BASE PLATE AND PARTS LIST.
4. ALL DIMENSIONS ARE IN MILLIMETRES UNLESS OTHERWISE NOTED.

NOT TO SCALE

BRITISH COLUMBIA | Ministry of Transportation and Infrastructure

No.	Revision	Date
F		
E		
D	PLYWOOD SIGN DETAILS REMOVED & NEW DRAWING NUMBER	APR 20
C	GENERAL REVISIONS	APR 17
B	DRAWING REFERENCES & DRAWING NUMBER REVISED	DEC 96
A	GENERAL REVISION	AUG 94

TYPE M SIGN POLE INSTALLATION DETAILS


Date Approved

30/09/93 E.L. (Signature on File)

Chief Highway Engineer

SPECIFICATION DRAWING No.

SP635-3.1.16

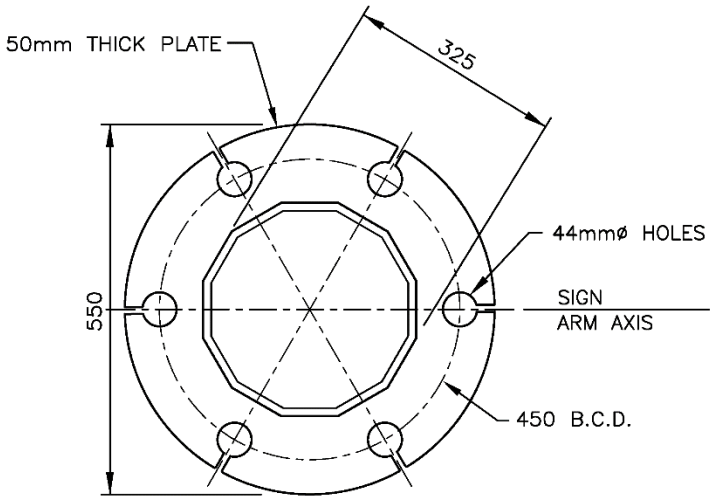

TYPE M POLE BASE PLATE

PARTS LIST FOR TYPE M SIGNAL POLE	
PART	MASS (kg)
TYPE [M] POLE	565
TYPE [M1] SIGN ARM (LENGTH VARIES)	55 PER METRE
TYPE [M2] SIGN ARM (LENGTH VARIES)	65 PER METRE
TYPE [4.25M] LUMINAIRE ARM EXTENSION – 4.25m	115
TYPE [1.75M] LUMINAIRE ARM EXTENSION – 1.75m	38
TYPE [0.25M] LUMINAIRE ARM EXTENSION – 0.25m	14
TYPE [2A] LUMINAIRE ARM	35
TYPE [2C] LUMINAIRE ARM	65
TYPE 1 FLANGE COVER PLATE [1FCP]	1.5
TYPE 3 FLANGE COVER PLATE [3FCP]	4
TYPE 4 FLANGE COVER PLATE [4FCP]	8
TYPE 5 FLANGE COVER PLATE [5FCP]	4
TYPE 4 TO 2 FLANGE ADAPTOR [FA]	75
POST TOP TENON [PTT]	5

* [ ] I.D. LABELS ON POLE

BRITISH COLUMBIA | Ministry of Transportation and Infrastructure

NOT TO SCALE

No.	Revision	Date
F		
E	NEW DRAWING NUMBER	APR 20
D	GENERAL REVISIONS	APR 17
C	DRAWING NUMBER REVISED	AUG 96
B	HOLE SIZES REVISED	AUG 95
A	GENERAL REVISION	AUG 94

TYPE M SIGN POLE INSTALLATION DETAILS


Date Approved

30/09/93 E.L. (Signature on File)

Chief Highway Engineer

SPECIFICATION DRAWING No.

SP635–3.1.17

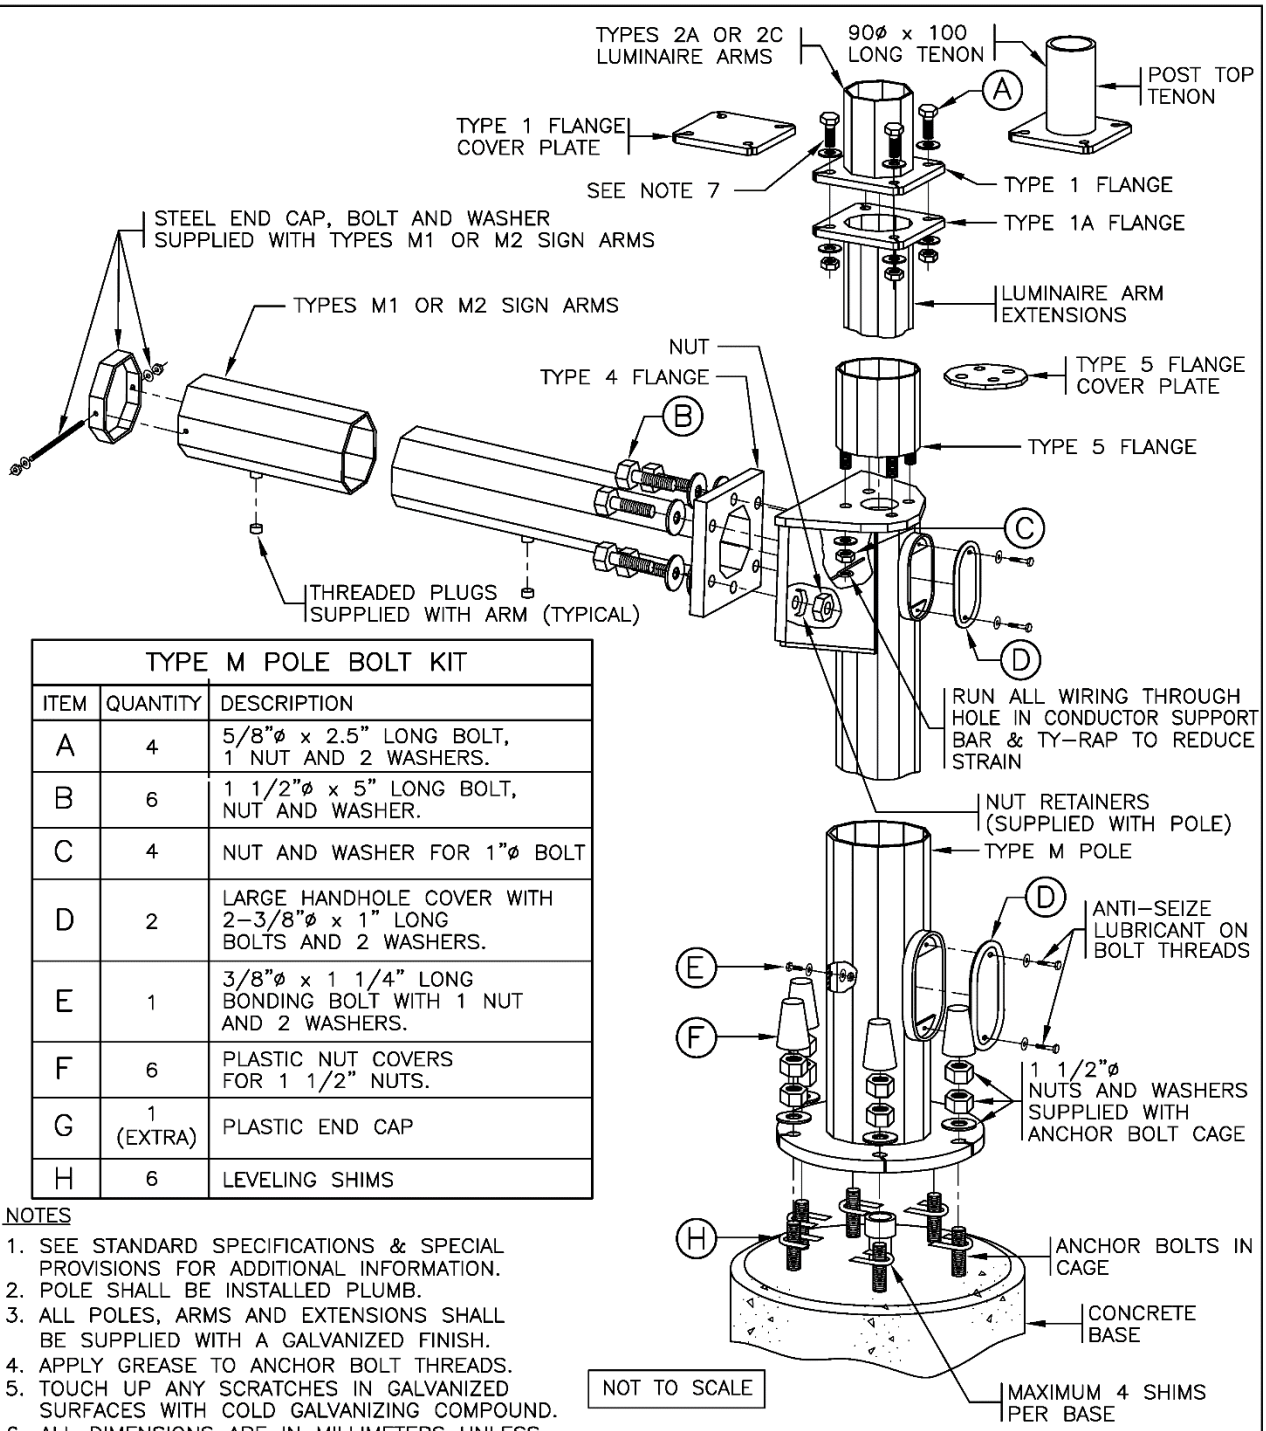

TYPE M POLE BOLT KIT		
ITEM	QUANTITY	DESCRIPTION
A	4	5/8"ø x 2.5" LONG BOLT, 1 NUT AND 2 WASHERS.
B	6	1 1/2"ø x 5" LONG BOLT, NUT AND WASHER.
C	4	NUT AND WASHER FOR 1"ø BOLT
D	2	LARGE HANDHOLE COVER WITH 2-3/8"ø x 1" LONG BOLTS AND 2 WASHERS.
E	1	3/8"ø x 1 1/4" LONG BONDING BOLT WITH 1 NUT AND 2 WASHERS.
F	6	PLASTIC NUT COVERS FOR 1 1/2" NUTS.
G	1 (EXTRA)	PLASTIC END CAP
H	6	LEVELING SHIMS

NOTES

1. SEE STANDARD SPECIFICATIONS & SPECIAL PROVISIONS FOR ADDITIONAL INFORMATION.
2. POLE SHALL BE INSTALLED PLUMB.
3. ALL POLES, ARMS AND EXTENSIONS SHALL BE SUPPLIED WITH A GALVANIZED FINISH.
4. APPLY GREASE TO ANCHOR BOLT THREADS.
5. TOUCH UP ANY SCRATCHES IN GALVANIZED SURFACES WITH COLD GALVANIZING COMPOUND.
6. ALL DIMENSIONS ARE IN MILLIMETERS UNLESS OTHERWISE NOTED.
7. BOLT, WASHERS, AND SINGLE NUT SHALL CONFORM TO ASTM F3125 GRADE A325. GRADE SAE 5 BOLTS WITH THE FOLLOWING SPECIFICATIONS MAY BE SUBSTITUTED: 5/8" DIAMETER, 3" LENGTH, 2 WASHERS, AND 2 NUTS. CONNECTION INSTALLATION TO BE IN ACCORDANCE WITH "TURN-OF-NUT" METHOD SPECIFIED IN CSA S6.

NOT TO SCALE

POLE ASSEMBLY DETAIL

BRITISH COLUMBIA — Ministry of Transportation and Infrastructure

No.	Revision	Date
G	GENERAL REVISIONS AND NEW DRAWING NUMBER	APR 20
F	GENERAL REVISIONS	APR 17
E	TYPE 1 & 8 FLANGE BOLTS CHANGED TO A325	DEC 10
D	ANTI-SEIZING LUBRICANT NOTED ON HANDHOLE BOLT	NOV 98
C	BOLT KIT LIST & DWG. No. REV'D & CONDUCTOR SUPPORT ADDED	AUG 96

TYPE M SIGN POLE INSTALLATION DETAILS


Date Approved

30/09/93 E.L. **(Signature on File)**

Chief Highway Engineer

SPECIFICATION DRAWING No.

SP635-3.1.18

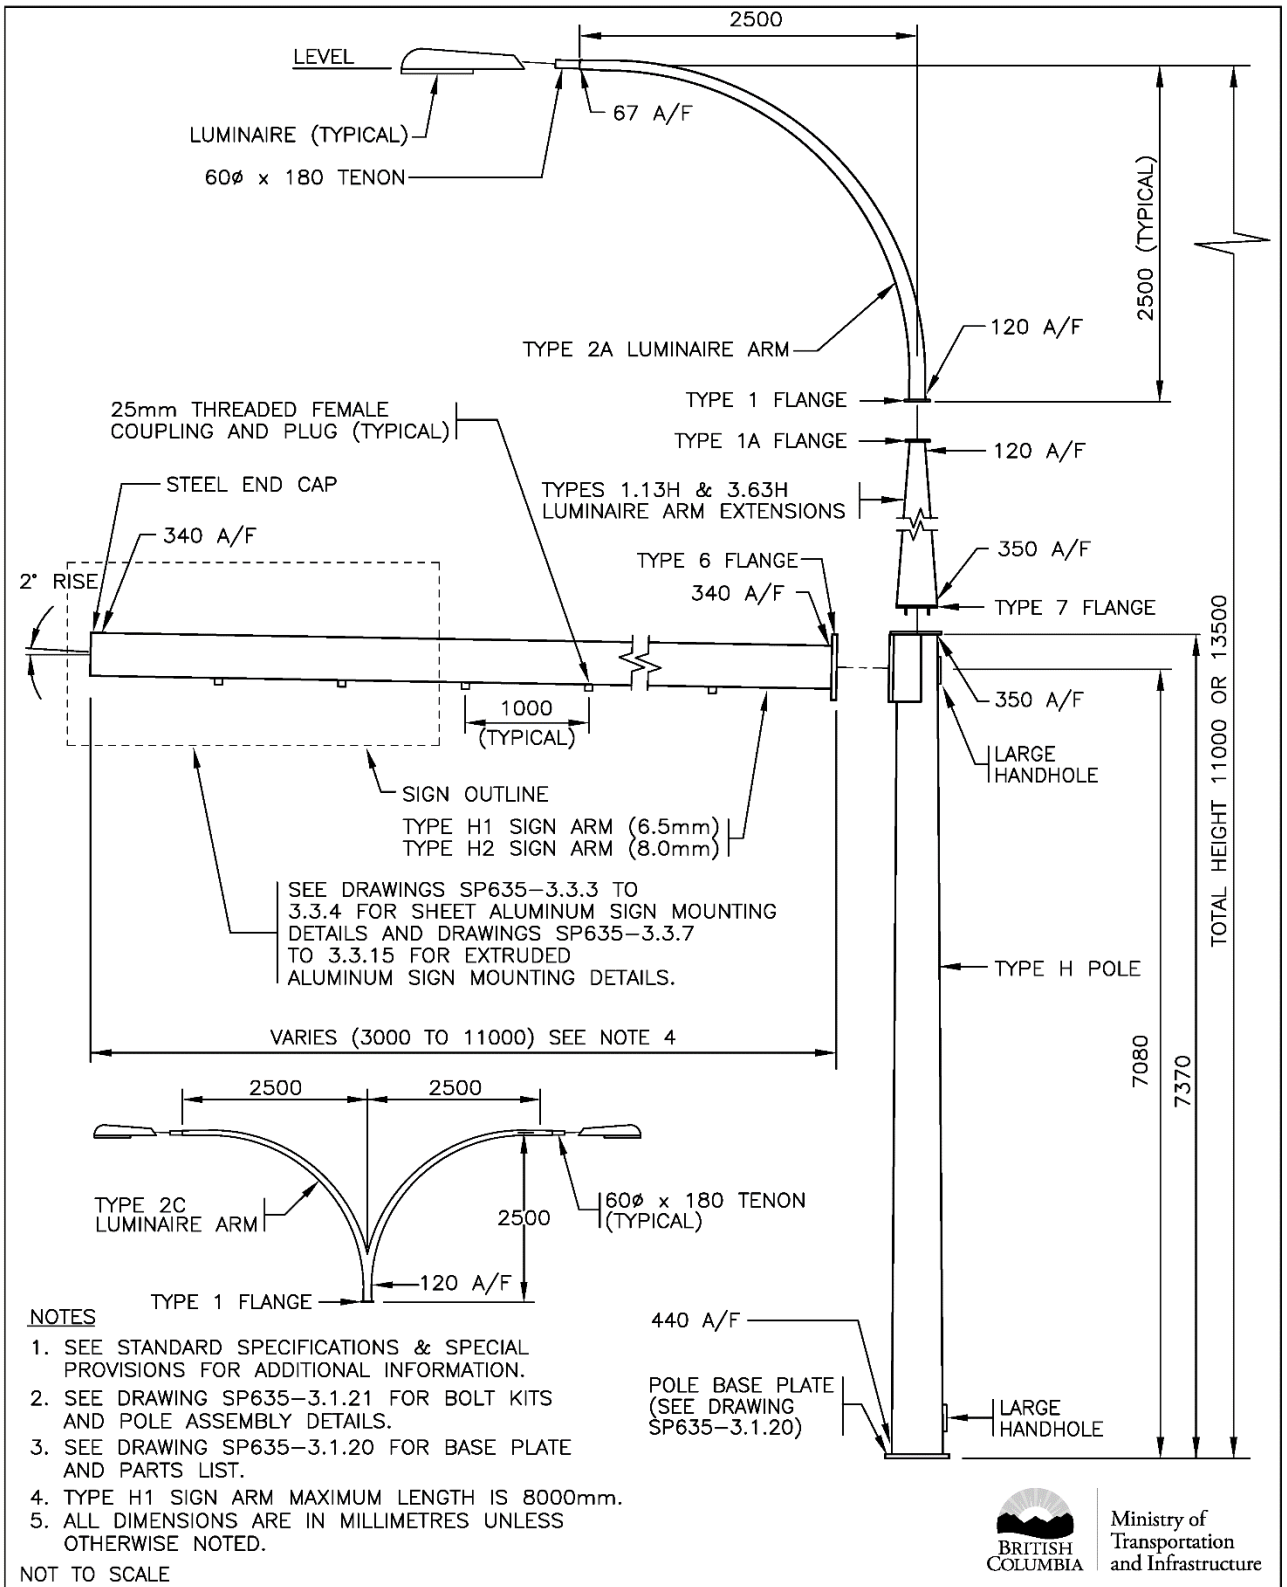

NOTES

1. SEE STANDARD SPECIFICATIONS & SPECIAL PROVISIONS FOR ADDITIONAL INFORMATION.
2. SEE DRAWING SP635-3.1.21 FOR BOLT KITS AND POLE ASSEMBLY DETAILS.
3. SEE DRAWING SP635-3.1.20 FOR BASE PLATE AND PARTS LIST.
4. TYPE H1 SIGN ARM MAXIMUM LENGTH IS 8000mm.
5. ALL DIMENSIONS ARE IN MILLIMETRES UNLESS OTHERWISE NOTED.

NOT TO SCALE


BRITISH COLUMBIA — Ministry of Transportation and Infrastructure

No.	Revision	Date
F		
E	H1 SIGN ARM MAX LENGTH ADDED	OCT 20
D	PLYWOOD SIGN DETAILS REMOVED & NEW DRAWING NUMBER	APR 20
C	GENERAL REVISIONS	APR 17
B	DRAWING NUMBER & DRAWING REFERENCES REVISED	DEC 96
A	GENERAL REVISION	AUG 94

TYPE H SIGN POLE INSTALLATION DETAILS

Date: **30/09/93** Approved: **E.L.** (Signature on File)
Chief Highway Engineer

SPECIFICATION DRAWING No.
SP635-3.1.19

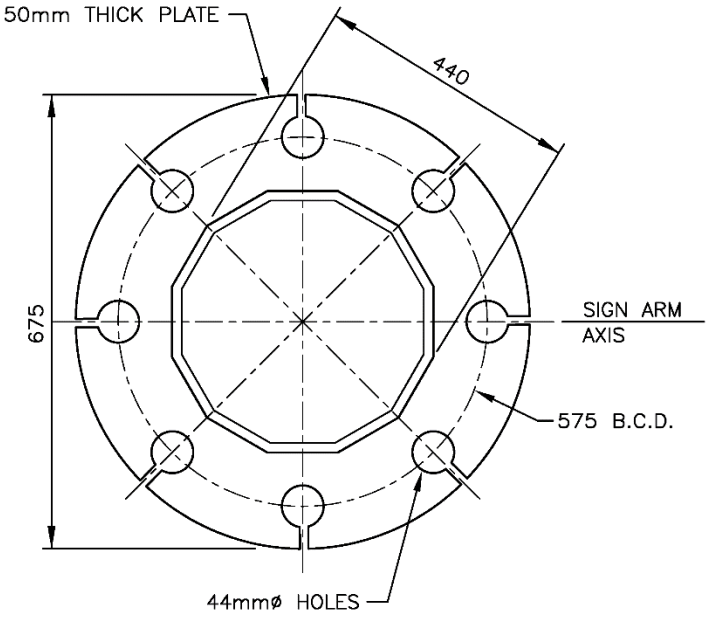

TYPE H POLE BASE PLATE

PARTS LIST FOR TYPE H SIGNAL POLE	
PART	MASS (kg)
TYPE [H] POLE	870
TYPE [H1] SIGN ARM (LENGTH VARIES) TYPE [H2] SIGN ARM (LENGTH VARIES)	73 PER METRE 86 PER METRE
TYPE [3.63H] LUMINAIRE ARM EXTENSION – 3.63m TYPE [1.13H] LUMINAIRE ARM EXTENSION – 1.13m	118 36
TYPE [2A] LUMINAIRE ARM TYPE [2C] LUMINAIRE ARM	35 65
TYPE 1 FLANGE COVER PLATE [1FCP] TYPE 6 FLANGE COVER PLATE [6FCP] TYPE 7 FLANGE COVER PLATE [7FCP]	1.5 12 6
POST TOP TENON [PTT]	5

* [ ] I.D. LABEL ON POLE

BRITISH COLUMBIA | Ministry of Transportation and Infrastructure

NOT TO SCALE

No.	Revision	Date
F		
E	NEW DRAWING NUMBER	APR 20
D	GENERAL REVISIONS	APR 17
C	DRAWING NUMBER REVISED	AUG 96
B	HOLE SIZE REVISED	AUG 95
A	GENERAL REVISION	AUG 94

TYPE H SIGN POLE INSTALLATION DETAILS


Date Approved

30/09/93 E.L. (Signature on File)

Chief Highway Engineer

SPECIFICATION DRAWING No.

SP635–3.1.20

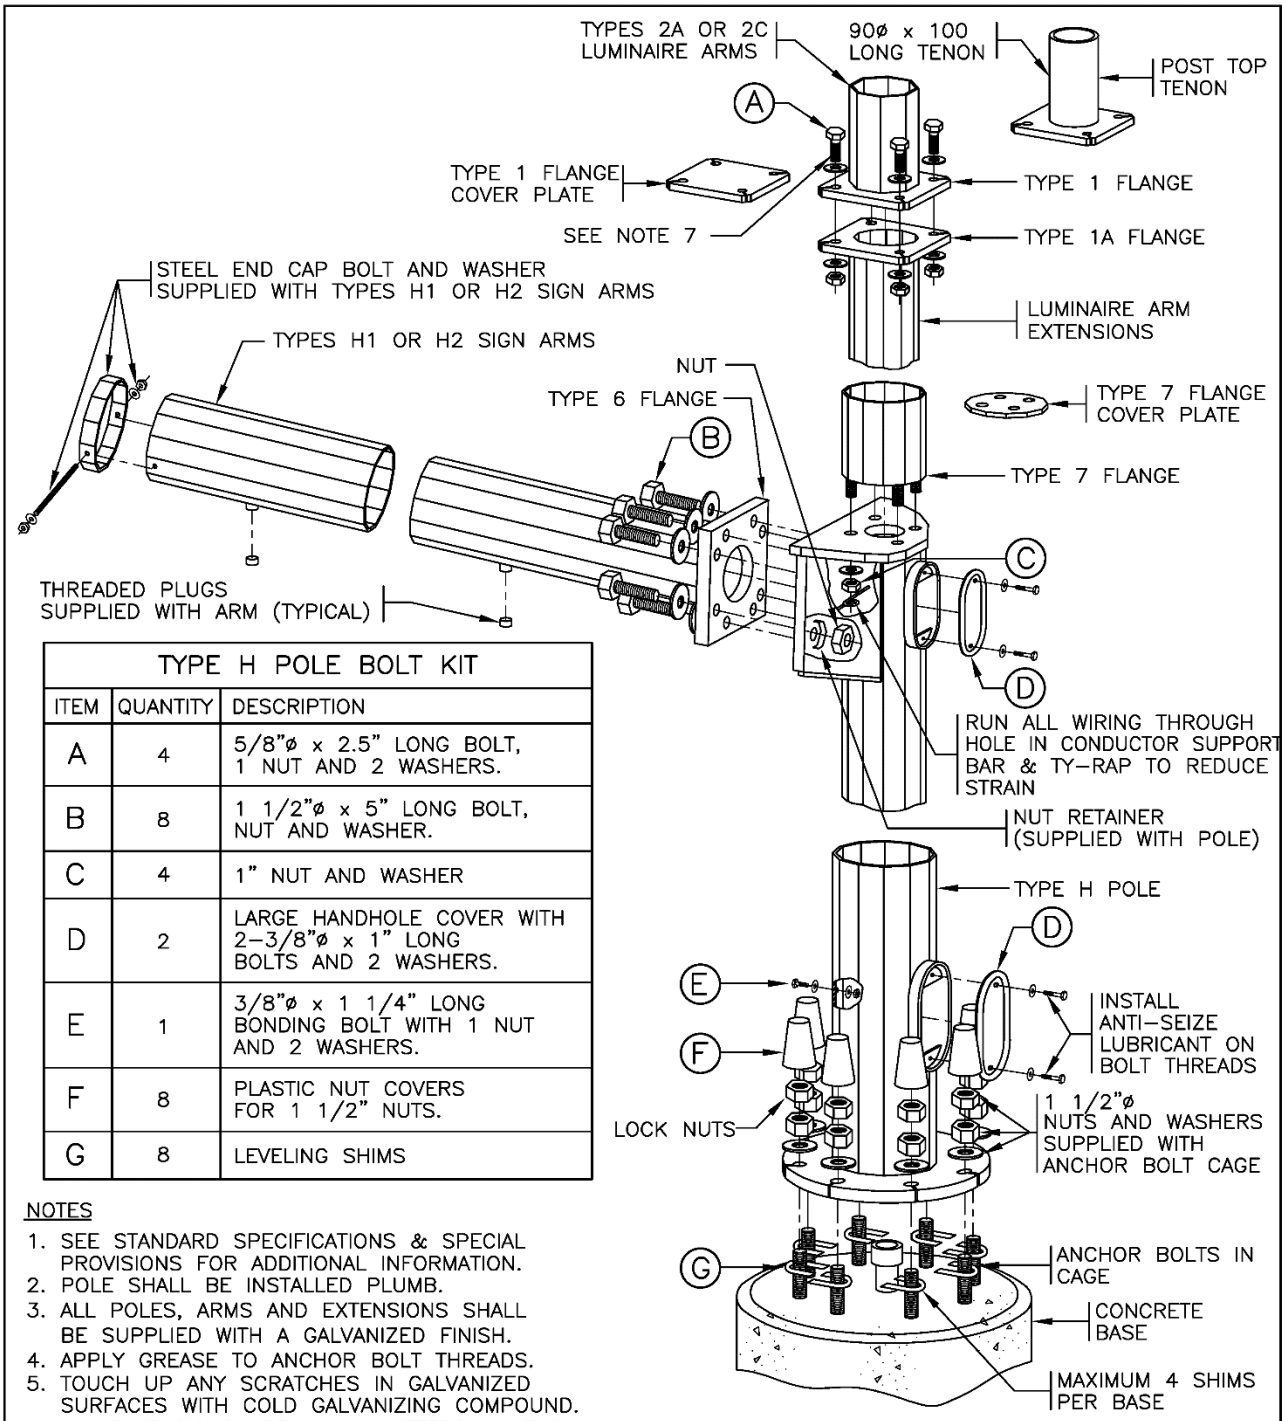

TYPE H POLE BOLT KIT		
ITEM	QUANTITY	DESCRIPTION
A	4	5/8"ø x 2.5" LONG BOLT, 1 NUT AND 2 WASHERS.
B	8	1 1/2"ø x 5" LONG BOLT, NUT AND WASHER.
C	4	1" NUT AND WASHER
D	2	LARGE HANDHOLE COVER WITH 2-3/8"ø x 1" LONG BOLTS AND 2 WASHERS.
E	1	3/8"ø x 1 1/4" LONG BONDING BOLT WITH 1 NUT AND 2 WASHERS.
F	8	PLASTIC NUT COVERS FOR 1 1/2" NUTS.
G	8	LEVELING SHIMS

NOTES

1. SEE STANDARD SPECIFICATIONS & SPECIAL PROVISIONS FOR ADDITIONAL INFORMATION.
2. POLE SHALL BE INSTALLED PLUMB.
3. ALL POLES, ARMS AND EXTENSIONS SHALL BE SUPPLIED WITH A GALVANIZED FINISH.
4. APPLY GREASE TO ANCHOR BOLT THREADS.
5. TOUCH UP ANY SCRATCHES IN GALVANIZED SURFACES WITH COLD GALVANIZING COMPOUND.
6. ALL DIMENSIONS ARE IN MILLIMETERS UNLESS OTHERWISE NOTED.
7. BOLT, WASHERS, AND SINGLE NUT SHALL CONFORM TO ASTM F3125 GRADE A325. GRADE SAE 5 BOLTS WITH THE FOLLOWING SPECIFICATIONS MAY BE SUBSTITUTED: 5/8" DIAMETER, 3" LENGTH, 2 WASHERS, AND 2 NUTS. CONNECTION INSTALLATION TO BE IN ACCORDANCE WITH "TURN-OF-NUT" METHOD SPECIFIED IN CSA S6.

POLE ASSEMBLY DETAIL

NOT TO SCALE

BRITISH COLUMBIA | Ministry of Transportation and Infrastructure

No.	Revision	Date
G	GENERAL REVISIONS AND NEW DRAWING NUMBER	APR 20
F	GENERAL REVISIONS	APR 17
E	TYPE 1 & ARM FLANGE BOLTS CHANGED TO A325	DEC 10
D	ANTI-SEIZE LUBRICANT NOTED ON HANDHOLE BOLT	NOV 98
C	DRAWING NUMBER REVISED & CONDUCTOR SUPPORT ADDED	AUG 96

TYPE H SIGN POLE INSTALLATION DETAILS


Date Approved

30/09/93 E.L. (Signature on File)


Chief Highway Engineer

SPECIFICATION DRAWING No.


SP635-3.1.21

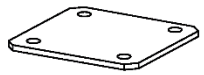


TYPE 1 & 1A FLANGE COVER PLATE

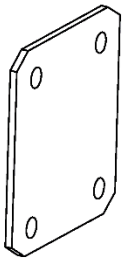


TYPE 2 FLANGE COVER PLATE

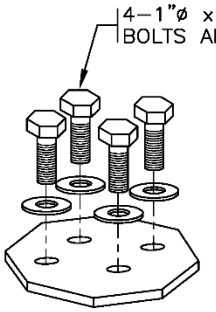


TYPE 3 FLANGE COVER PLATE

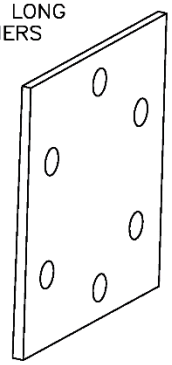


TYPE 4 FLANGE COVER PLATE

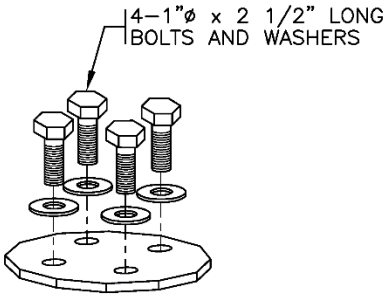


TYPE 5 FLANGE COVER PLATE

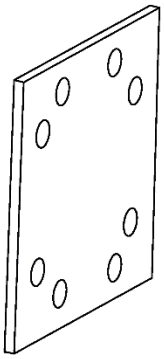


TYPE 6 FLANGE COVER PLATE

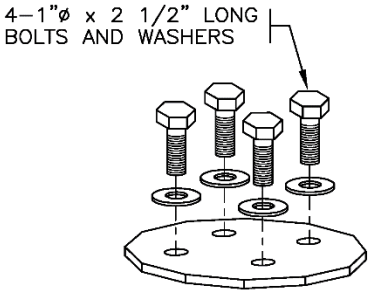


TYPE 7 FLANGE COVER PLATE

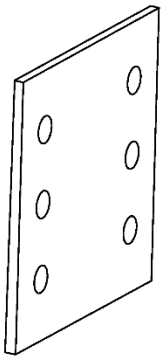

TYPE S FLANGE COVER PLATE

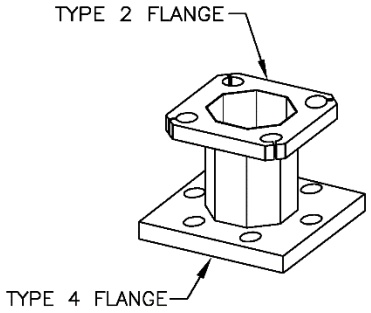

TYPE 4 TO TYPE 2 FLANGE ADAPTOR

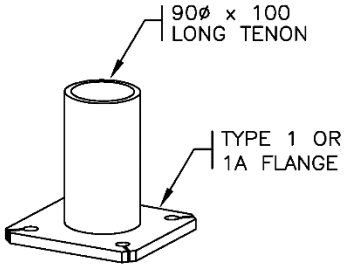

POST TOP TENON

NOTES

1. SEE STANDARD SPECIFICATIONS & SPECIAL PROVISIONS FOR ADDITIONAL INFORMATION.

NOT TO SCALE


BRITISH COLUMBIA Ministry of Transportation and Infrastructure

No.	Revision	Date
F		
E		
D		
C		
B	GENERAL REVISIONS	APR 17
A	TYPE S FLANGE COVER PLATE ADDED	OCT 03

SIGN POLE ACCESSORIES


Date: **14/11/03** Approved: **D.N. (Signature on File)** Chief Engineer

SPECIFICATION DRAWING No. SP635–3.1.22

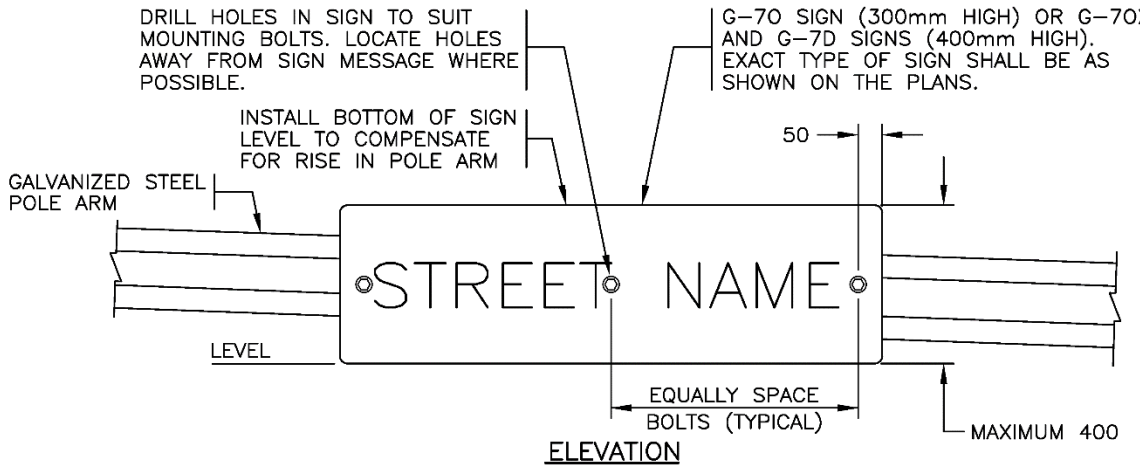

ELEVATION

SIGN WIDTH	NUMBER OF BOLTS
900	3
1200	4
1500	5
1800	6
2100	7

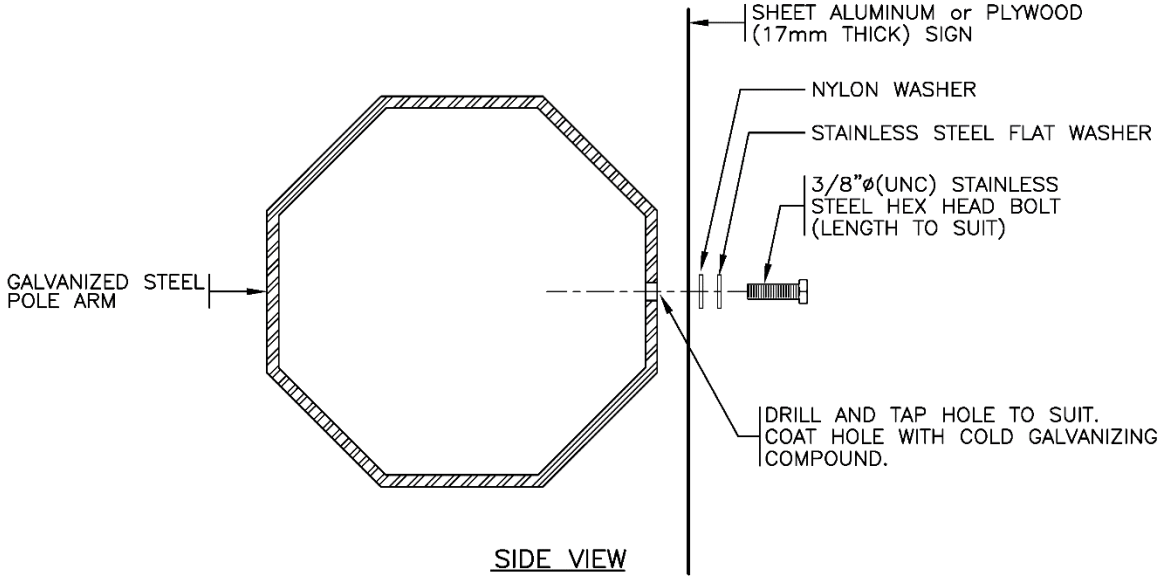

SIDE VIEW

NOTES

1. SEE STANDARD SPECIFICATIONS & SPECIAL PROVISIONS FOR ADDITIONAL INFORMATION.
2. POSITION SIGN ON POLE ARM AS INDICATED ON THE PLANS.
3. ALL DIMENSIONS ARE IN MILLIMETRES UNLESS OTHERWISE NOTED.

NOT TO SCALE

BRITISH COLUMBIA Ministry of Transportation and Infrastructure

No.	Revision	Date
F		
E	GENERAL REVISIONS	APR 20
D	GENERAL REVISIONS	APR 17
C	GENERAL REVISIONS	AUG 96
B	SIGN NUMBER AND SIZES REVISED	AUG 95
A	GENERAL REVISION	AUG 94

OVERHEAD STREETNAME SIGN INSTALLATION DETAILS (ON SIGNAL POLE ARMS)


Date Approved

30/09/93 E.L. (Signature on File)

Chief Highway Engineer

SPECIFICATION DRAWING No.

SP635–3.2.1

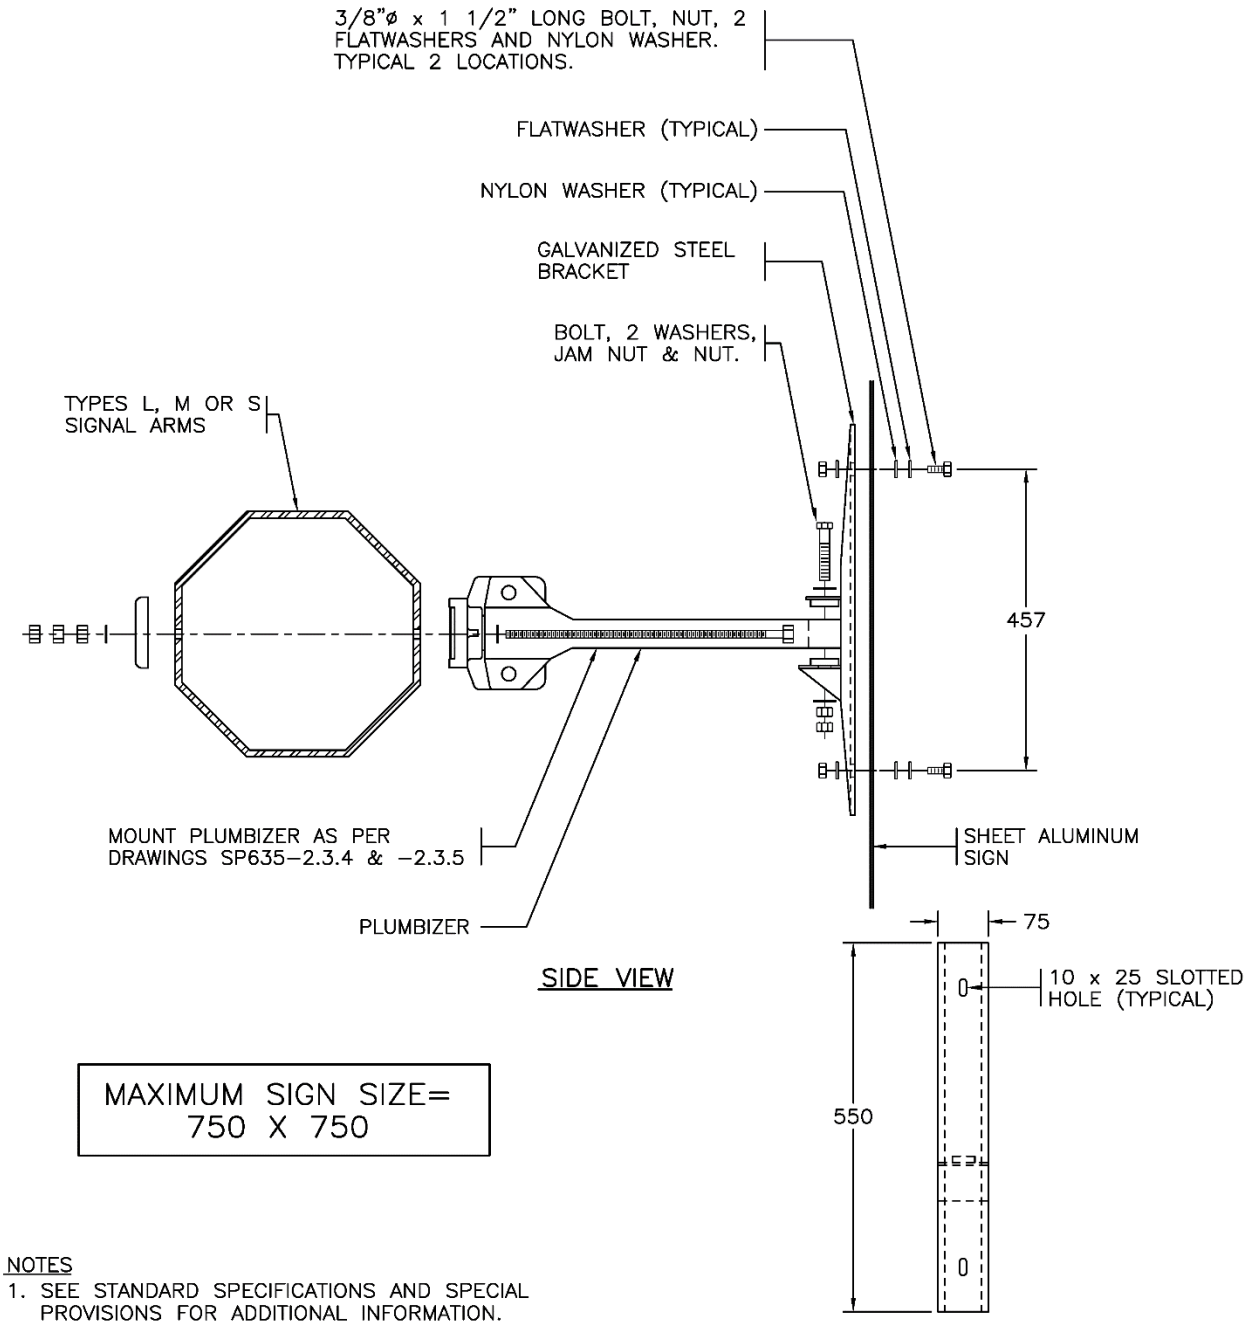

MAXIMUM SIGN SIZE= 750 X 750

NOTES
1. SEE STANDARD SPECIFICATIONS AND SPECIAL PROVISIONS FOR ADDITIONAL INFORMATION.
2. ALL DIMENSIONS ARE IN MILLIMETRES UNLESS OTHERWISE NOTED.
3. AIM SIGN AS PER PLANS.

NOT TO SCALE


BRITISH COLUMBIA Ministry of Transportation and Infrastructure

No.	Revision	Date
F		
E	NOTE 3 UPDATED	APR 20
D	GENERAL REVISIONS	APR 17
C	NYLOCK NUT REMOVED. NUT ADDED	AUG 99
B	REFERENCED DWG Nos. REVISED	DEC 98
A	PLUMBIZER BOLTING REVISED	AUG 95

SMALL OVERHEAD SIGN INSTALLATION DETAILS (ON TYPE S, L & M SIGNAL POLES)

Date: **18/11/94** Approved: **E.L.** **(Signature on File)**
Chief Highway Engineer

SPECIFICATION DRAWING No.
SP635-3.2.2

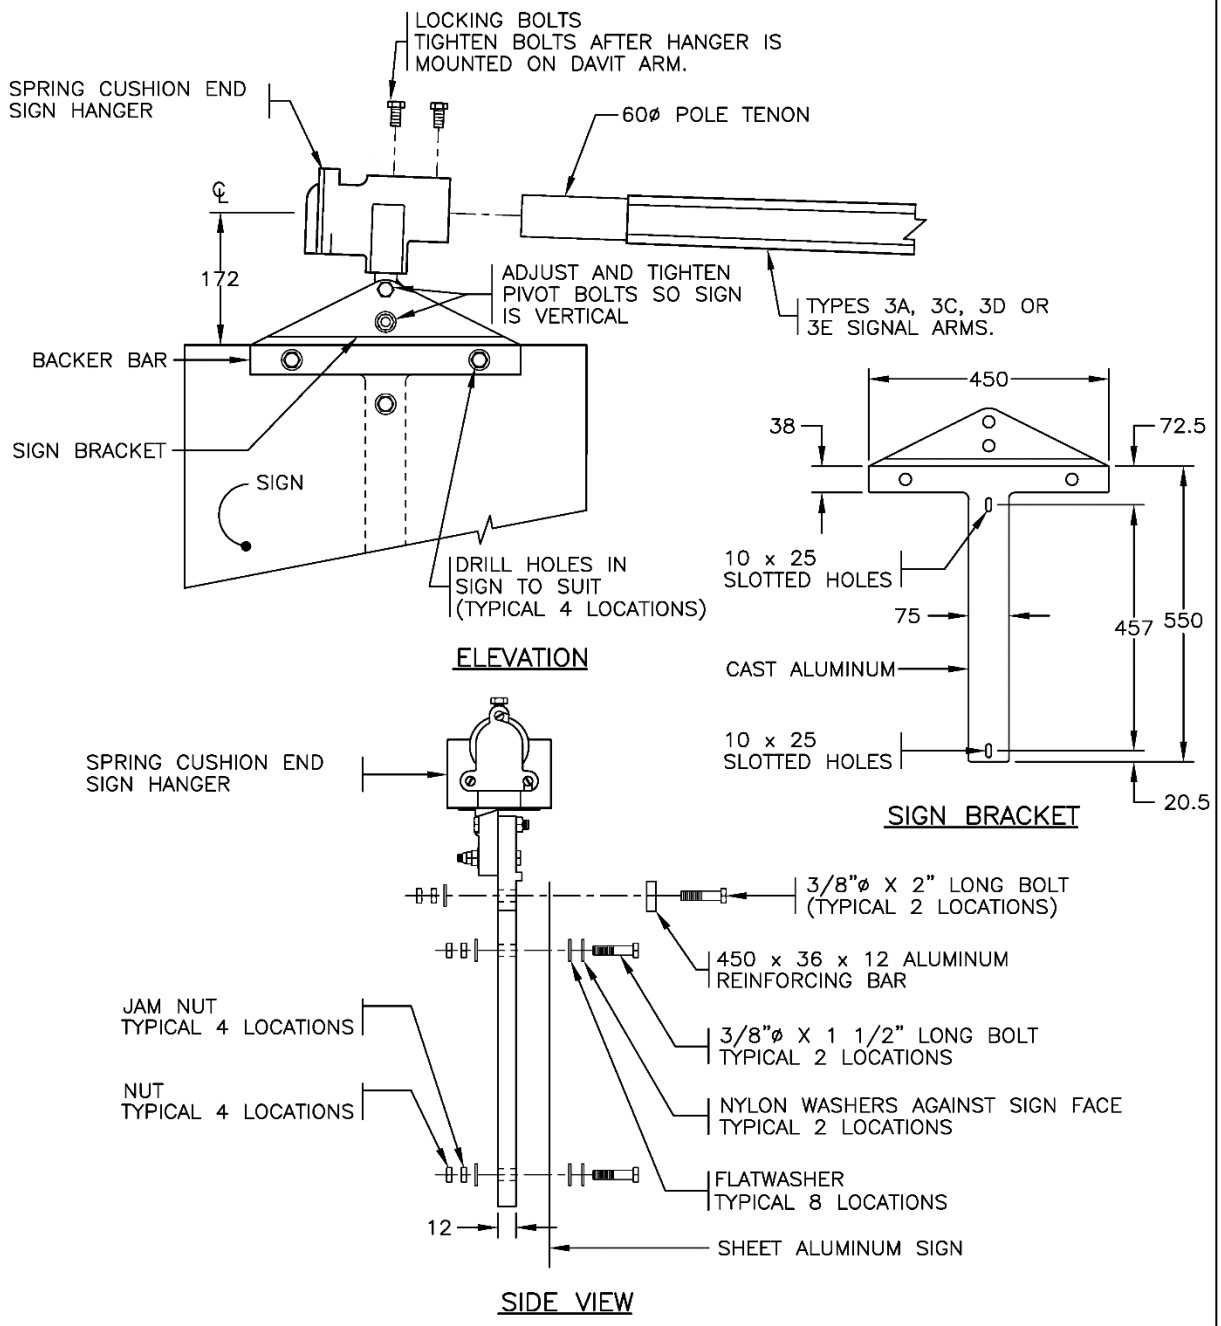

NOTES

1. SEE STANDARD SPECIFICATIONS & SPECIAL PROVISIONS FOR ADDITIONAL INFORMATION.
2. AIM SIGNS AS PER PLANS.
3. ALL DIMENSIONS ARE IN MILLIMETRES UNLESS OTHERWISE NOTED.

MAXIMUM SIGN SIZE = 750 X 750

NOT TO SCALE

Ministry of Transportation and Infrastructure
BRITISH COLUMBIA

No.	Revision	Date
F		
E	NOTE 2 UPDATED	APR 20
D	GENERAL REVISIONS	APR 17
C	NYLOCK NUT REMOVED. NUT ADDED	AUG 99
B	SIGN BOLTING TO BRACKET MODIFIED	AUG 95
A	GENERAL REVISION	AUG 94

SMALL OVERHEAD SIGN INSTALLATION DETAILS (ON TYPE 3 SIGNAL ARMS)


Date Approved

30/09/93 E.L. **(Signature on File)**

Chief Highway Engineer

SPECIFICATION DRAWING No.

SP635–3.2.3

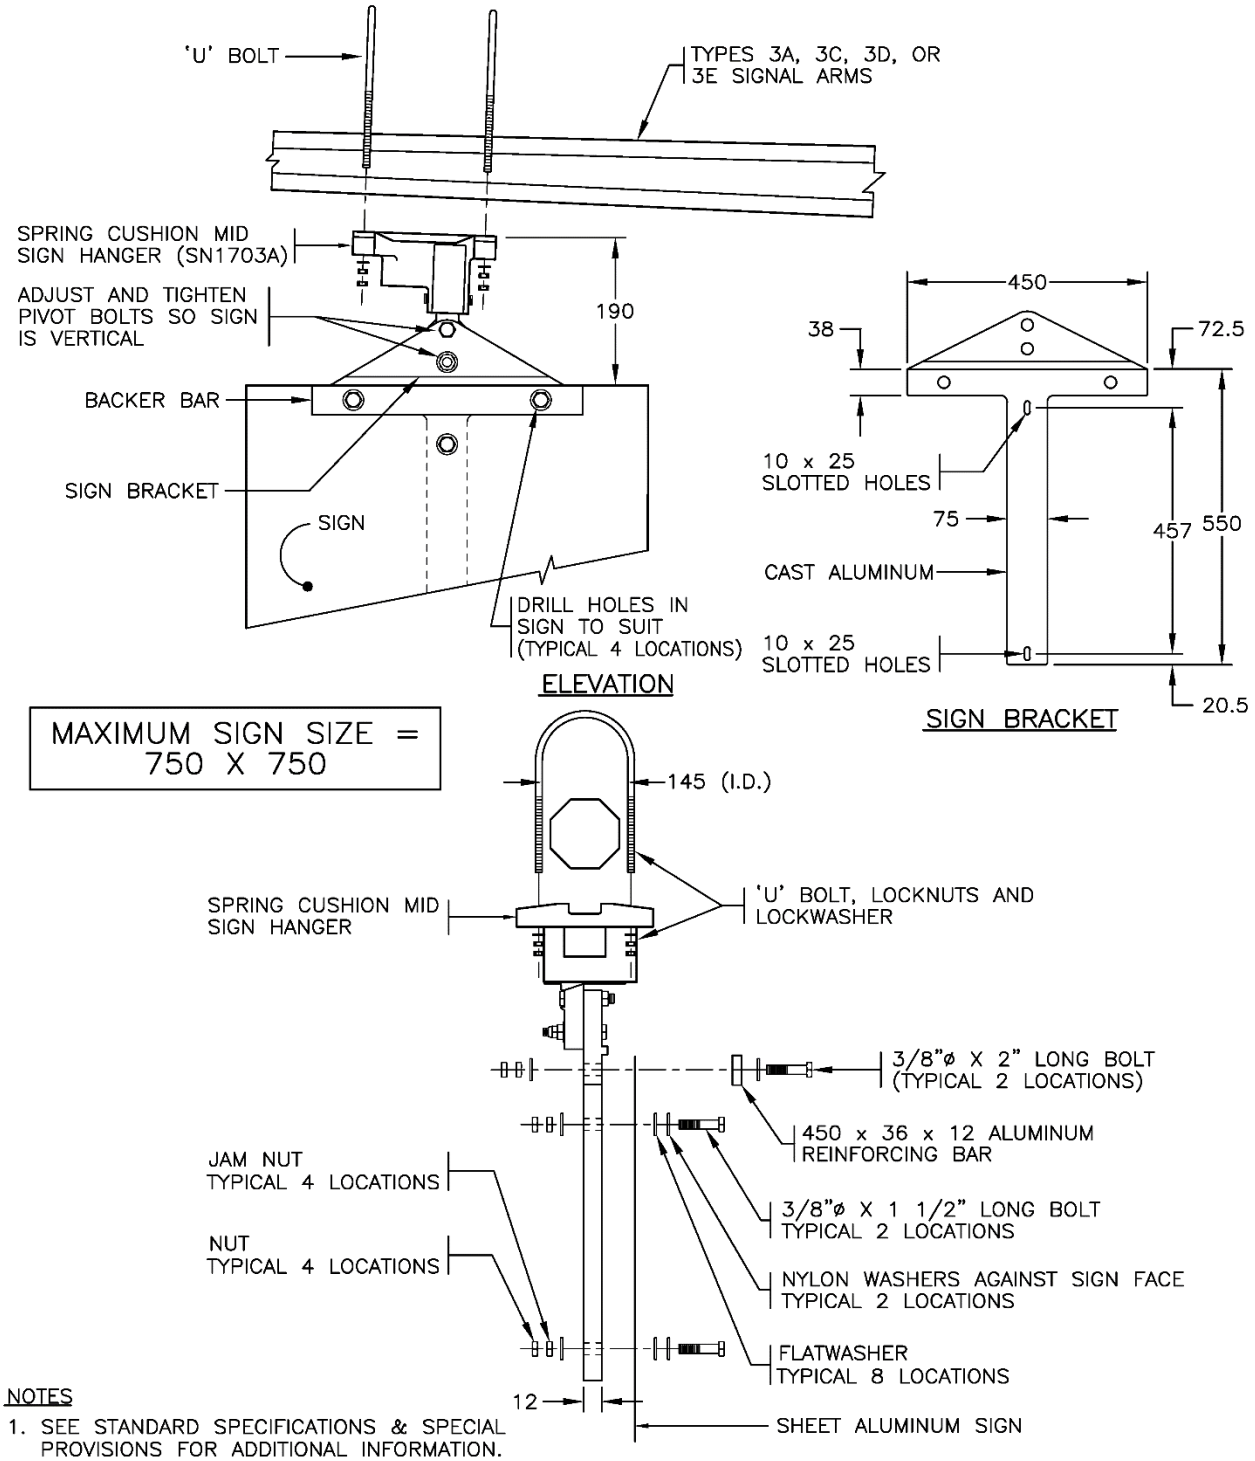

NOTES

1. SEE STANDARD SPECIFICATIONS & SPECIAL PROVISIONS FOR ADDITIONAL INFORMATION.
2. AIM SIGNS AS PER PLANS.
3. ALL DIMENSIONS ARE IN MILLIMETRES UNLESS OTHERWISE NOTED.

NOT TO SCALE

BRITISH COLUMBIA — Ministry of Transportation and Infrastructure

No.	Revision	Date
F		
E	NOTE 2 UPDATED	APR 20
D	GENERAL REVISIONS	APR 17
C	NYLOCK NUT REMOVED. NUT ADDED	AUG 99
B	SIGN BOLTING TO BRACKET MODIFIED	AUG 95
A	GENERAL REVISION	AUG 94

SMALL OVERHEAD SIGN INSTALLATION DETAILS (ON TYPE 3 SIGNAL ARMS)


Date Approved

30/09/93 E.L. (Signature on File)


Chief Highway Engineer

SPECIFICATION DRAWING No.

SP635–3.2.4

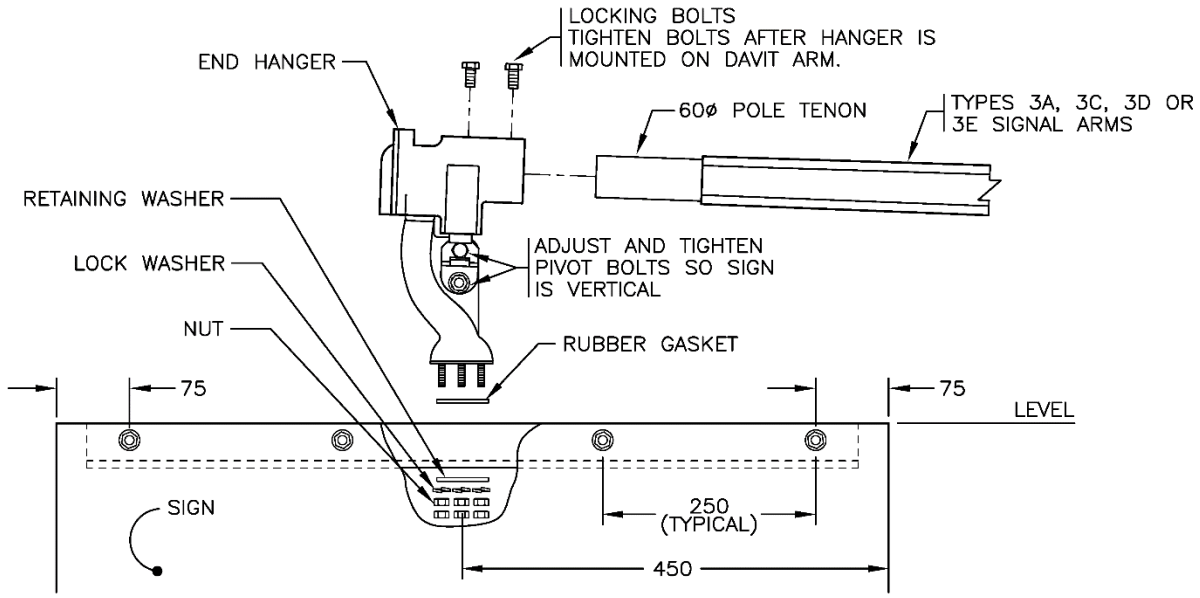

ELEVATION

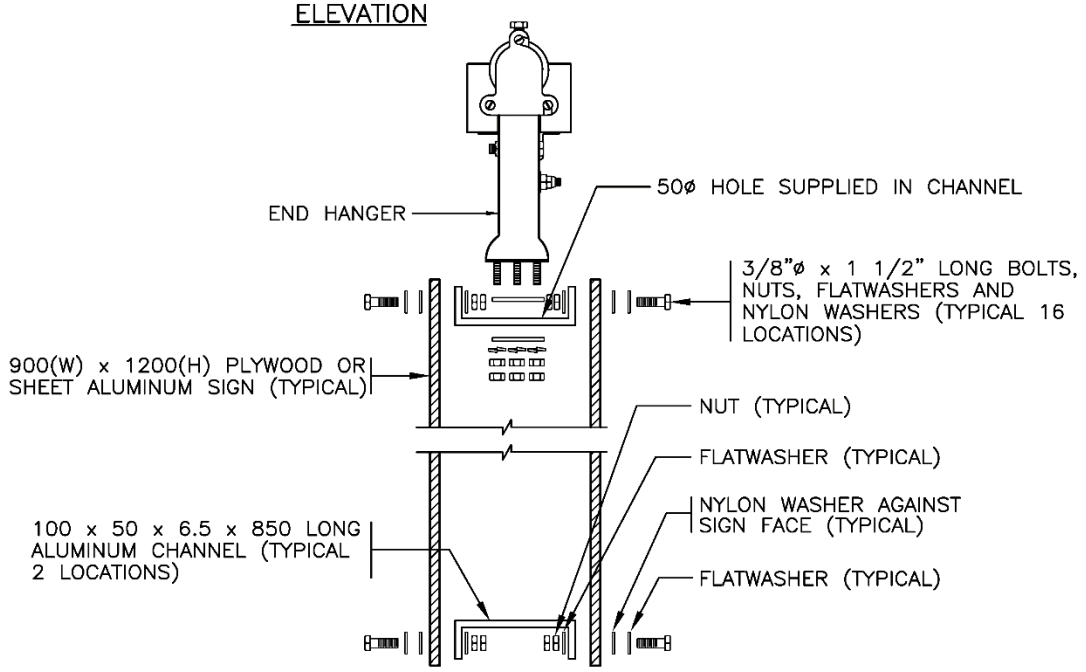

SIDE VIEW

NOTES

1. SEE STANDARD SPECIFICATIONS & SPECIAL PROVISIONS FOR ADDITIONAL INFORMATION.
2. AIM SIGN AS PER PLANS.
3. ALL DIMENSIONS ARE IN MILLIMETRES UNLESS OTHERWISE NOTED.

MAXIMUM SIGN SIZE = 1200 X 900

NOT TO SCALE

BRITISH COLUMBIA | Ministry of Transportation and Infrastructure

No.	Revision	Date
F		
E	NOTE 2 UPDATED	APR 20
D	GENERAL REVISIONS	APR 17
C	SHEET ALUMINUM SIGN ADDED	APR 05
B	NYLOCK NUTS REMOVED. DOUBLE NUTS ADDED	AUG 99
A	GENERAL REVISION	AUG 94

2–WAY SMALL OVERHEAD SIGN INSTALLATION DETAILS (ON TYPE 3 SIGNAL ARMS)


Date Approved

30/09/93 E.L. (Signature on File)


Chief Highway Engineer

SPECIFICATION DRAWING No.

SP635–3.2.5

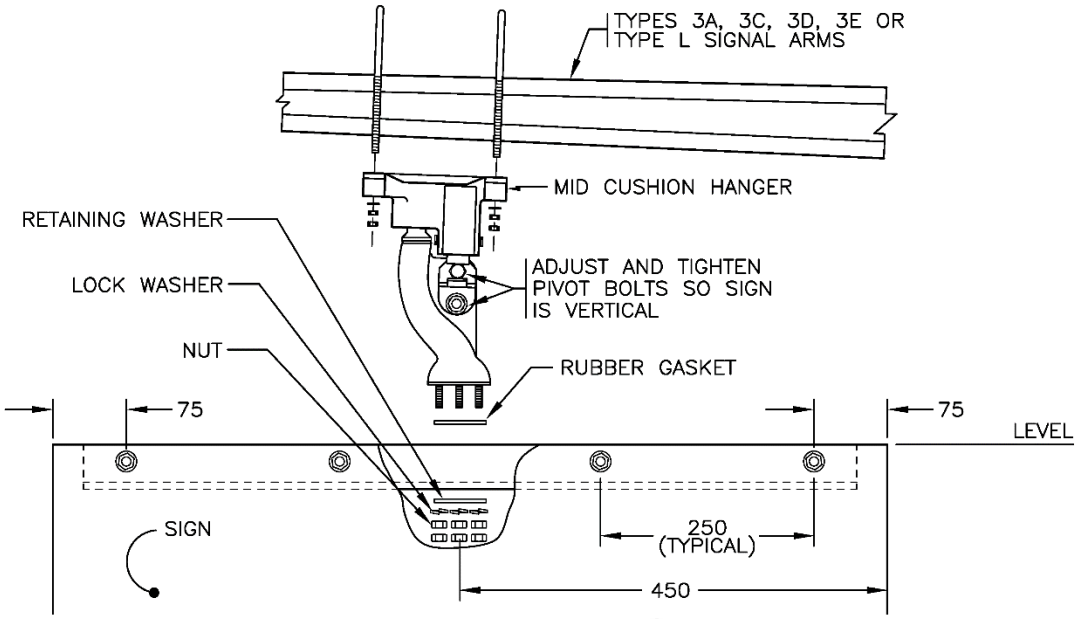

ELEVATION

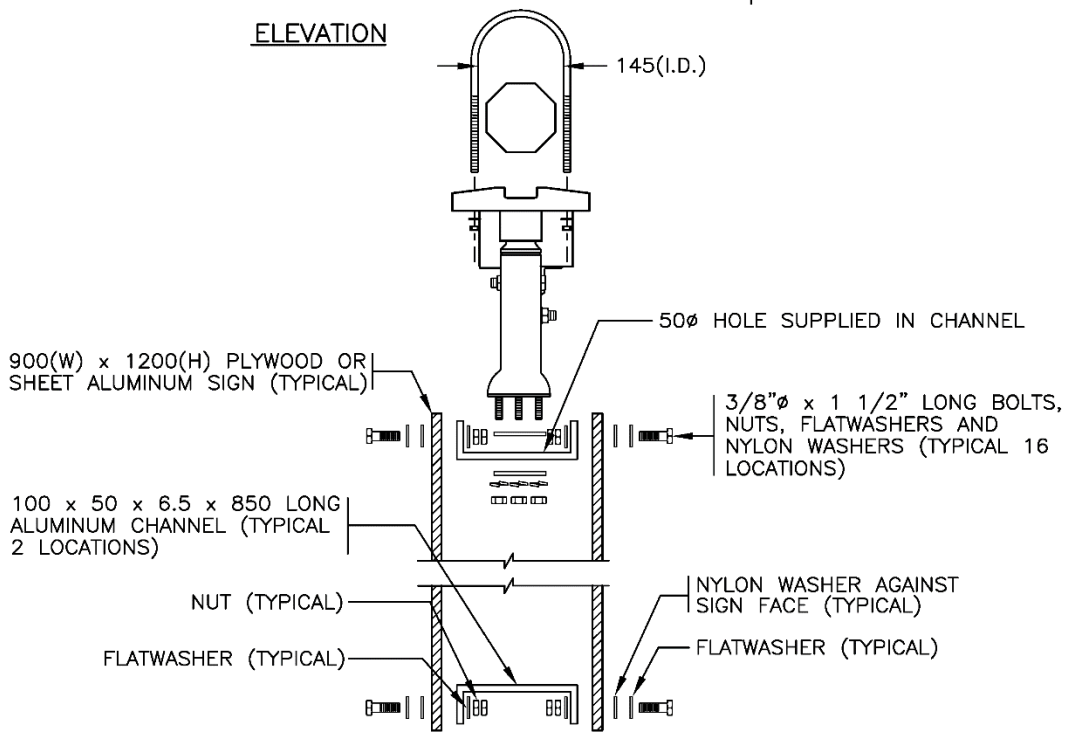

SIDE VIEW

MAXIMUM SIGN SIZE = 1200 X 900

NOTES

1. SEE STANDARD SPECIFICATIONS & SPECIAL PROVISIONS FOR ADDITIONAL INFORMATION.
2. AIM SIGN AS PER PLANS.
3. ALL DIMENSIONS ARE IN MILLIMETRES UNLESS OTHERWISE NOTED.

NOT TO SCALE

BRITISH COLUMBIA Ministry of Transportation and Infrastructure

No.	Revision	Date
F	GENERAL REVISIONS	OCT 20
E	NOTE 2 UPDATED	APR 20
D	GENERAL REVISIONS	APR 17
C	SHEET ALUMINUM SIGN ADDED	APR 05
B	NYLOCK NUTS REMOVED. DOUBLE NUTS ADDED	AUG 99
A	GENERAL REVISION	AUG 94

2–WAY SMALL OVERHEAD SIGN INSTALLATION DETAILS (FOR TYPE 3 AND L SIGNAL ARMS)


Date Approved

30/09/93 E.L. (Signature on File)

Chief Highway Engineer

SPECIFICATION DRAWING No.

SP635–3.2.6

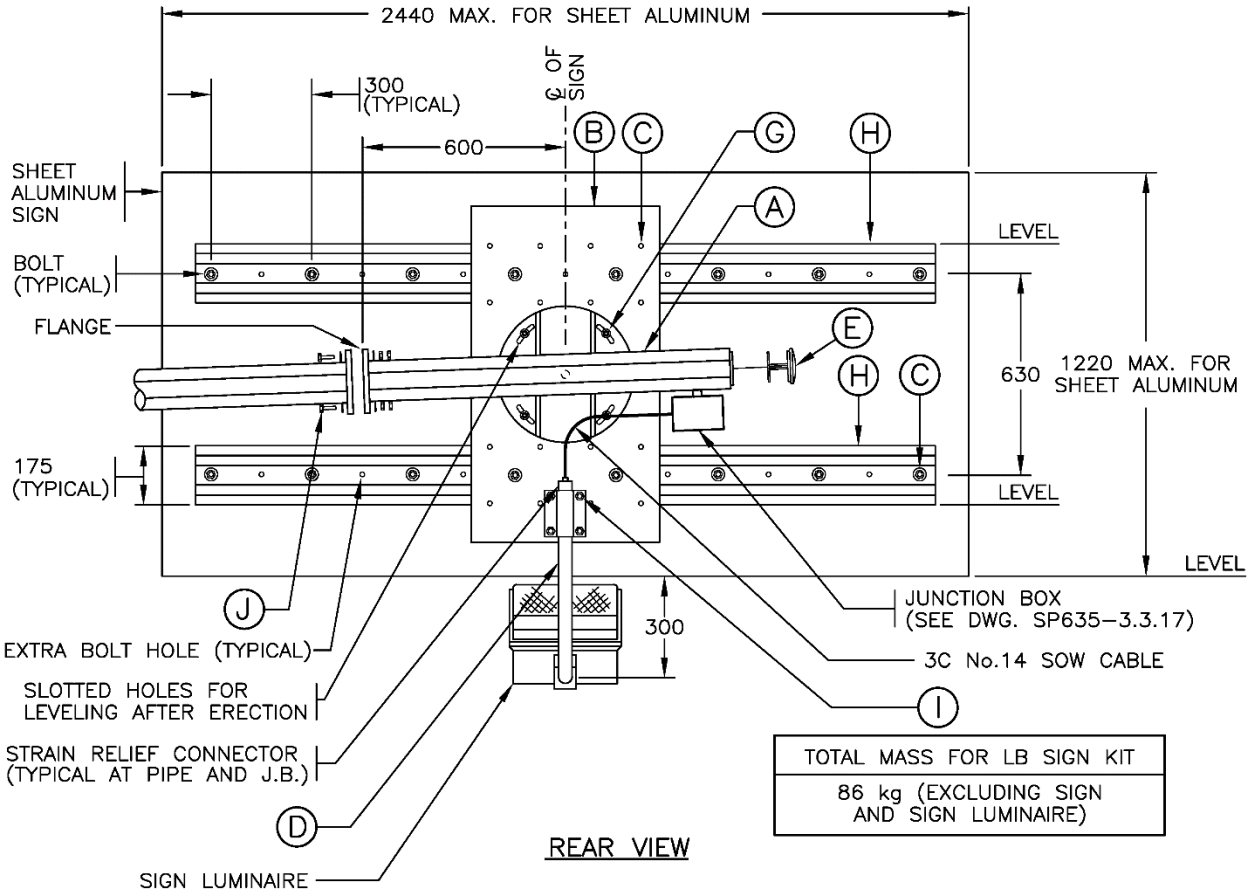

TOTAL MASS FOR LB SIGN KIT
86 kg (EXCLUDING SIGN AND SIGN LUMINAIRE)

TYPE LB SIGN MOUNTING KIT		
ITEM	QUANTITY	DESCRIPTION
A	1	TYPE LB GALVANIZED SIGN ARM
B	1	550 x 1000 GALVANIZED SIGN SUPPORT MOUNTING PLATE
C	16	3/8"ø x 1 1/2" LONG BOLT, NUT, 2 FLATWASHERS, LOCKWASHER AND NYLON WASHER.
D	1	SIGN LUMINAIRE PIPE BRACKET
E	1	PLASTIC END CAP
F	1	PIPE MOUNTING CLAMP
G	4	1/2"ø x 1 1/4" LONG BOLT, FLATWASHER AND LOCKWASHER
H	2	2350 LONG GALVANIZED HORIZONTAL SIGN SUPPORTS
I	4	1/2"ø x 1 1/2" LONG BOLT, NUT, 2 FLATWASHERS AND LOCKWASHER
J	4	5/8"ø x 3" LONG BOLT, 2 NUTS AND 2 FLATWASHERS

SEE DRAWING SP635-3.3.2 FOR NOTES

SIGN LUMINAIRES SHALL BE USED ONLY WHEN SPECIFICALLY NOTED ON THE DESIGN DRAWINGS

NOT TO SCALE

BRITISH COLUMBIA Ministry of Transportation and Infrastructure

No.	Revision	Date
G	PLYWOOD SIGN REMOVED	APR 20
F	SHEET ALUMINUM SIGN ADDED	APR 05
E	SIGN LUMINAIRE NOTE ADDED	SEPT 00
D	J.B. DRAWING REFERENCE REVISED	DEC 98
C	J.B. DRAWING REFERENCE REVISED	DEC 96
B	LUMINAIRE CHANGED & J.B. ADDED	AUG 95

LARGE OVERHEAD GUIDE SIGN INSTALLATION DETAILS (UP TO 1220 X 2440 SHEET ALUMINUM)


Date Approved

30/09/93 E.L. (Signature on File)

Chief Highway Engineer

SPECIFICATION DRAWING No.

SP635-3.3.1

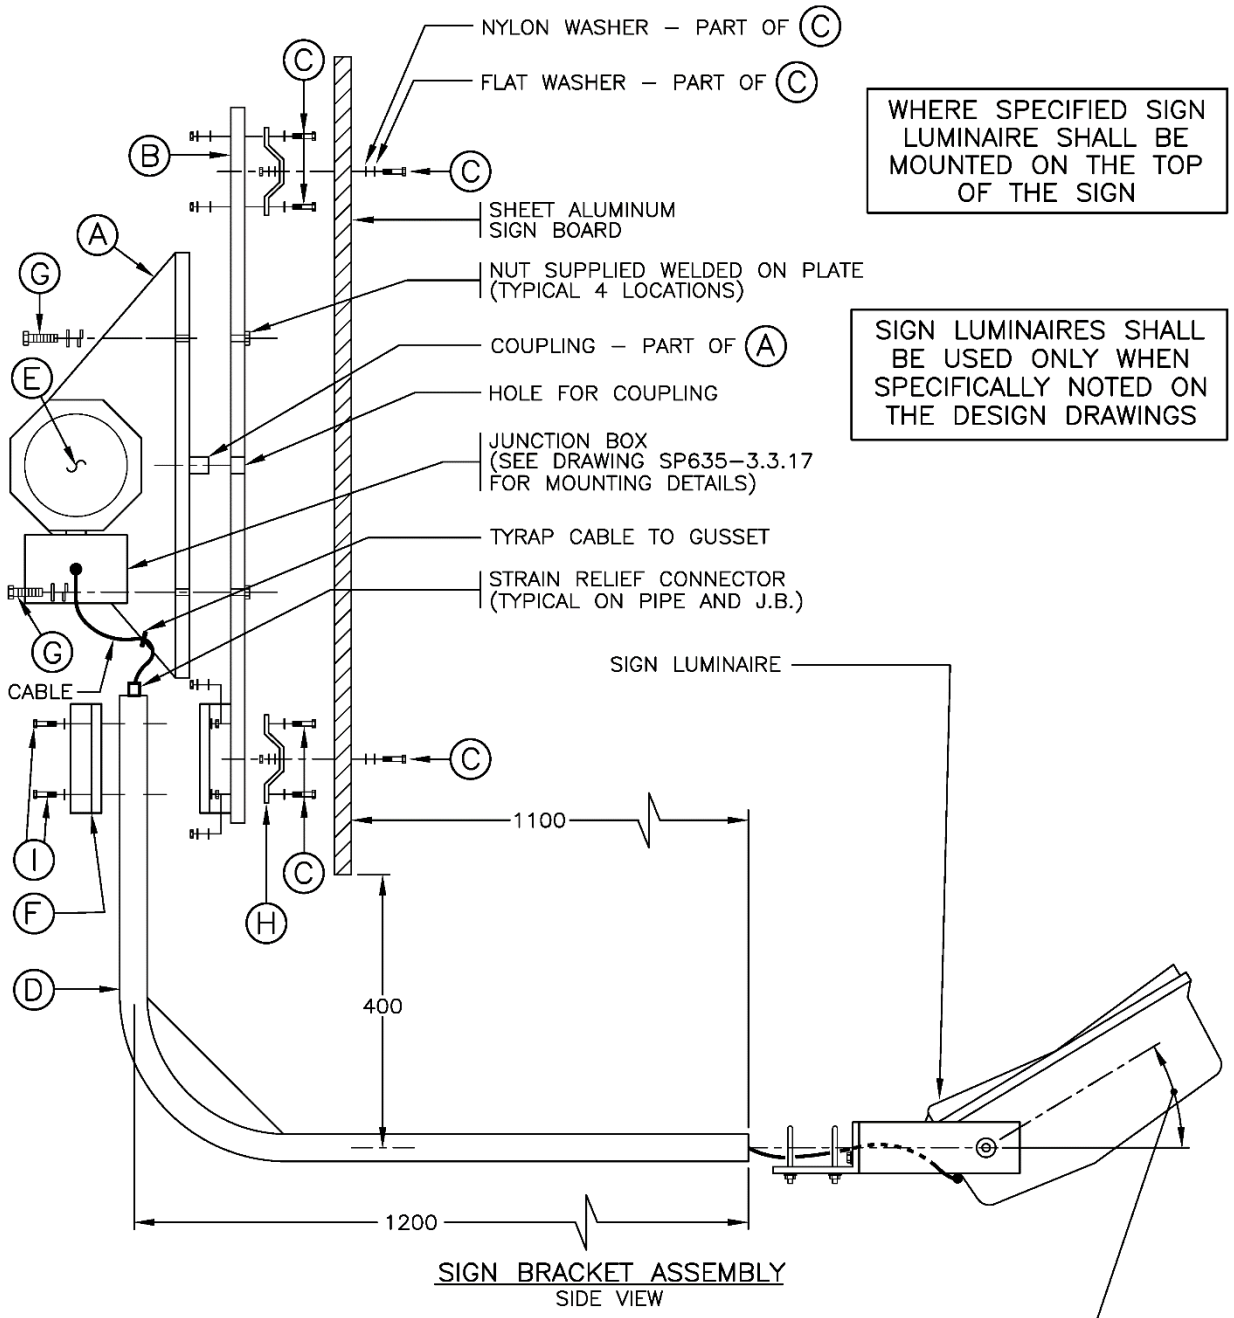

SIGN BRACKET ASSEMBLY
SIDE VIEW

NOTES

1. SEE STANDARD SPECIFICATIONS & SPECIAL PROVISIONS FOR ADDITIONAL INFORMATION.
2. ALL DIMENSIONS ARE IN MILLIMETRES UNLESS OTHERWISE NOTED.

SEE DRAWING SP635–3.3.1 FOR ADDITIONAL DETAILS

NOT TO SCALE

BRITISH COLUMBIA | Ministry of Transportation and Infrastructure

No.	Revision	Date
G	GENERAL REVISION	APR 20
F	SHEET ALUMINUM SIGN ADDED	APR 05
E	SIGN LUMINAIRE NOTE ADDED	SEPT 00
D	SIGN LUMINAIRE TYPE C CHANGED TO TYPE A	NOV 98
C	SIGN LUMINAIRE & MOUNTING REVISED	DEC 96
B	LUMINAIRE CHANGED & J.B. ADDED	AUG 95

LARGE OVERHEAD PLYWOOD GUIDE SIGN INSTALLATION DETAILS (UP TO 1220 X 2440 SHEET ALUMINUM)


Date Approved

30/09/93 E.L. **(Signature on File)**

Chief Highway Engineer

SPECIFICATION DRAWING No.

SP635–3.3.2

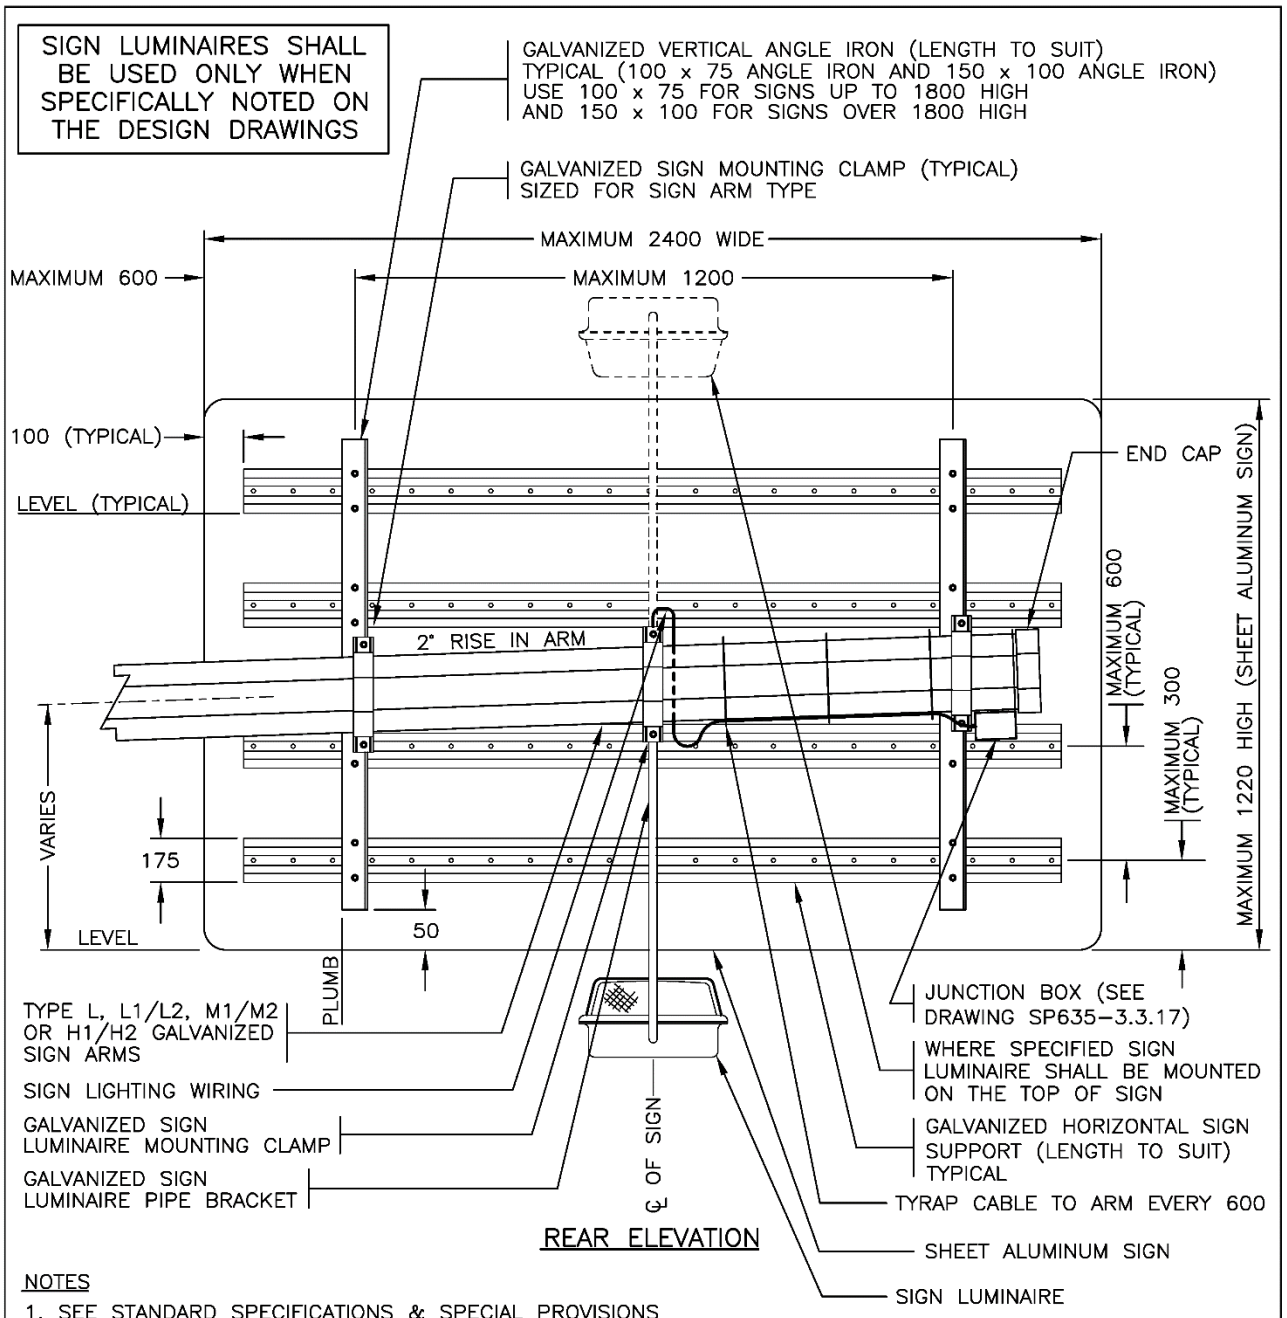

NOTES

1. SEE STANDARD SPECIFICATIONS & SPECIAL PROVISIONS FOR ADDITIONAL INFORMATION.
2. A SKETCH DETAILING THE EXACT SPACING OF VERTICAL ANGLE IRONS AND HORIZONTAL SIGN SUPPORTS WILL BE SUPPLIED WITH SIGN BRACKET ASSEMBLY.
3. NUMBER OF SIGN LUMINAIRES MAY VARY.
4. SIGN LUMINAIRE, PIPE CLAMP AND CABLE ARE NOT REQUIRED FOR NON-ILLUMINATED SIGN.
5. ALL DIMENSIONS ARE IN MILLIMETRES UNLESS OTHERWISE NOTED.

NOT TO SCALE

Ministry of Transportation and Infrastructure

No.	Revision	Date
H	GENERAL REVISIONS	APR 20
G	SHEET ALUMINUM SIGN ADDED	APR 05
F	JUNCTION BOX ON SIGNAL ARM RELOCATED	NOV 01
E	SIGN LUMINAIRE NOTE ADDED	SEPT 00
D	J.B. DRAWING REFERENCE REVISED	DEC 98
C	SIGN LUMINAIRE CLAMP REVISED	DEC 96

LARGE OVERHEAD SHEET ALUMINUM GUIDE SIGN INSTALLATION DETAILS (UP TO 2400 WIDE SIGNS)


Date Approved

30/09/93 E.L. (Signature on File)

Chief Highway Engineer

SPECIFICATION DRAWING No.

SP635-3.3.3

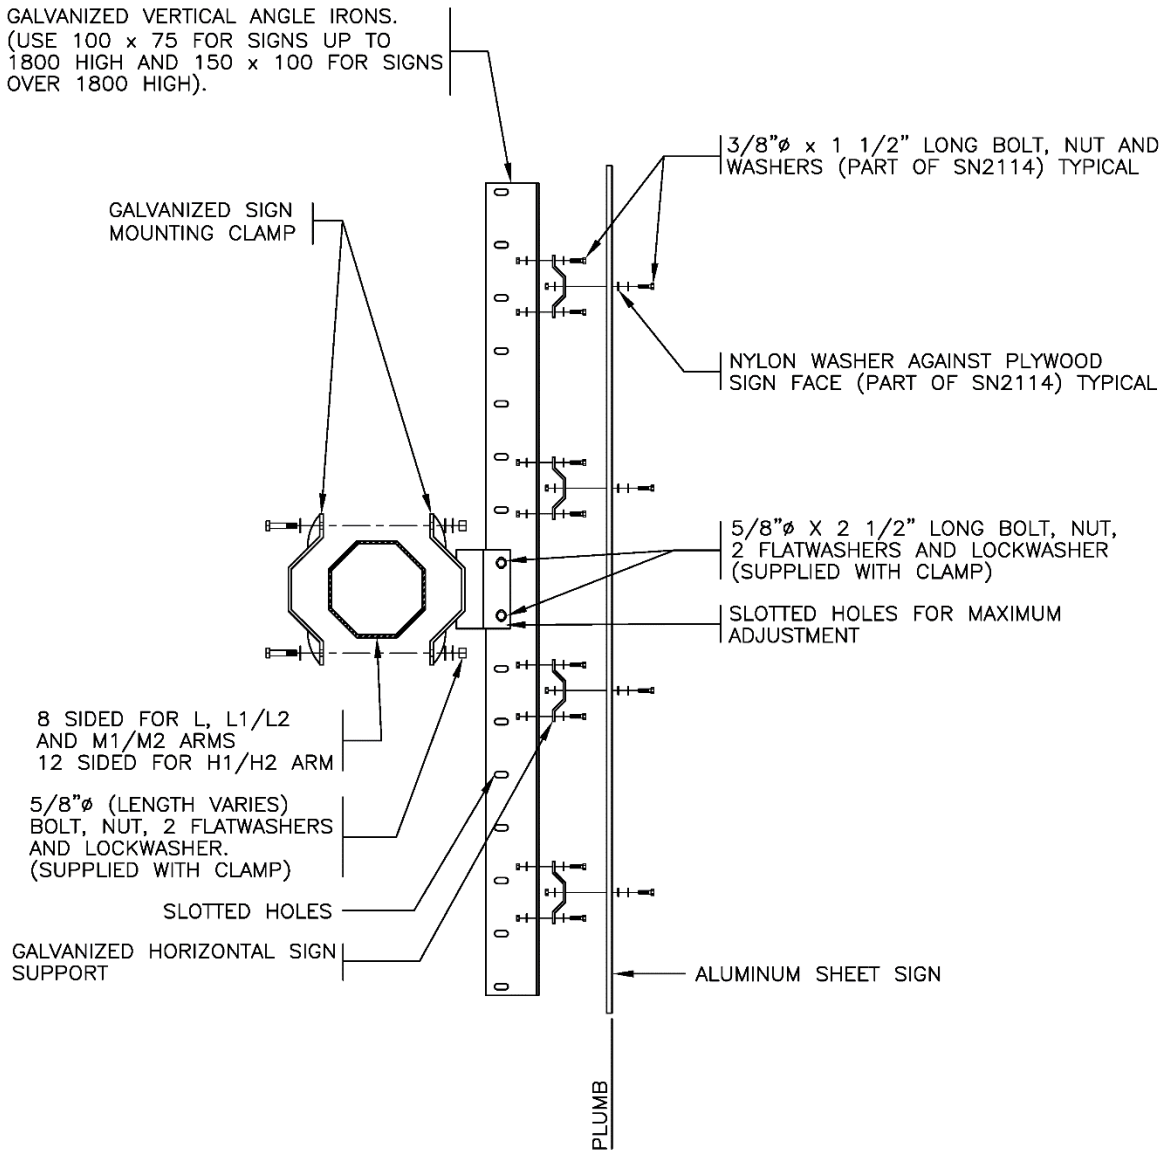

SIGN BRACKET ASSEMBLY
SIDE VIEW

NOTES

1. SEE STANDARD SPECIFICATIONS & SPECIAL PROVISIONS FOR ADDITIONAL INFORMATION.
2. ALL DIMENSIONS ARE IN MILLIMETRES UNLESS OTHERWISE NOTED.

NOT TO SCALE

BRITISH COLUMBIA Ministry of Transportation and Infrastructure

No.	Revision	Date
F		
E		
D	GENERAL REVISION	APR 20
C	SIGN MOUNTING CLAMPS REVISED	DEC 96
B	L1/L2 ARMS ADDED & CLAMP REVISED	AUG 95
A	GENERAL REVISION	AUG 94

LARGE OVERHEAD SHEET ALUMINUM GUIDE SIGN ASSEMBLY DETAILS


Date Approved

30/09/93 E.L. (Signature on File)

Chief Highway Engineer

SPECIFICATION DRAWING No.

SP635–3.3.4

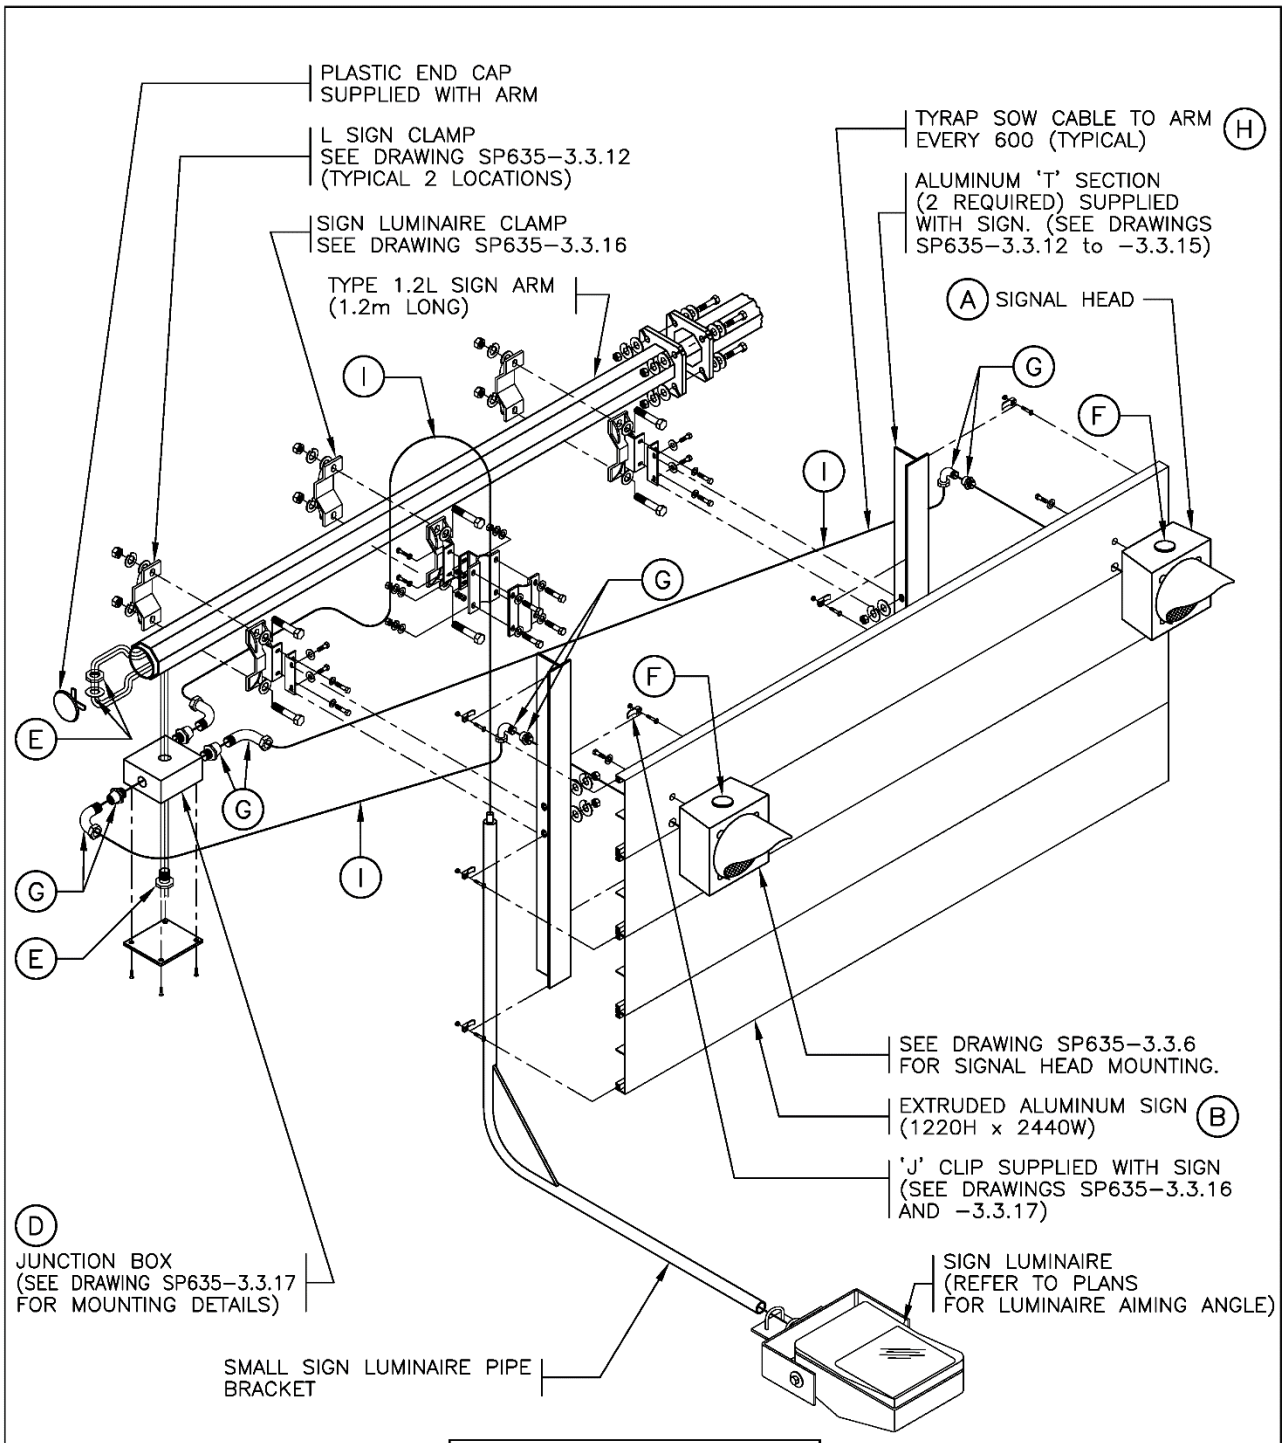

SEE DRAWING SP635–3.3.6 FOR NOTES AND ADDITIONAL DETAILS

SIGN LUMINAIRES SHALL BE USED ONLY WHEN SPECIFICALLY NOTED ON THE DESIGN DRAWINGS

BRITISH COLUMBIA Ministry of Transportation and Infrastructure

NOT TO SCALE

No.	Revision	Date
F		
E	GENERAL REVISION	APR 20
D	JUNCTION BOX MOUNTING REVISED	NOV 01
C	SIGN LUMINAIRE TYPE C CHANGED TO TYPE A	NOV 98
B	SIGN ARM REDRAWN	OCT 97
A	MOUNTING CLAMPS REVISED	AUG 96

LARGE OVERHEAD EXTRUDED ALUMINUM ADVANCE WARNING SIGN ASSEMBLY DETAILS


Date Approved

15/11/95 M.C. (Signature on File)


Chief Highway Engineer

SPECIFICATION DRAWING No.

SP635–3.3.5

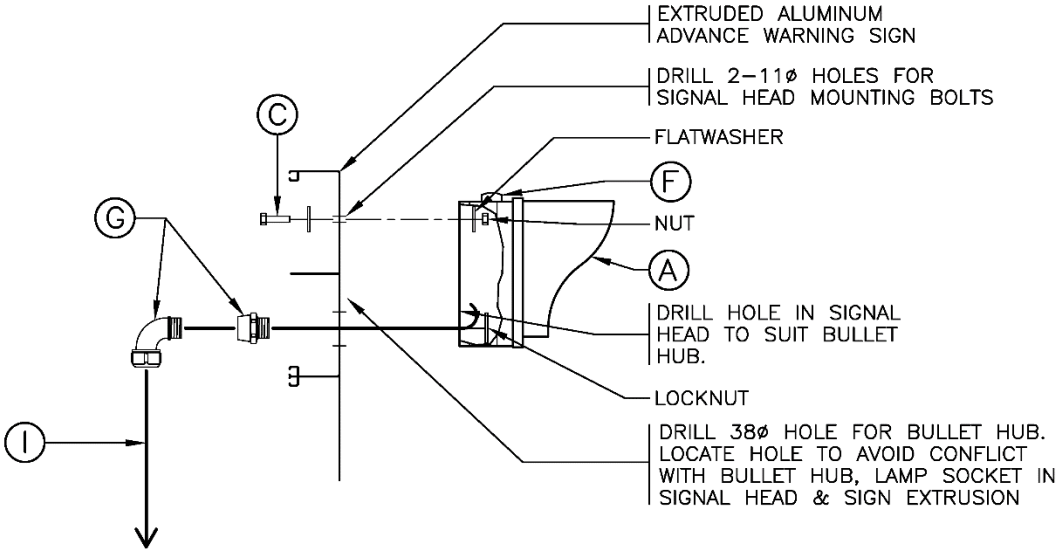

SIGNAL HEAD MOUNTING DETAIL

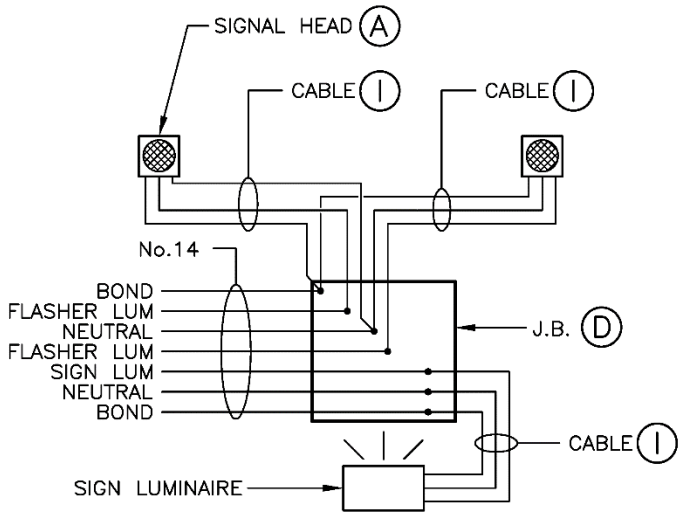

WIRING DIAGRAM

SIGN LUMINAIRES SHALL BE USED ONLY WHEN SPECIFICALLY NOTED ON THE DESIGN DRAWINGS

NOTES

1. SEE STANDARD SPECIFICATIONS & SPECIAL PROVISIONS FOR ADDITIONAL INFORMATION.
2. SEE DRAWINGS SP635–3.3.7 & –3.3.8 FOR PARTS LISTS.
3. ALL DIMENSIONS ARE IN MILLIMETRES UNLESS OTHERWISE NOTED.

NOT TO SCALE

BRITISH COLUMBIA Ministry of Transportation and Infrastructure

No.	Revision	Date
F		
E		
D		
C	GENERAL REVISION	APR 20
B	SIGN CHANGED TO ALUMINUM EXTRUDED	AUG 95
A	GENERAL REVISION	AUG 94

LARGE OVERHEAD EXTRUDED ALUMINUM ADVANCE WARNING SIGN INSTALLATION DETAILS


Date Approved

30/09/93 E.L. (Signature on File)

Chief Highway Engineer

SPECIFICATION DRAWING No.

SP635–3.3.6

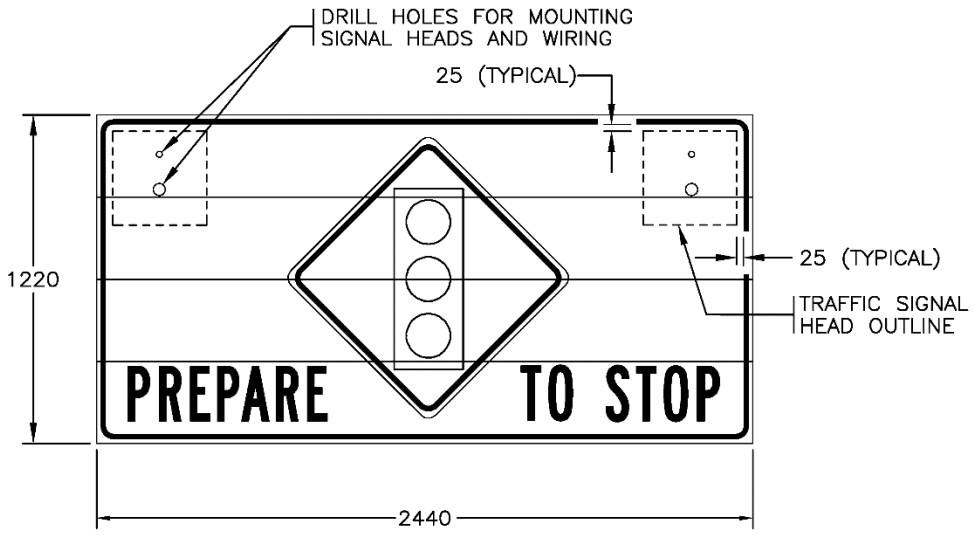

TRAFFIC SIGNAL ADVANCE WARNING SIGN

TRAFFIC SIGNAL ADVANCE WARNING SIGN KIT		
ITEM	QUANTITY	DESCRIPTION
A	2	300mm SIGNAL HEAD SECTION C/W YELLOW LENS, LAMP AND COWL VISOR
B	1	TRAFFIC SIGNAL EXTRUDED ALUMINUM ADVANCE WARNING SIGN BOARD
C	2	3/8"ø x 1 1/2" LONG STAINLESS STEEL HEX HEAD BOLT, NUT, 2 FLAT WASHERS AND 1 LOCKWASHER
D	1	150 x 150 x 100 PVC J.B.
E	1	3/4" INSULATED CHASE NIPPLE, LOCKNUT AND FLAT WASHER
F	2	FINIAL
G	4	1/2" BULLET HUB AND 90° STRAIN RELIEF CONNECTOR AND LOCKNUT
H	5	LARGE TY-RAP
I	7m	3C No. 14 S.O.W. CABLE

SEE DRAWING SP635-3.3.6 FOR NOTES

NOT TO SCALE

BRITISH COLUMBIA Ministry of Transportation and Infrastructure

No.	Revision	Date
F		
E		
D	GENERAL REVISIONS	APR 20
C	ITEM E REVISED	NOV 01
B	SIGN CHANGED TO ALUMINUM EXTRUDED	AUG 95
A	GENERAL REVISIONS	AUG 94

LARGE OVERHEAD EXTRUDED ALUMINUM TRAFFIC SIGNAL ADVANCE WARNING SIGN INSTALLATION DETAILS


Date Approved

30/09/93 E.L. (Signature on File)

Chief Highway Engineer

SPECIFICATION DRAWING No.

SP635-3.3.7

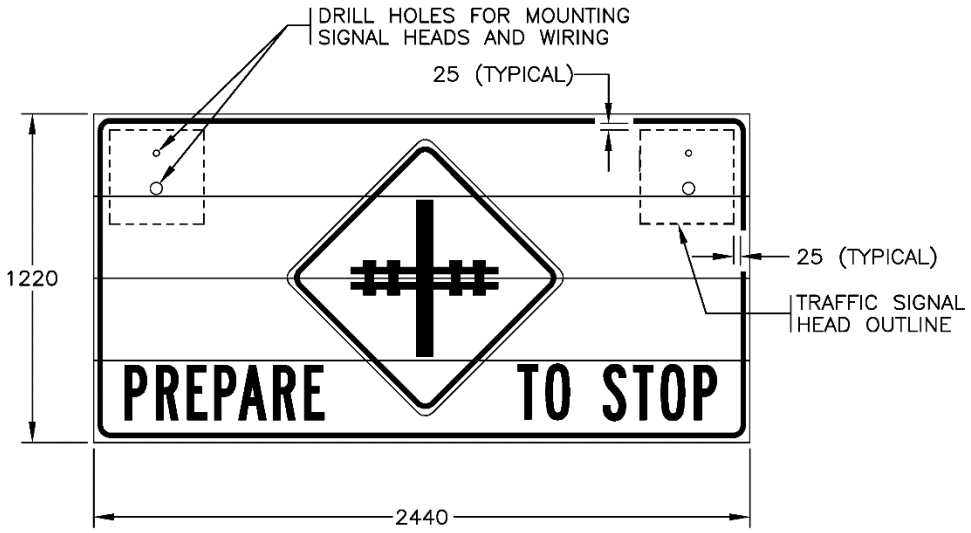

RAILWAY ADVANCE WARNING SIGN

TRAFFIC SIGNAL ADVANCE WARNING SIGN KIT		
ITEM	QUANTITY	DESCRIPTION
A	2	300mm SIGNAL HEAD SECTION C/W YELLOW LENS, LAMP AND COWL VISOR
B	1	EXTRUDED ALUMINUM RAILWAY ADVANCE WARNING SIGN BOARD
C	2	3/8"ø x 1 1/2" LONG STAINLESS STEEL HEX HEAD BOLT, NUT, 2 FLAT WASHERS AND 1 LOCKWASHER
D	1	150 x 150 x 100 PVC J.B.
E	1	3/4" INSULATED CHASE NIPPLE, 2 LOCKNUTS AND 2 FLAT WASHERS
F	2	FINIAL
G	4	1/2" BULLET HUB AND 90° STRAIN RELIEF CONNECTOR AND LOCKNUT
H	5	LARGE TY-RAP
I	7m	3C No. 14 S.O.W. CABLE

SEE DRAWING SP635-3.3.6 FOR NOTES

NOT TO SCALE


BRITISH COLUMBIA | Ministry of Transportation and Infrastructure

No.	Revision	Date
F		
E		
D		
C	GENERAL REVISIONS	APR 20
B	SIGN CHANGED TO ALUMINUM EXTRUDED	AUG 95
A	GENERAL REVISIONS	AUG 94

LARGE OVERHEAD EXTRUDED ALUMINUM RAILWAY ADVANCE WARNING SIGN INSTALLATION DETAILS

Date 18/11/94 Approved E.L. (Signature on File) Chief Highway Engineer

SPECIFICATION DRAWING No. SP635-3.3.8

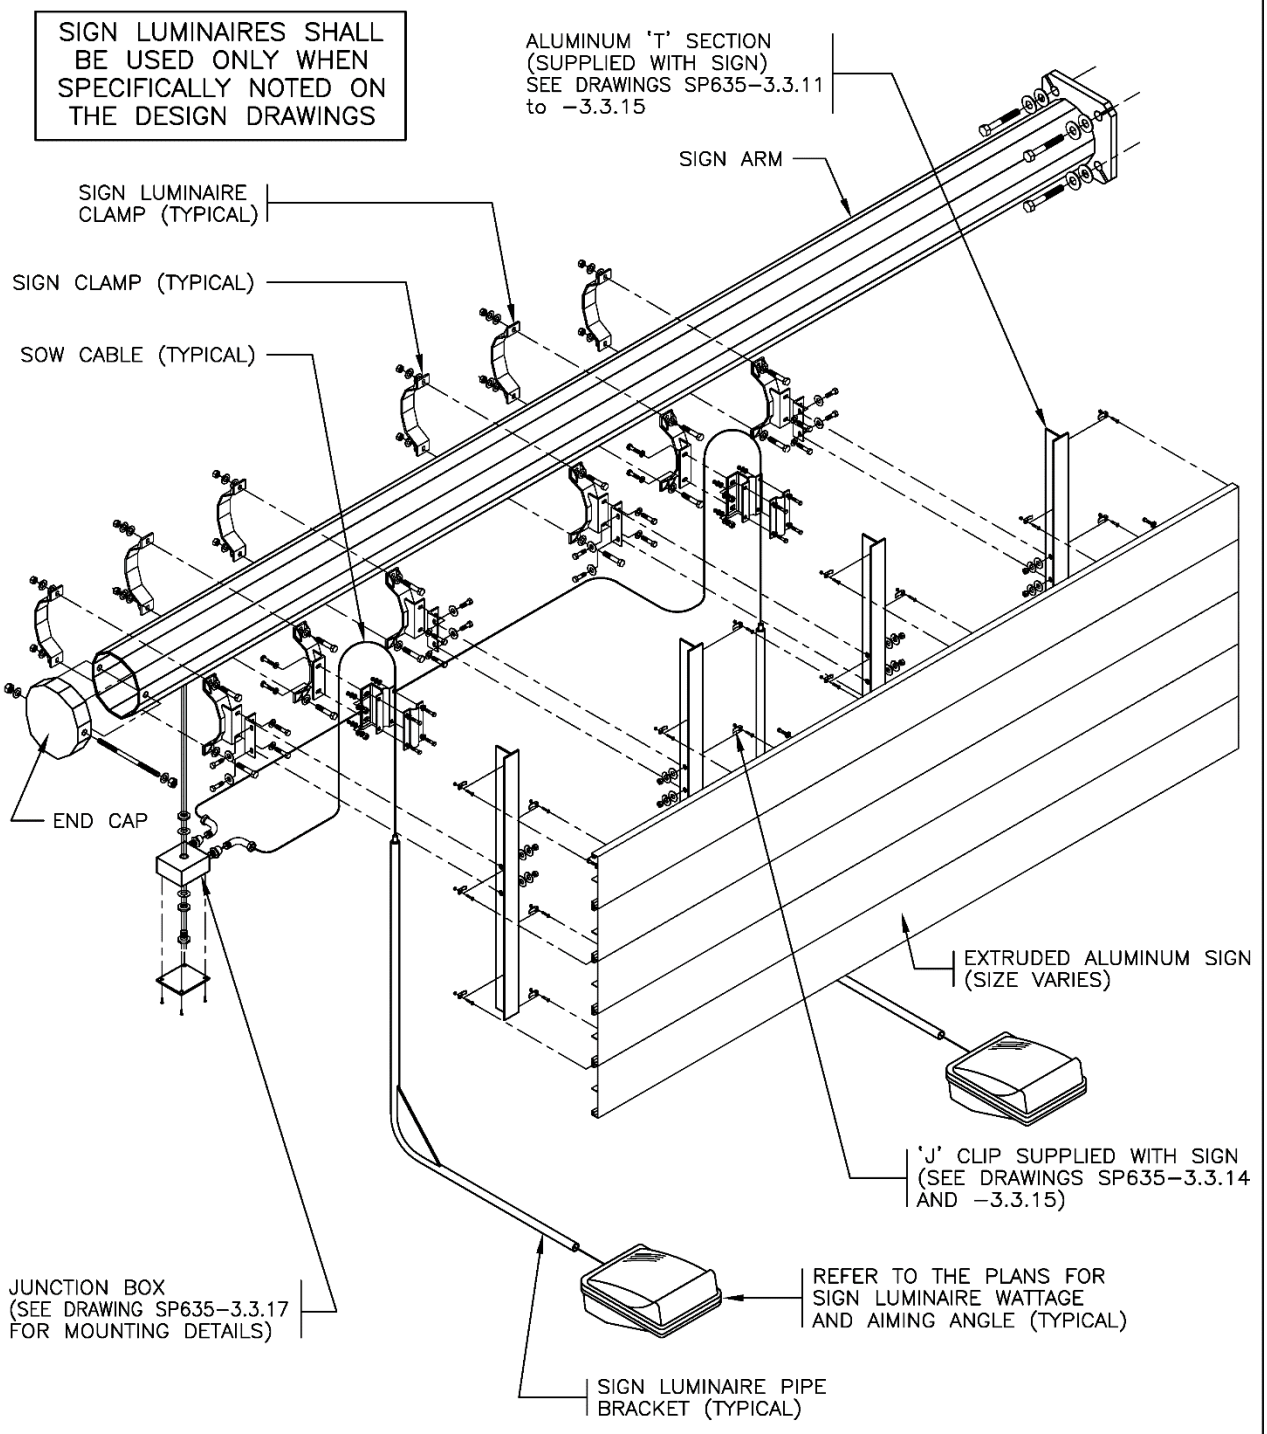

No.	Revision	Date
F		
E		
D	GENERAL REVISION	APR 20
C	SIGN LUMINAIRE NOTE ADDED	SEPT 00
B	SIGN LUMINAIRE TYPE B NOTE DELETED	NOV 98
A	MOUNTING CLAMPS REVISED	AUG 96

LARGE OVERHEAD EXTRUDED ALUMINUM GUIDE SIGN ASSEMBLY DETAILS


Date Approved

15/11/95 M.C. (Signature on File)

Chief Highway Engineer

SPECIFICATION DRAWING No.

SP635-3.3.9

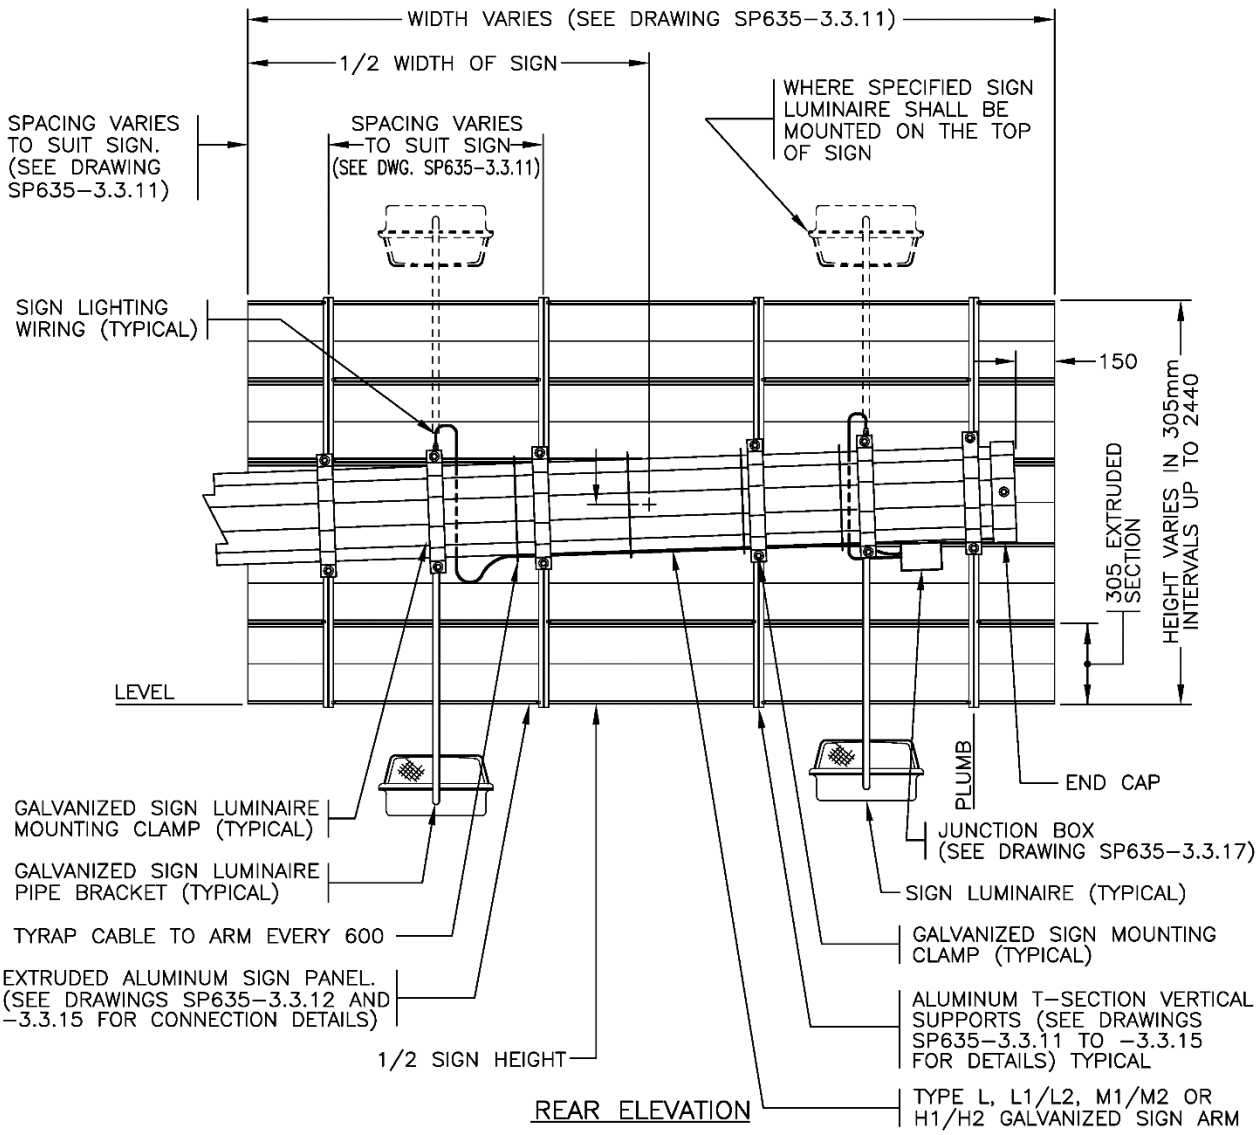

TOTAL MASS
EACH EXTRUDED ALUMINUM SIGN SECTION = 4 kg/m

SIGN LUMINAIRES SHALL BE USED ONLY WHEN SPECIFICALLY NOTED ON THE DESIGN DRAWINGS

NOTES

1. SEE STANDARD SPECIFICATIONS & SPECIAL PROVISIONS FOR ADDITIONAL INFORMATION.
2. NUMBER OF SIGN LUMINAIRES MAY VARY.
3. FUSE SIGN LUMINAIRES IN POLE HANDHOLE.
4. SIGN LUMINAIRE, MOUNTING PIPE, CLAMP AND CABLE IS NOT REQUIRED FOR NON–ILLUMINATED SIGN.
5. ALL DIMENSIONS ARE IN MILLIMETRES UNLESS OTHERWISE NOTED.

NOT TO SCALE










BRITISH COLUMBIA Ministry of Transportation and Infrastructure

No.	Revision	Date
F		
E	GENERAL REVISION	APR 20
D	SIGN LUMINAIRE NOTE ADDED	SEPT 00
C	J.B. DRAWING REFERENCE REVISED	DEC 98
B	SIGN LUMINAIRE CLAMPS REVISED	DEC 96
A	L1/L2 ARMS & JUNCTION BOX ADDED	AUG 95

LARGE OVERHEAD EXTRUDED ALUMINUM GUIDE SIGN INSTALLATION DETAILS

Date: **21/11/94** Approved: **E.L.** **(Signature on File)**
Chief Highway Engineer

SPECIFICATION DRAWING No.
SP635–3.3.10

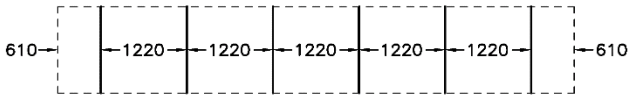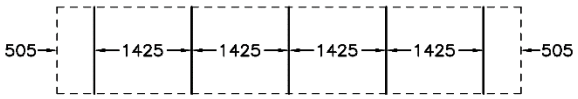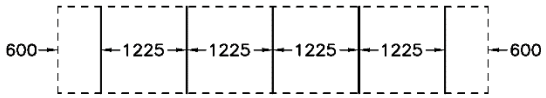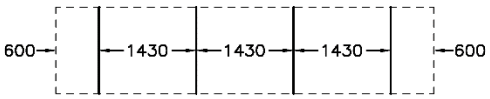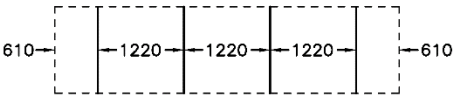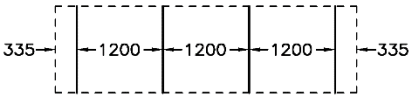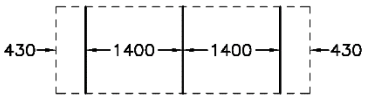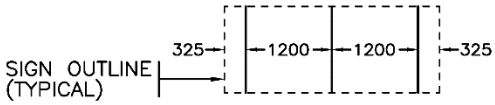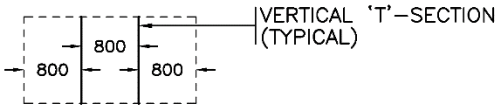TYPICAL SIGN WIDTH	SPACING OF VERTICAL T–SECTIONS	NUMBER OF VERTICALS
7320mm		6
6710mm		5
6100mm		5
5490mm		4
4880mm		4
4270mm		4
3660mm		3
3050mm		3
2440mm		2

SEE DRAWING SP635–3.3.10 FOR NOTES AND ADDITIONAL DETAILS

NOT TO SCALE

BRITISH COLUMBIA Ministry of Transportation and Infrastructure

No.	Revision	Date
F		
E		
D		
C	GENERAL REVISION	APR 20
B	T–SECTION SPACING FOR 2440 WIDE SIGN REVISED	AUG 96
A	SIGN WDTHS & T–SECTION SPACING REVISED	AUG 95

LARGE OVERHEAD EXTRUDED ALUMINUM GUIDE SIGN INSTALLATION DETAILS

Date 18/11/94 Approved E.L. (Signature on File) Chief Highway Engineer

SPECIFICATION DRAWING No. SP635–3.3.11