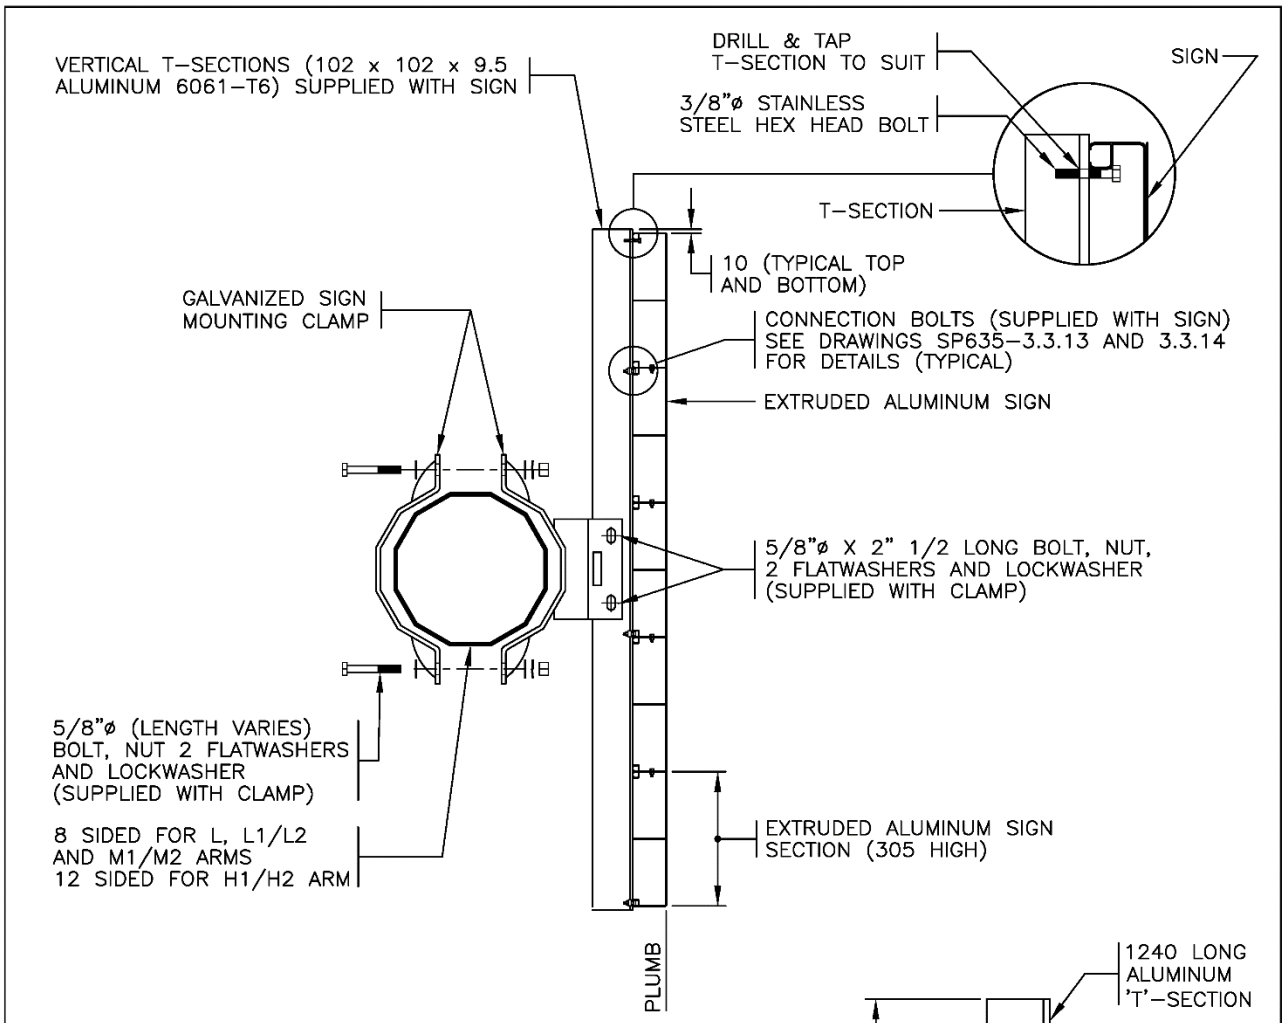



BRITISH COLUMBIA — Ministry of Transportation and Infrastructure

No.	Revision	Date
F		
E		
D	GENERAL REVISION	APR 20
C	'T'–SECTION SLOT DETAIL ADDED	NOV 01
B	MOUNTING CLAMPS REV'D & SAFETY BOLT ADDED	AUG 96
A	L1/L2 ARMS ADDED & T–SECTION DETAILS REVISED	AUG 95

LARGE OVERHEAD EXTRUDED ALUMINUM GUIDE SIGN ASSEMBLY DETAILS

Date: **18/11/94** Approved: **E.L.** (Signature on File)
Chief Highway Engineer

SPECIFICATION DRAWING No.
SP635–3.3.12

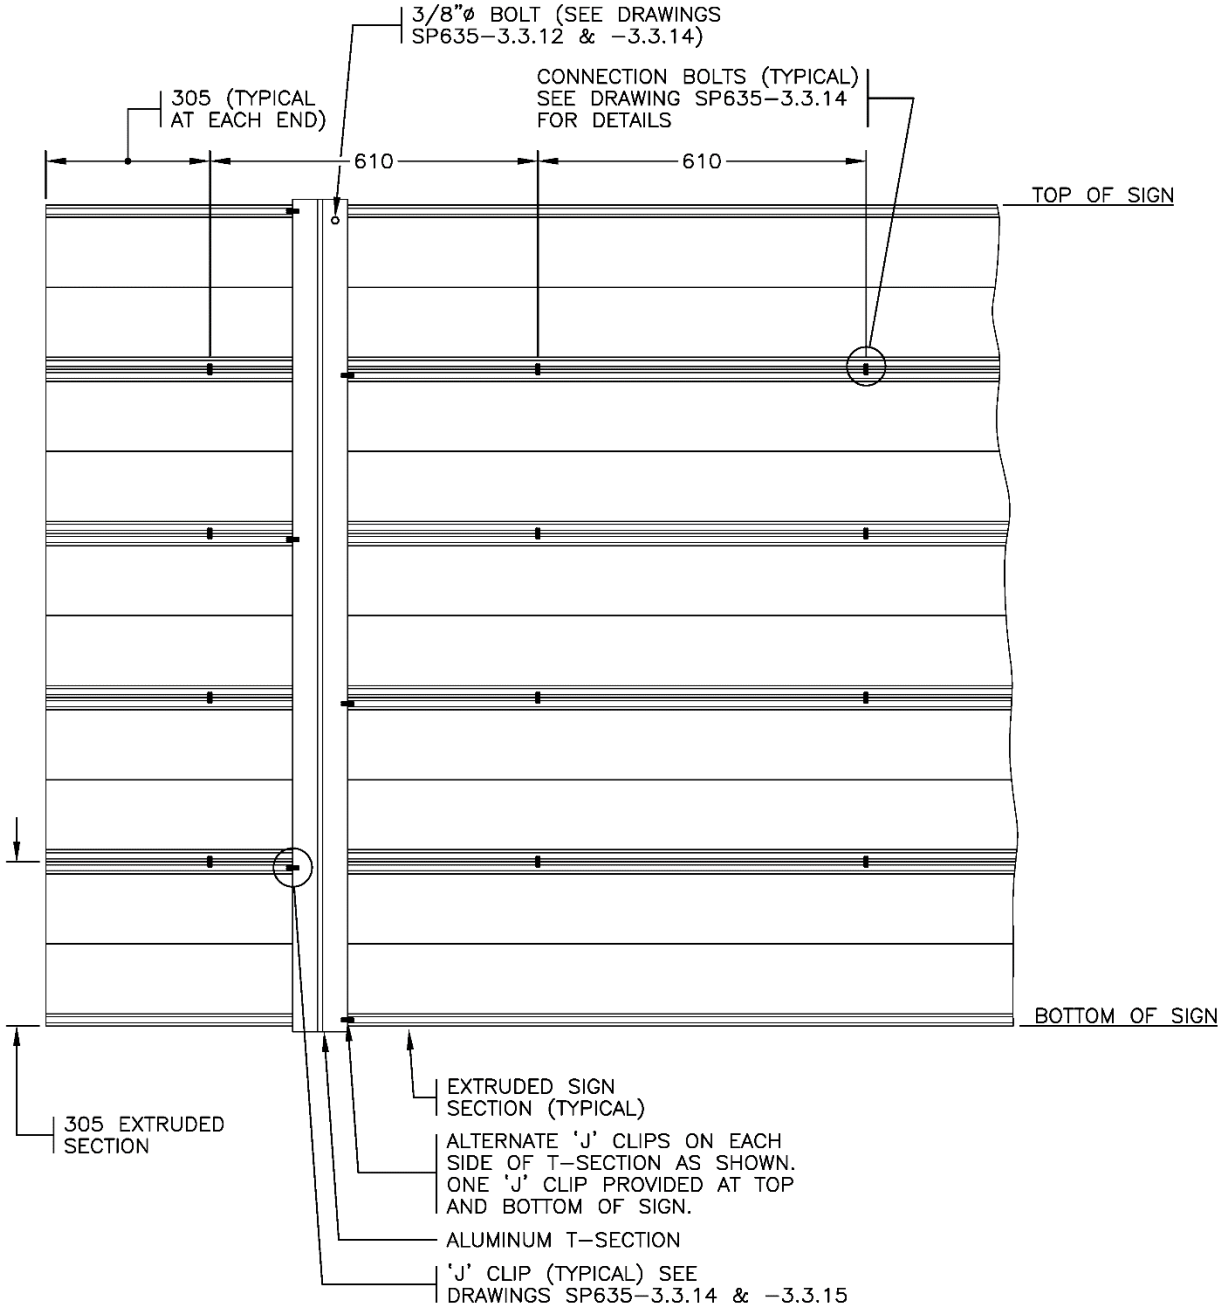

REAR VIEW OF SIGN

SEE DRAWING SP635–3.3.10 FOR NOTES AND ADDITIONAL DETAILS.

NOT TO SCALE

BRITISH COLUMBIA | Ministry of Transportation and Infrastructure

No.	Revision	Date
F		
E		
D		
C	GENERAL REVISION	APR 20
B	SAFETY BOLT ADDED	AUG 96
A	END HOLE SPACING REVISED	AUG 95

LARGE OVERHEAD EXTRUDED ALUMINUM GUIDE SIGN ASSEMBLY DETAILS


Date Approved

18/11/94 E.L. (Signature on File)

Chief Highway Engineer

SPECIFICATION DRAWING No.

SP635–3.3.13

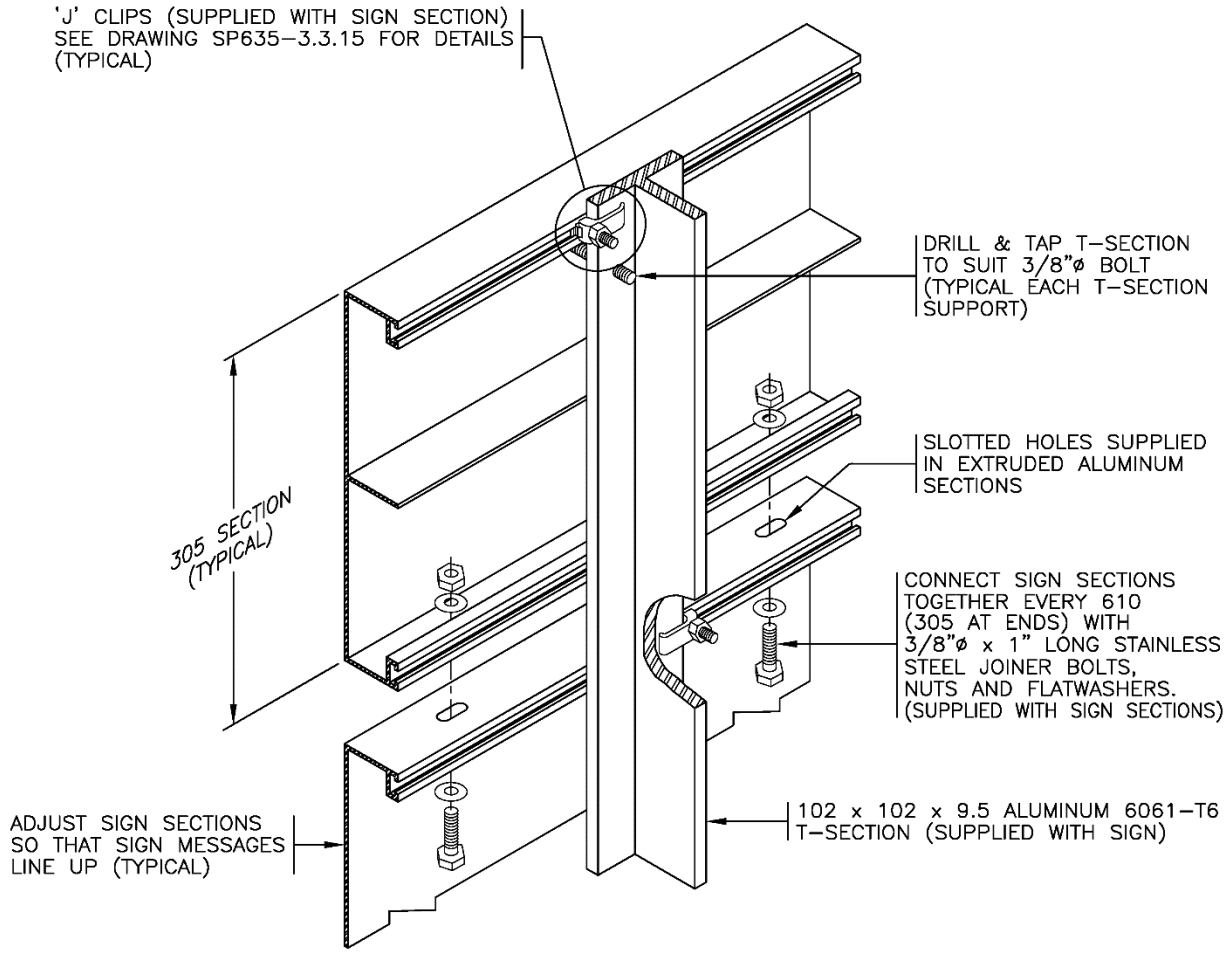

ASSEMBLY VIEW

TORQUE JOINER BOLTS AND 'J' CLIPS TO 19 ft. lbs.

SEE DRAWING SP635-3.3.10 FOR NOTES AND ADDITIONAL DETAILS.

NOT TO SCALE

BRITISH COLUMBIA | Ministry of Transportation and Infrastructure

No.	Revision	Date
F		
E		
D		
C	GENERAL REVISIONS	APR 20
B	SAFETY BOLT ADDED	AUG 96
A	END HOLE SPACING REVISED	AUG 95

LARGE OVERHEAD EXTRUDED ALUMINUM GUIDE SIGN ASSEMBLY DETAILS


Date Approved

18/11/94 E.L. (Signature on File)

Chief Highway Engineer

SPECIFICATION DRAWING No.

SP635-3.3.14

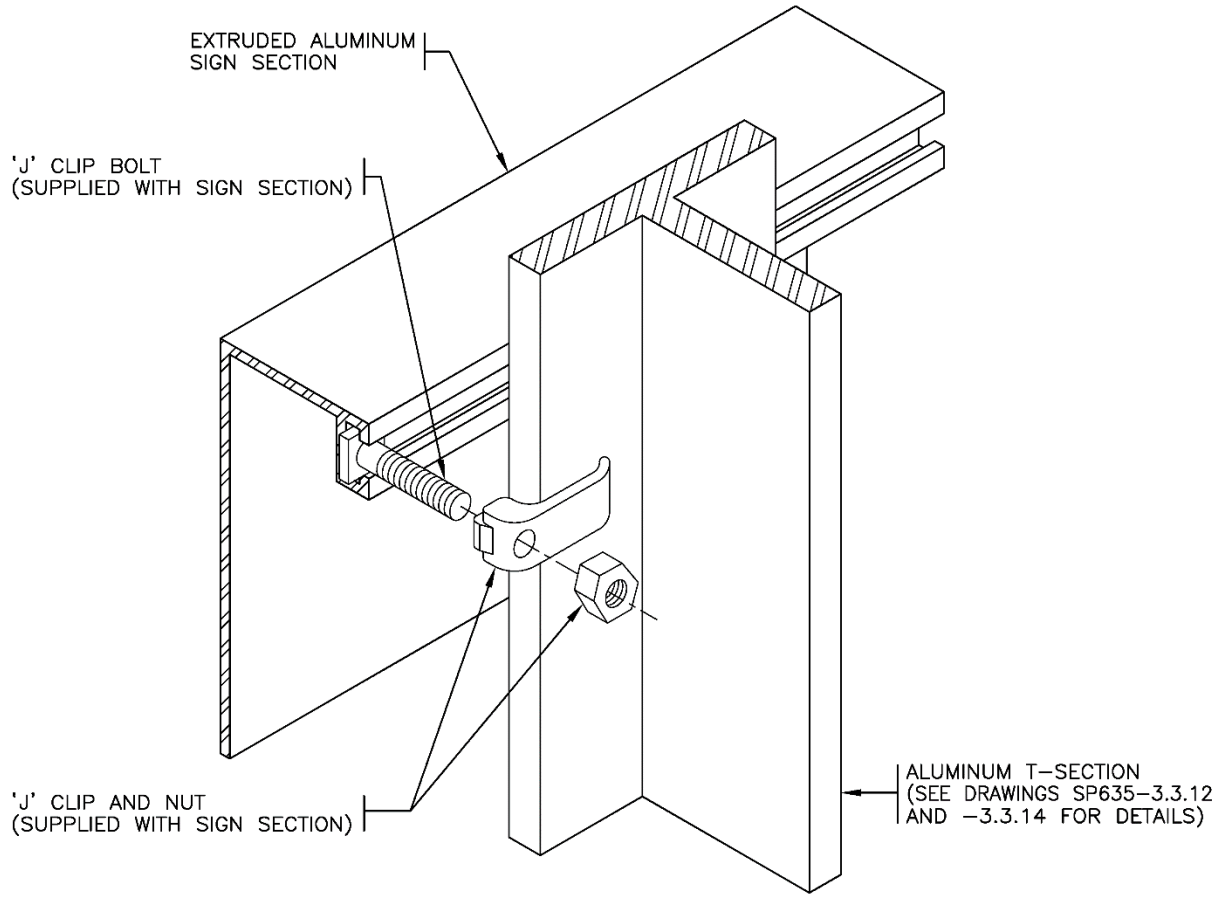

ASSEMBLY VIEW

TORQUE JOINER BOLTS AND 'J' CLIPS TO 19 ft. lbs.

SEE DRAWING SP635–3.3.10 FOR NOTES AND ADDITIONAL DETAILS.

NOT TO SCALE

BRITISH COLUMBIA Ministry of Transportation and Infrastructure

No.	Revision	Date
F		
E		
D		
C		
B	GENERAL REVISIONS	APR 20
A	DRAWING NUMBER REVISED	AUG 95

LARGE OVERHEAD EXTRUDED ALUMINUM GUIDE SIGN ASSEMBLY DETAILS


Date Approved

18/11/94 E.L. (Signature on File)

Chief Highway Engineer

SPECIFICATION DRAWING No.

SP635–3.3.15

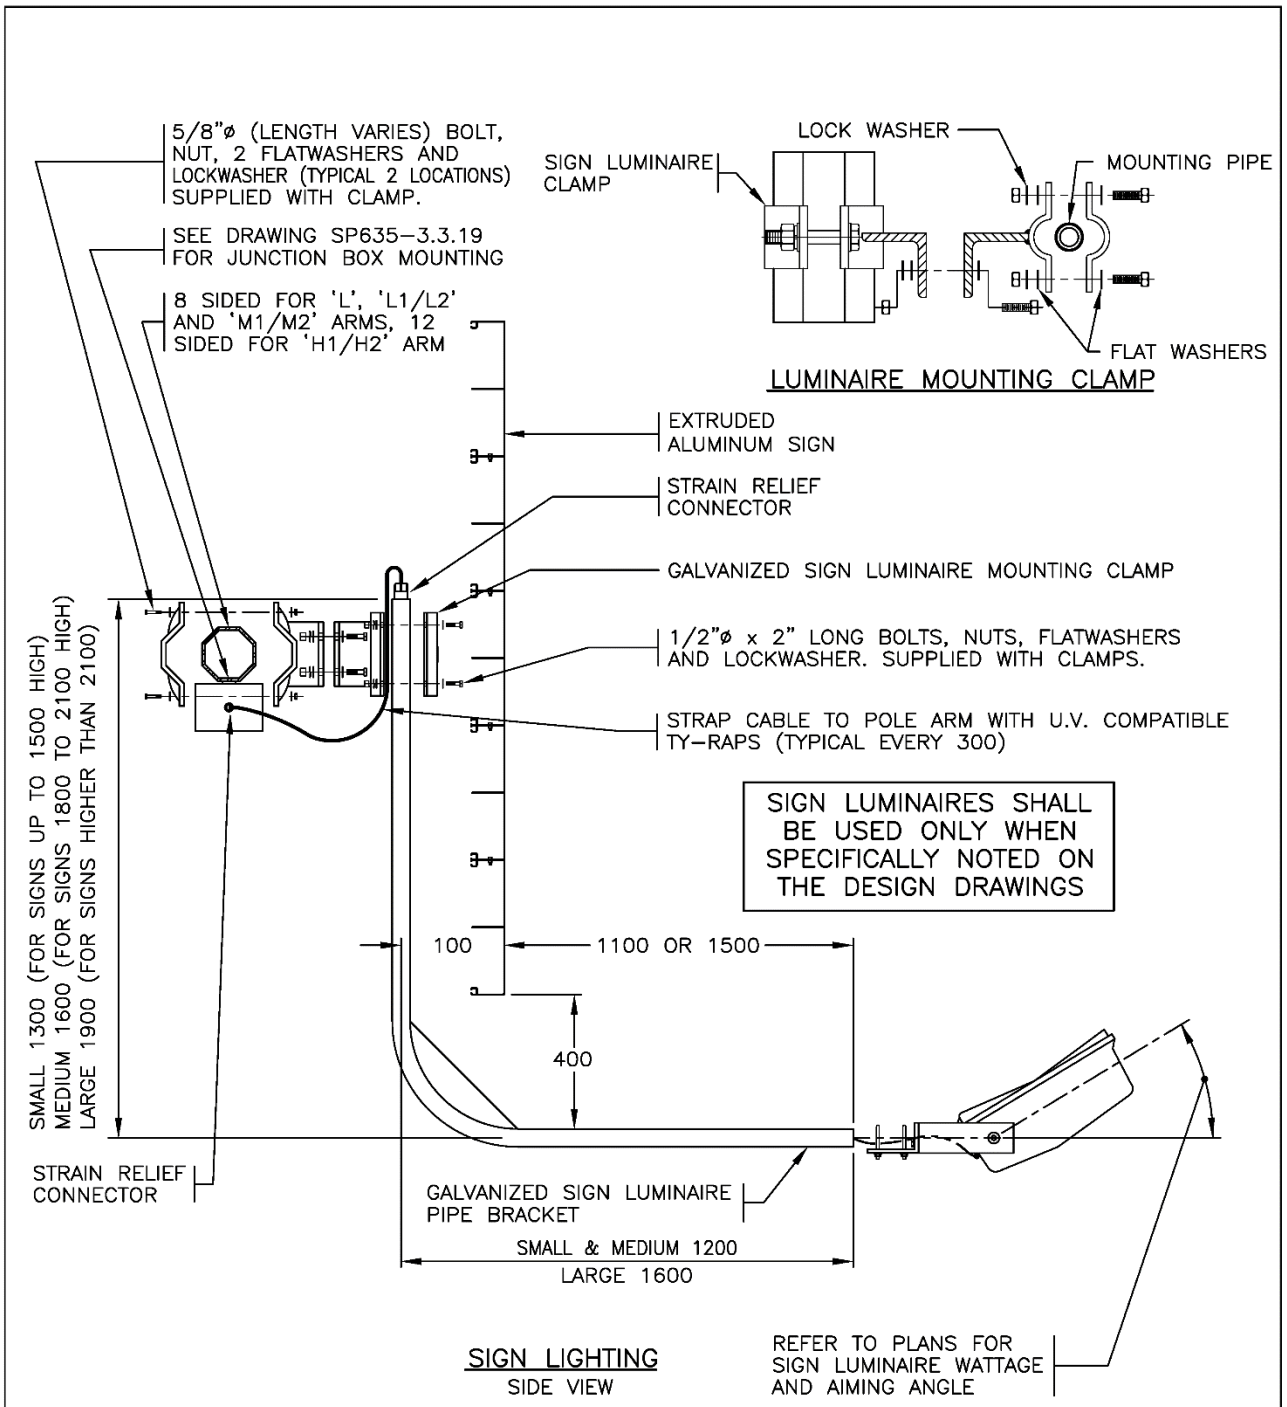

SIGN LIGHTING
SIDE VIEW

NOTES

1. SEE STANDARD SPECIFICATIONS & SPECIAL PROVISIONS FOR ADDITIONAL INFORMATION.
2. ALL DIMENSIONS ARE IN MILLIMETRES UNLESS OTHERWISE NOTED.

NOT TO SCALE


BRITISH COLUMBIA Ministry of Transportation and Infrastructure

No.	Revision	Date
G	GENERAL REVISIONS	APR 20
F	JUNCTION BOX MOUNTING REVISED	NOV 01
E	SIGN LUMINAIRE NOTE ADDED	SEPT 00
D	SIGN LUMINAIRE MOUNTING DIMENSIONS CHANGED	NOV 98
C	SIGN LUMINAIRE & MOUNTING REVISED	DEC 96
B	TYPE C LUMINIARE & J.B. ADDED	AUG 95

LARGE OVERHEAD GUIDE SIGN LUMINAIRE INSTALLATION DETAILS

Date Approved
30/09/93 E.L. **(Signature on File)**
Chief Highway Engineer

SPECIFICATION DRAWING No.
SP635-3.3.16

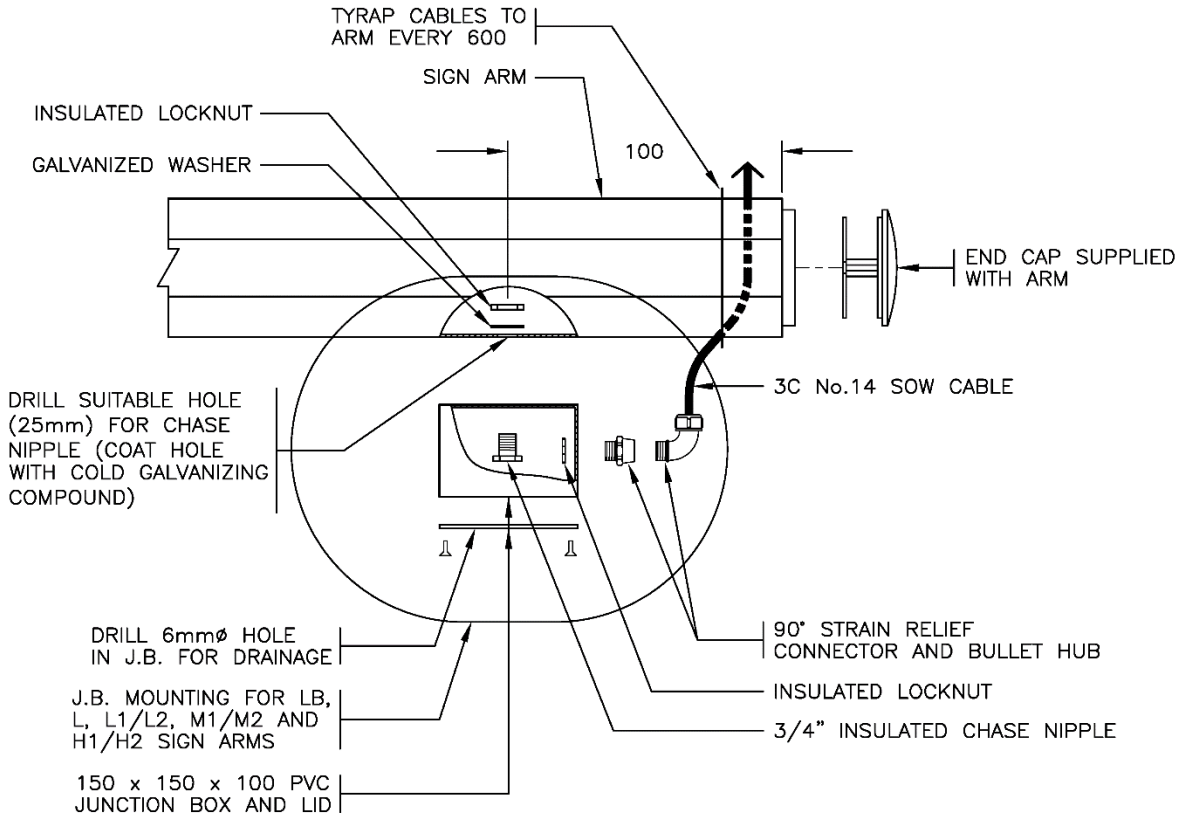

J.B. MOUNTING DETAIL

NOTES

1. SEE STANDARD SPECIFICATIONS & SPECIAL PROVISIONS FOR ADDITIONAL INFORMATION.
2. ALL DIMENSIONS ARE IN MILLIMETRES UNLESS OTHERWISE NOTED.

NOT TO SCALE

BRITISH COLUMBIA Ministry of Transportation and Infrastructure

No.	Revision	Date
F		
E		
D		
C	GENERAL REVISION	APR 20
B	MOUNTING REVISED	NOV 01
A	DRAWING NUMBER REVISED	DEC 98

JUNCTION BOX INSTALLATION DETAILS ON SIGN ARMS


Date Approved

15/11/95 M.C. (Signature on File)

Chief Highway Engineer

SPECIFICATION DRAWING No.

SP635–3.3.17

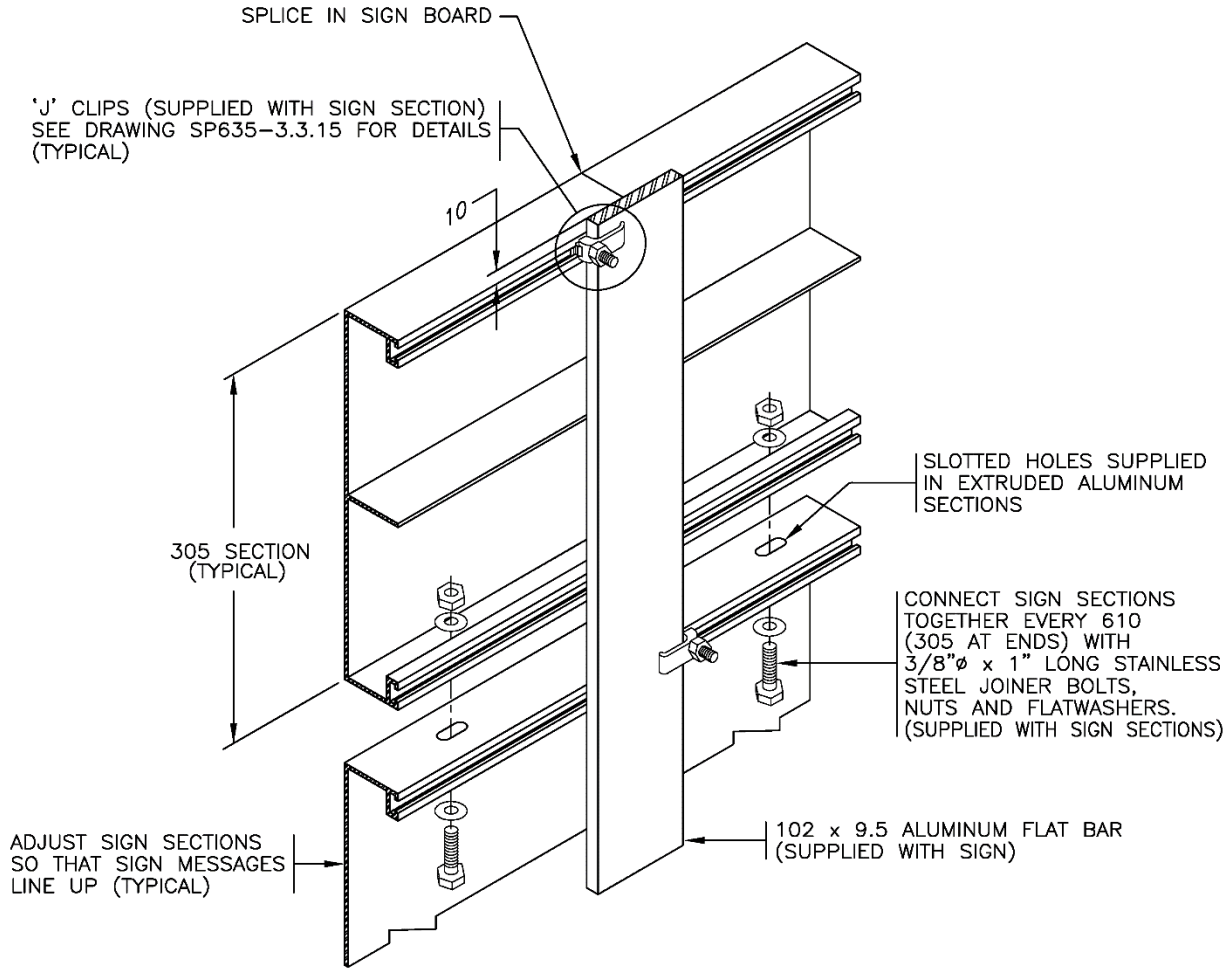

ASSEMBLY VIEW

TORQUE JOINER BOLTS AND 'J' CLIPS TO 19 ft. lbs.

SEE DRAWING SP635-3.3.10 FOR NOTES AND ADDITIONAL DETAILS.

NOT TO SCALE

BRITISH COLUMBIA Ministry of Transportation and Infrastructure

No.	Revision	Date
F		
E		
D		
C		
B	GENERAL REVISION	APR 20
A	DRAWING NUMBER REVISED	DEC 98


LARGE OVERHEAD EXTRUDED ALUMINUM GUIDE SIGN FLAT BAR AT SPLICE DETAILS

Date Approved

Chief Highway Engineer

SPECIFICATION DRAWING No.

SP635-3.3.18

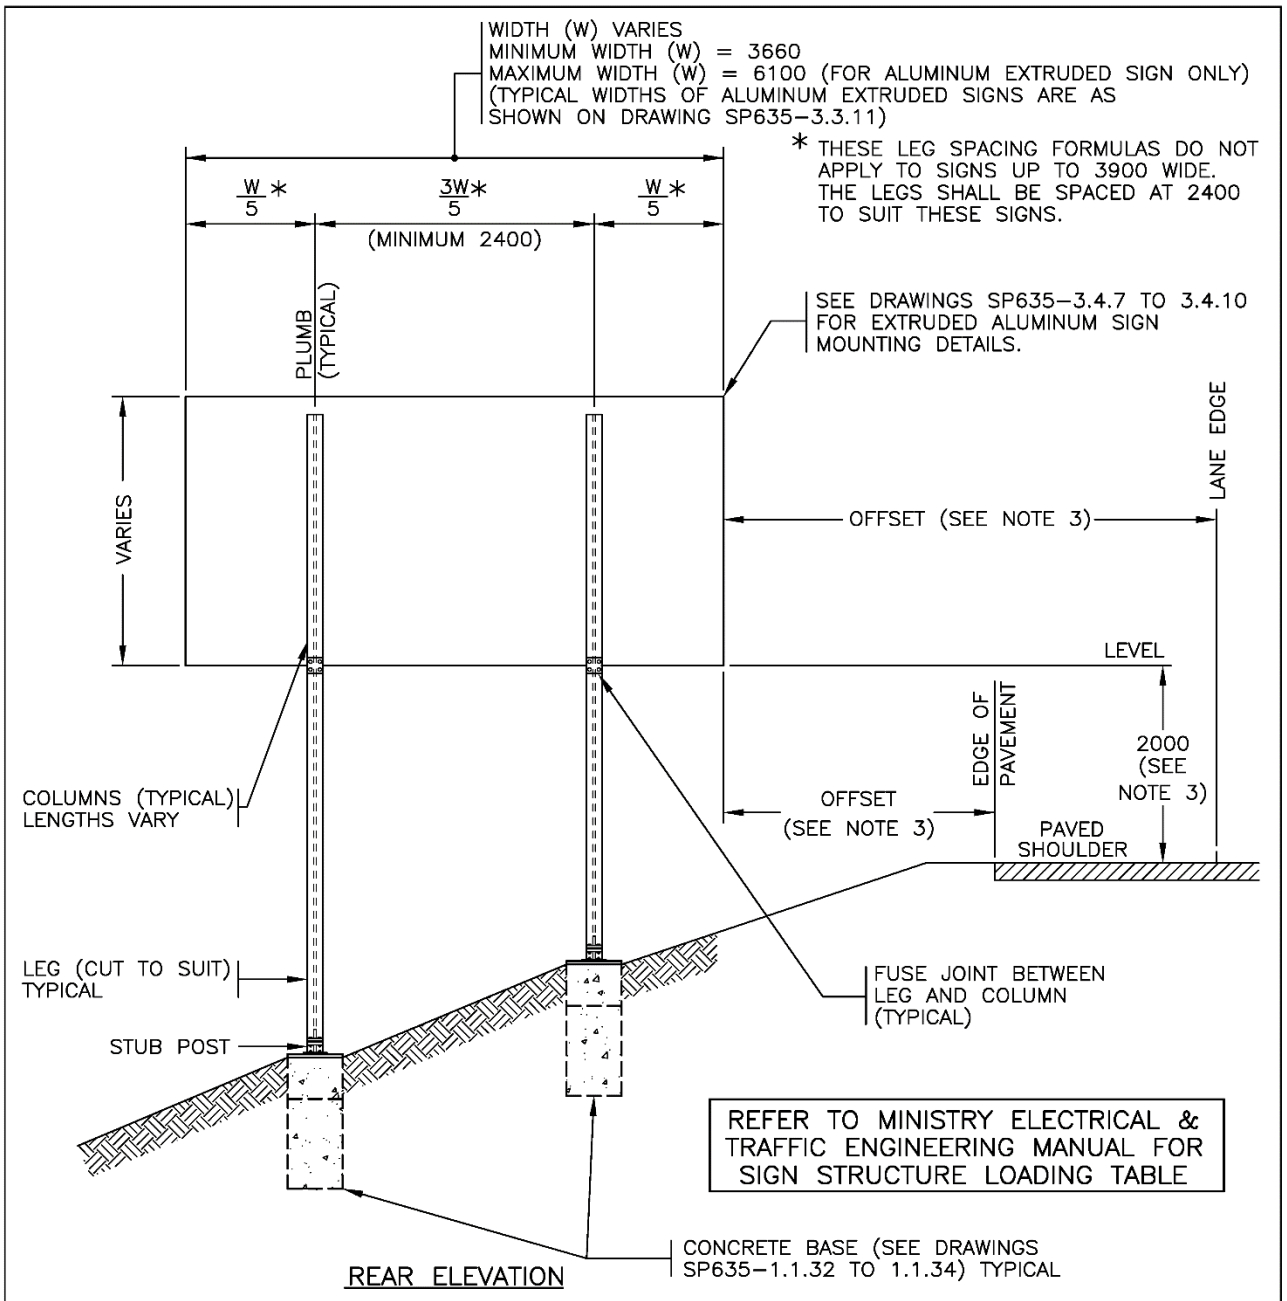

NOTES

1. SEE STANDARD SPECIFICATIONS & SPECIAL PROVISIONS FOR ADDITIONAL INFORMATION.
2. ALL DIMENSIONS ARE IN MILLIMETRES UNLESS OTHERWISE NOTED.
3. MOUNTING HEIGHTS & OFFSETS SHALL FALL WITHIN THE RANGES NOTED IN THE MINISTRY MANUAL OF STANDARD TRAFFIC SIGNS & PAVEMENT MARKINGS.

NOT TO SCALE

BRITISH COLUMBIA | Ministry of Transportation and Infrastructure

No.	Revision	Date
G	REMOVED PLYWOOD SIGN DETAILS	APR 20
F	GENERAL REVISIONS	APR 17
E	GENERAL REVISIONS	APR 05
D	MOUNTING HEIGHTS & OFFSETS REFERED THE MINISTRY MANUAL OF STANDARD TRAFFIC SIGNS	NOV 98
C	SLOPE & BASE DWG. REFERENCES REV'D	AUG 96

TWO LEG BREAKAWAY SIGN STRUCTURE INSTALLATION DETAILS


Date Approved

30/09/93 E.L. (Signature on File)

Chief Highway Engineer

SPECIFICATION DRAWING No.

SP635-3.4.1

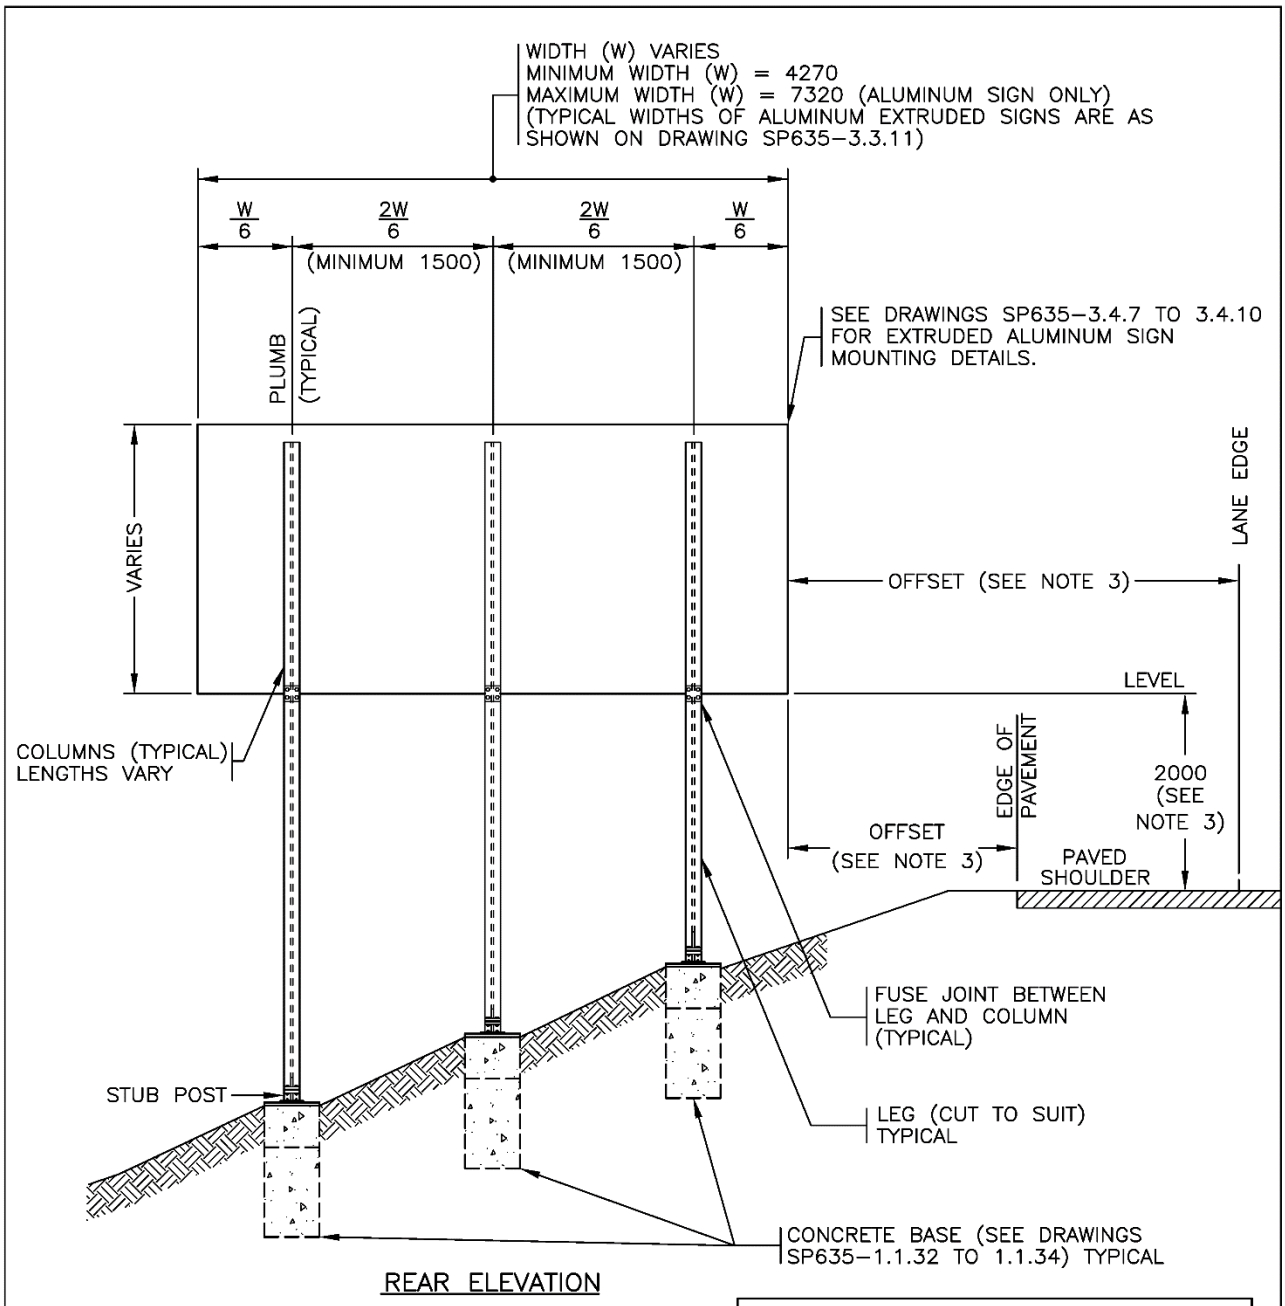

REAR ELEVATION

REFER TO MINISTRY ELECTRICAL & TRAFFIC ENGINEERING MANUAL FOR SIGN STRUCTURE LOADING TABLE

NOTES

1. SEE STANDARD SPECIFICATIONS & SPECIAL PROVISIONS FOR ADDITIONAL INFORMATION.
2. ALL DIMENSIONS ARE IN MILLIMETRES UNLESS OTHERWISE NOTED.
3. MOUNTING HEIGHTS & OFFSETS SHALL FALL WITHIN THE RANGES NOTED IN THE MINISTRY MANUAL OF STANDARD TRAFFIC SIGNS & PAVEMENT MARKINGS.

NOT TO SCALE

BRITISH COLUMBIA — Ministry of Transportation and Infrastructure

No.	Revision	Date
E	REMOVED PLYWOOD SIGN DETAILS	APR 20
E	GENERAL REVISIONS	APR 17
D	MOUNTING HEIGHTS & OFFSETS REFERED THE MINISTRY MANUAL OF STANDARD TRAFFIC SIGNS	NOV 98
C	SLOPE & BASE DWG. REFERENCES REV'D	AUG 96
B	SLOPE SHOWN & TYPICAL SIGN WIDTHS SHOWN	AUG 95

THREE LEG BREAKAWAY SIGN STRUCTURE INSTALLATION DETAILS


Date Approved

30/09/93 E.L. (Signature on File)

Chief Highway Engineer

SPECIFICATION DRAWING No.

SP635-3.4.2

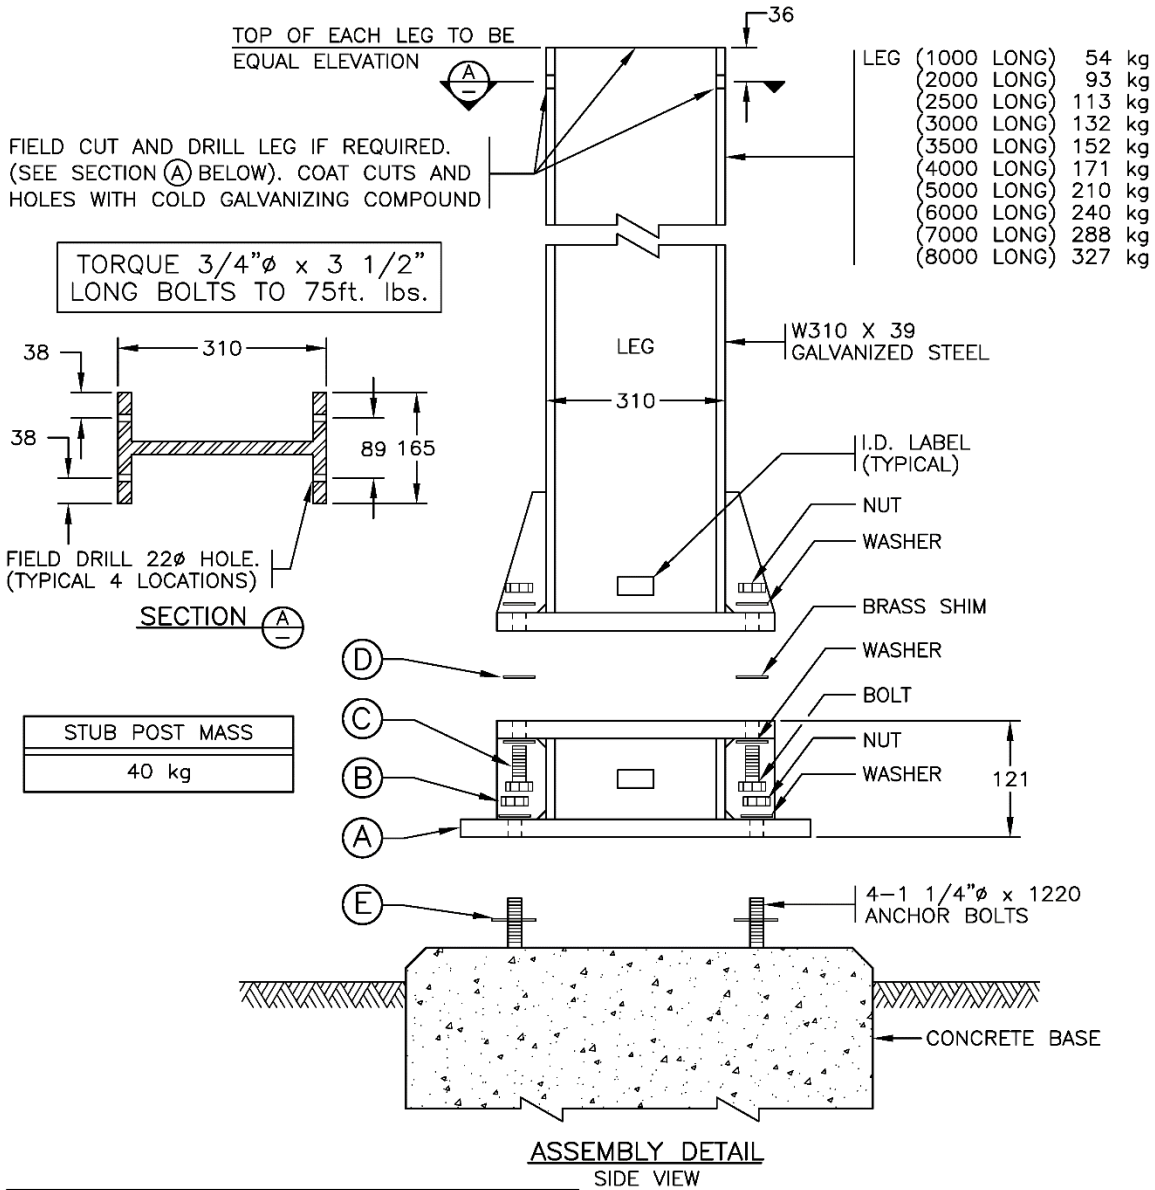

ASSEMBLY DETAIL
SIDE VIEW

STUB POST KIT		
ITEM	QUANTITY	DESCRIPTION
A	1	GALVANIZED STEEL STUB POST
B	4	GALVANIZED NUT AND WASHER FOR 1 1/4"ø ANCHOR BOLT
C	4	3/4"ø x 3 1/2" LONG GALVANIZED BOLT, 2 WASHERS AND NUT
D	4	BRASS SHIMS (1 PER BOLT)
E	4	LEVELING SHIMS (MAX 4 PER BOLT)

NOTES

1. SEE STANDARD SPECIFICATIONS & SPECIAL PROVISIONS FOR ADDITIONAL INFORMATION.
2. ALL DIMENSIONS ARE IN MILLIMETRES UNLESS OTHERWISE NOTED.

NOT TO SCALE


BRITISH COLUMBIA | Ministry of Transportation and Infrastructure

No.	Revision	Date
F		
E		
D		
C		
B	GENERAL REVISIONS	APR 17
A	GENERAL REVISIONS	AUG 94

BREAKAWAY LEG AND STUB POST INSTALLATION DETAILS


Date Approved
30/09/93 E.L. (Signature on File)
Chief Highway Engineer

SPECIFICATION DRAWING No.
SP635–3.4.3

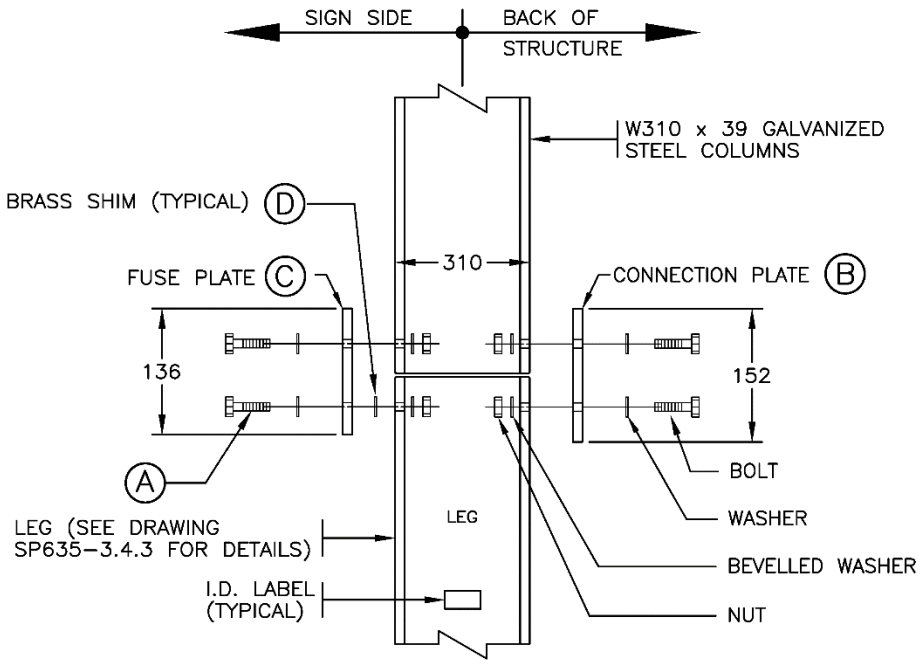


ASSEMBLY DETAIL
SIDE VIEW

TORQUE 3/4"ø x 2" LONG BOLTS TO 262ft. lbs.

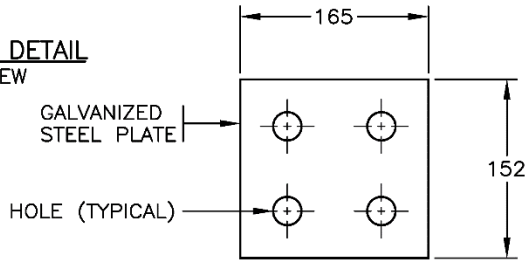

CONNECTION PLATE
(ITEM B)

FUSE JOINT KIT		
ITEM	QUANTITY	DESCRIPTION
A	8	3/4"ø x 2" LONG GALVANIZED BOLT, NUT, WASHER AND BEVELLED WASHER.
B	1	CONNECTION PLATE
C	1	FUSE PLATE
D	2	BRASS SHIMS

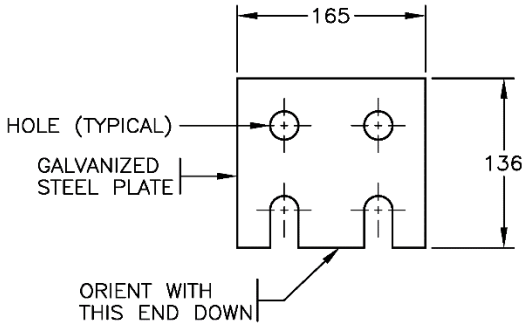

FUSE PLATE
(ITEM C)

NOTES

1. SEE STANDARD SPECIFICATIONS & SPECIAL PROVISIONS FOR ADDITIONAL INFORMATION.
2. ALL DIMENSIONS ARE IN MILLIMETRES UNLESS OTHERWISE NOTED.

NOT TO SCALE


BRITISH COLUMBIA | Ministry of Transportation and Infrastructure

No.	Revision	Date
F		
E		
D		
C		
B	GENERAL REVISIONS	APR 17
A	GENERAL REVISIONS	AUG 94


BREAKAWAY FUSE JOINT INSTALLATION DETAILS

Date Approved
30/09/93 E.L. (Signature on File)
Chief Highway Engineer

SPECIFICATION DRAWING No.
SP635-3.4.4

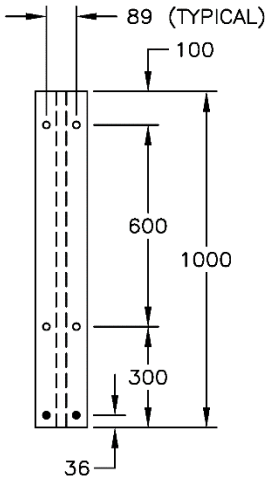

SUPPORT COLUMN FOR SHEET ALUMINUM SIGNS

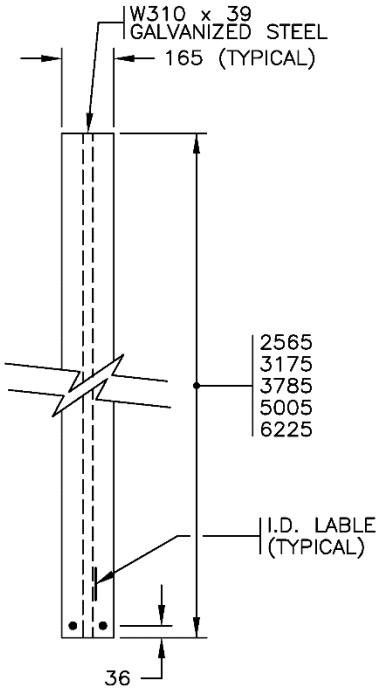

SUPPORT COLUMN FOR EXTRUDED ALUMINUM SIGNS

COLUMNS	
LENGTH	MASS (kg)
1000	39
2565	100
3175	124
3785	148
5005	195
6225	243

NOTES

1. SEE STANDARD SPECIFICATIONS & SPECIAL PROVISIONS FOR ADDITIONAL INFORMATION.
2. HOLES SHOWN ● ARE FOR FUSE OR CONNECTION PLATES ONLY
3. HOLES SHOWN O ARE FOR BATTENS ONLY
4. ALL DIMENSIONS ARE IN MILLIMETRES UNLESS OTHERWISE NOTED.

NOT TO SCALE

BRITISH COLUMBIA | Ministry of Transportation and Infrastructure

No.	Revision	Date
E		
D		
C		
B	REMOVED PLYWOOD SIGN DETAILS NEW DRAWING NUMBER	APR 20
A	GENERAL REVISION	AUG 94

BREAKAWAY SIGN SUPPORT COLUMN DETAILS


Date Approved

30/09/93 E.L. (Signature on File)


Chief Highway Engineer

SPECIFICATION DRAWING No.

SP635–3.4.5

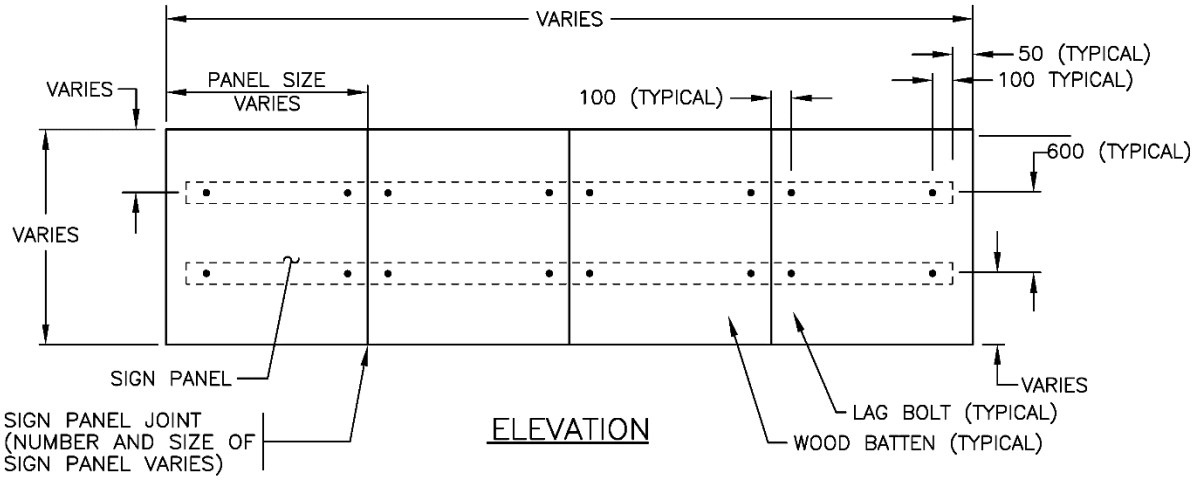

ELEVATION

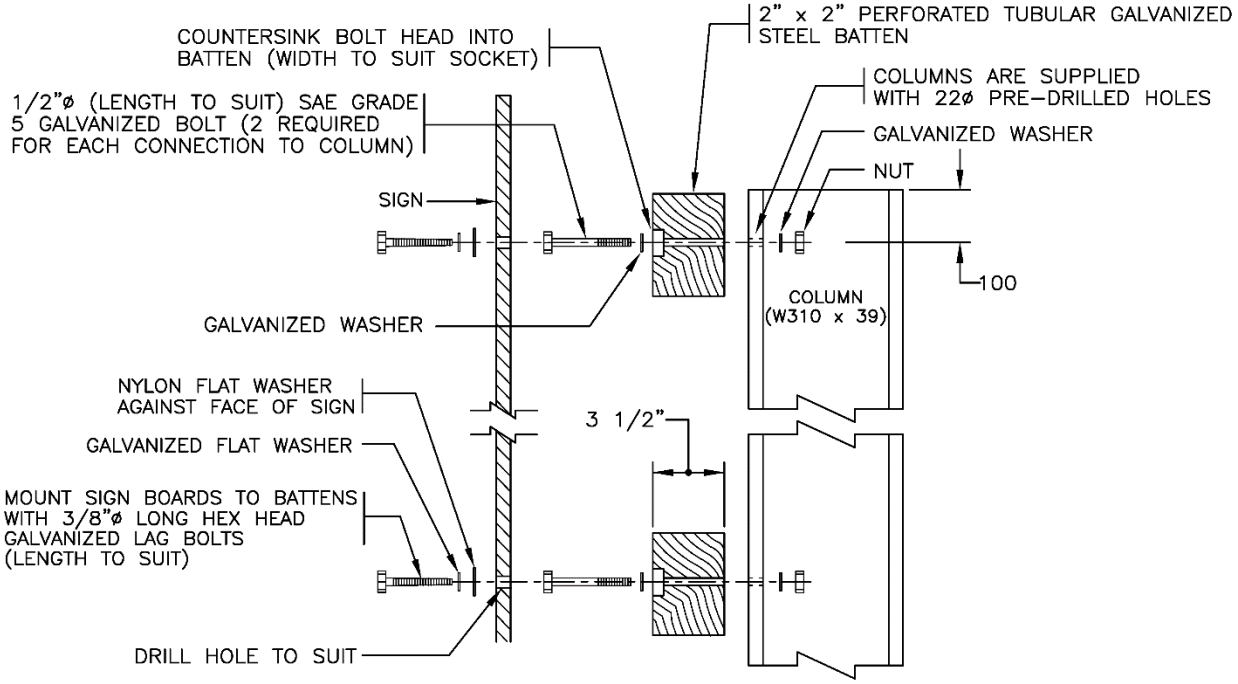

SIDE VIEW

NOTES

1. SEE STANDARD SPECIFICATIONS & SPECIAL PROVISIONS FOR ADDITIONAL INFORMATION.
2. ALL DIMENSIONS ARE IN MILLIMETRES UNLESS OTHERWISE NOTED.

NOT TO SCALE

BRITISH COLUMBIA | Ministry of Transportation and Infrastructure

No.	Revision	Date
E		
D		
C	REMOVED PLYWOOD SIGN DETAILS NEW DRAWING NUMBER	APR 20
B	GENERAL REVISIONS	APR 05
A	GENERAL REVISIONS	AUG 94

SHEET ALUMINUM SIGN MOUNTING DETAILS ON BREAKAWAY SIGN STRUCTURE


Date Approved

30/09/93 E.L. (Signature on File)

Chief Highway Engineer

SPECIFICATION DRAWING No.

SP635-3.4.6

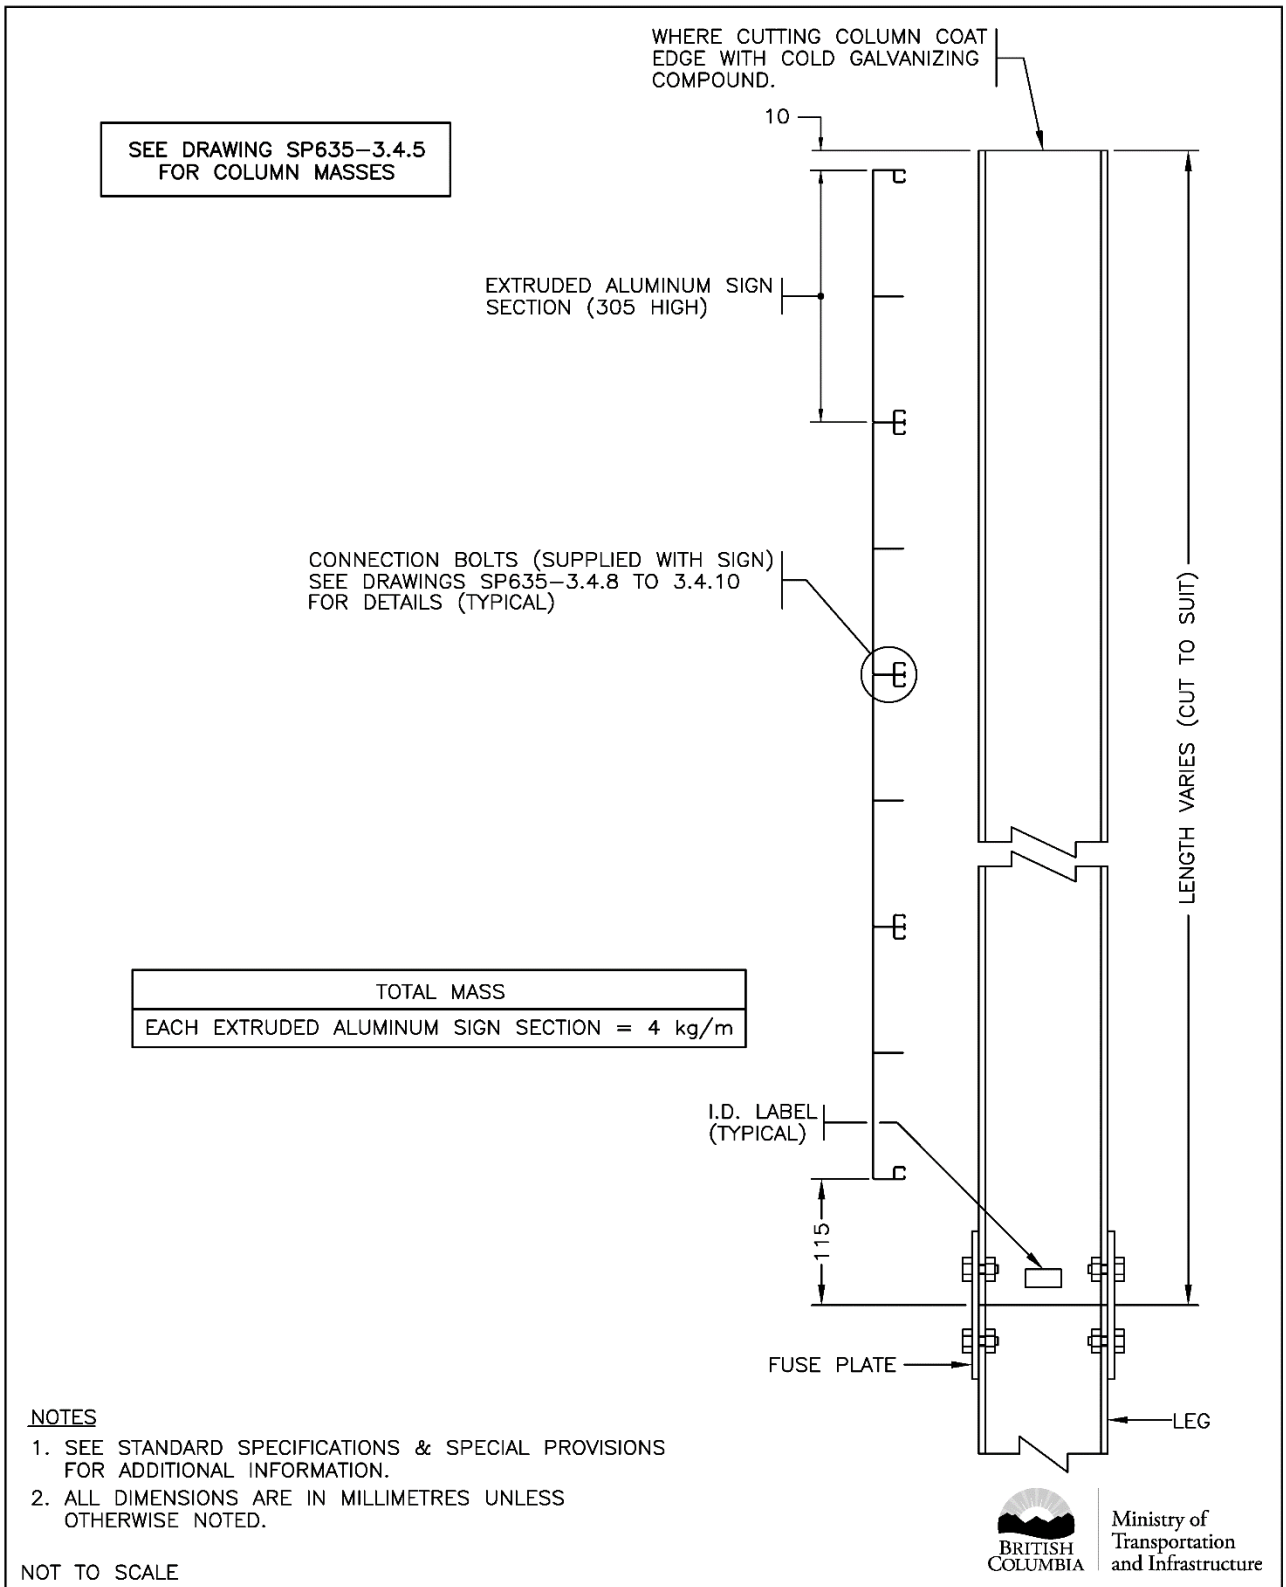

NOTES

1. SEE STANDARD SPECIFICATIONS & SPECIAL PROVISIONS FOR ADDITIONAL INFORMATION.
2. ALL DIMENSIONS ARE IN MILLIMETRES UNLESS OTHERWISE NOTED.

NOT TO SCALE

BRITISH COLUMBIA Ministry of Transportation and Infrastructure

No.	Revision	Date
E		
D		
C	GENERAL REVISIONS NEW DRAWING NUMBER	APR 20
B	GENERAL REVISIONS	APR 17
A	NEW DRAWING NUMBER	OCT 97

EXTRUDED ALUMINUM SIGN MOUNTING DETAILS ON BREAKAWAY SIGN STRUCTURE


Date Approved

18/11/94 E.L. (Signature on File)

Chief Highway Engineer

SPECIFICATION DRAWING No.

SP635–3.4.7

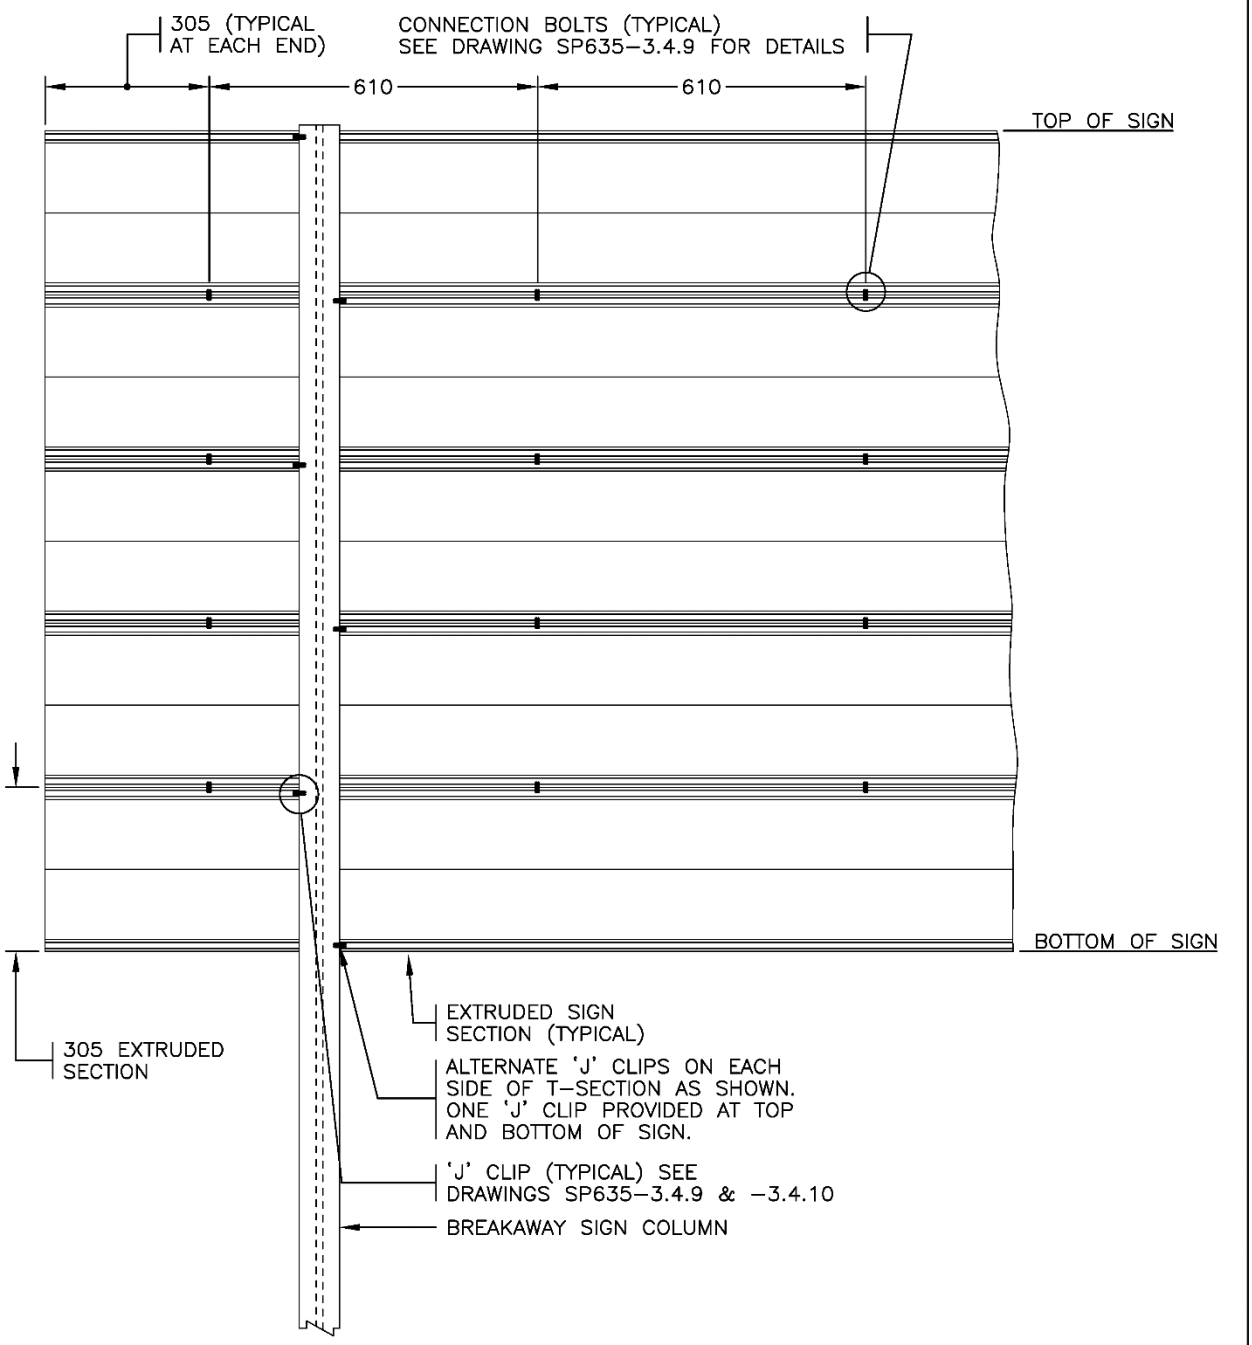

REAR VIEW OF SIGN

SEE DRAWING SP635–3.4.7 FOR NOTES AND ADDITIONAL DETAILS.

NOT TO SCALE

BRITISH COLUMBIA | Ministry of Transportation and Infrastructure

No.	Revision	Date
E		
D	GENERAL REVISIONS NEW DRAWING NUMBER	APR 20
C	GENERAL REVISIONS	APR 17
B	NEW DRAWING NUMBER	OCT 97
A	END HOLE SPACING REVISED	AUG 95

EXTRUDED ALUMINUM SIGN MOUNTING DETAILS ON BREAKAWAY SIGN STRUCTURE

Date Approved


18/11/94 E.L. (Signature on File)

Chief Highway Engineer

SPECIFICATION DRAWING No.

SP635–3.4.8

9

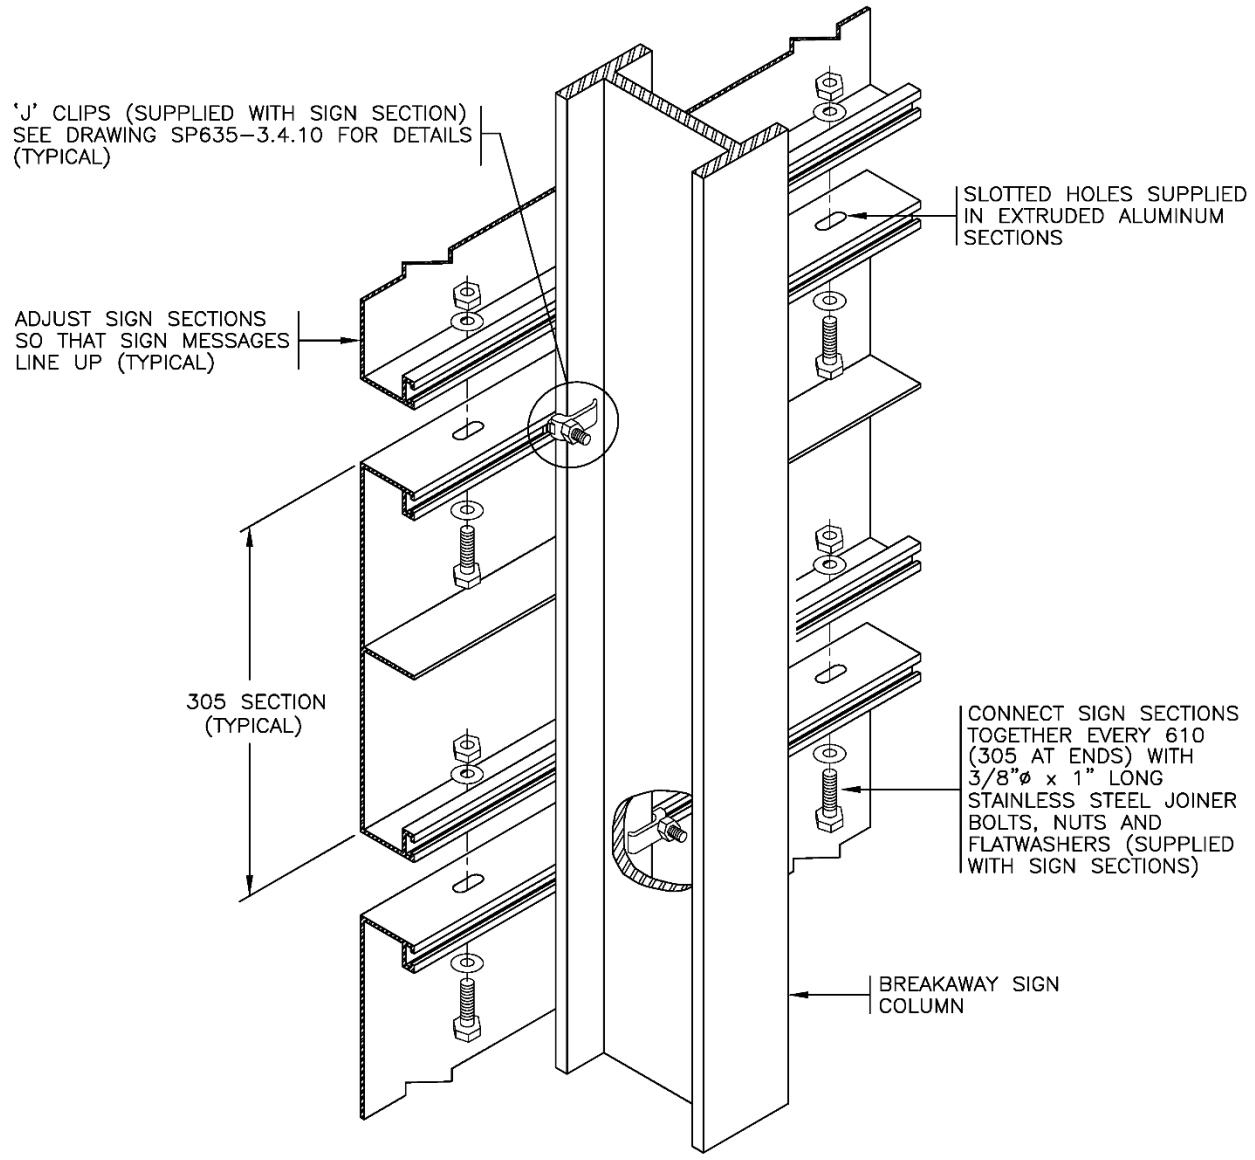

ASSEMBLY VIEW

TORQUE JOINER BOLTS AND 'J' CLIPS TO 19 ft. lbs.

SEE DRAWING SP635-3.4.7 FOR NOTES AND ADDITIONAL DETAILS.

NOT TO SCALE

BRITISH COLUMBIA Ministry of Transportation and Infrastructure

No.	Revision	Date
E		
D	GENERAL REVISIONS NEW DRAWING NUMBER	APR 20
C	GENERAL REVISIONS	APR 17
B	NEW DRAWING NUMBER	OCT 97
A	END HOLE SPACING REVISED	AUG 95

EXTRUDED ALUMINUM SIGN MOUNTING DETAILS ON BREAKAWAY SIGN STRUCTURE


Date Approved

18/11/94 E.L. (Signature on File)

Chief Highway Engineer

SPECIFICATION DRAWING No.

SP635-3.4.9

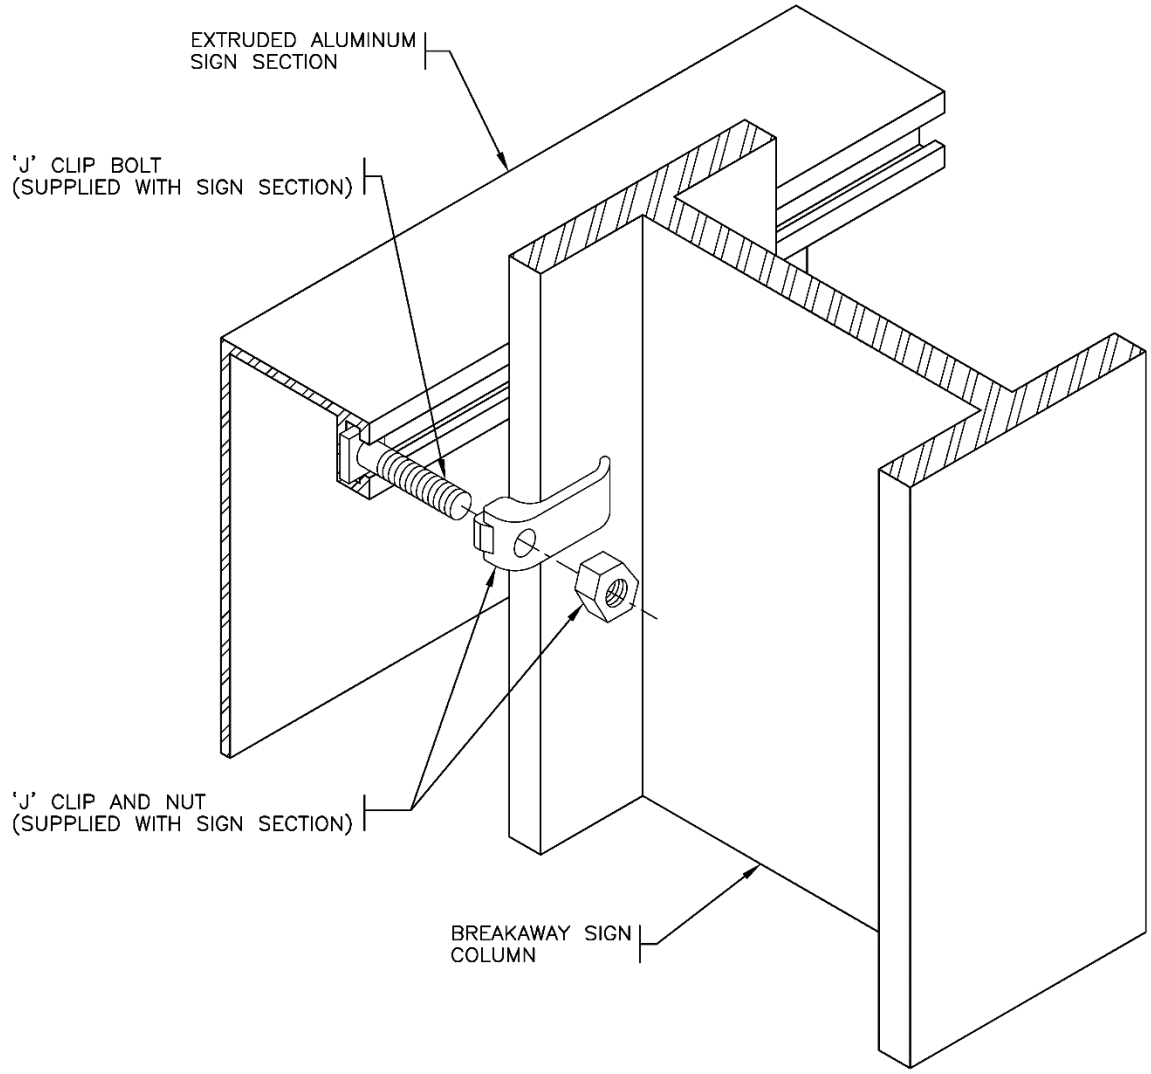

ASSEMBLY VIEW

TORQUE JOINER BOLTS AND 'J' CLIPS TO 19 ft. lbs.

SEE DRAWING SP635–3.4.7 FOR NOTES AND ADDITIONAL DETAILS.

NOT TO SCALE

BRITISH COLUMBIA | Ministry of Transportation and Infrastructure

No.	Revision	Date
E		
D		
C	GENERAL REVISIONS NEW DRAWING NUMBER	APR 20
B	GENERAL REVISIONS	APR 17
A	NEW DRAWING NUMBER	OCT 97

EXTRUDED ALUMINUM SIGN MOUNTING DETAILS ON BREAKAWAY SIGN STRUCTURE

Date Approved


18/11/94 E.L. (Signature on File)

Chief Highway Engineer

SPECIFICATION DRAWING No.

SP635–3.4.10

SIGN HEIGHT	NUMBER OF BOLTS
UP TO 750 HIGH	2
751 TO 1260 HIGH	3

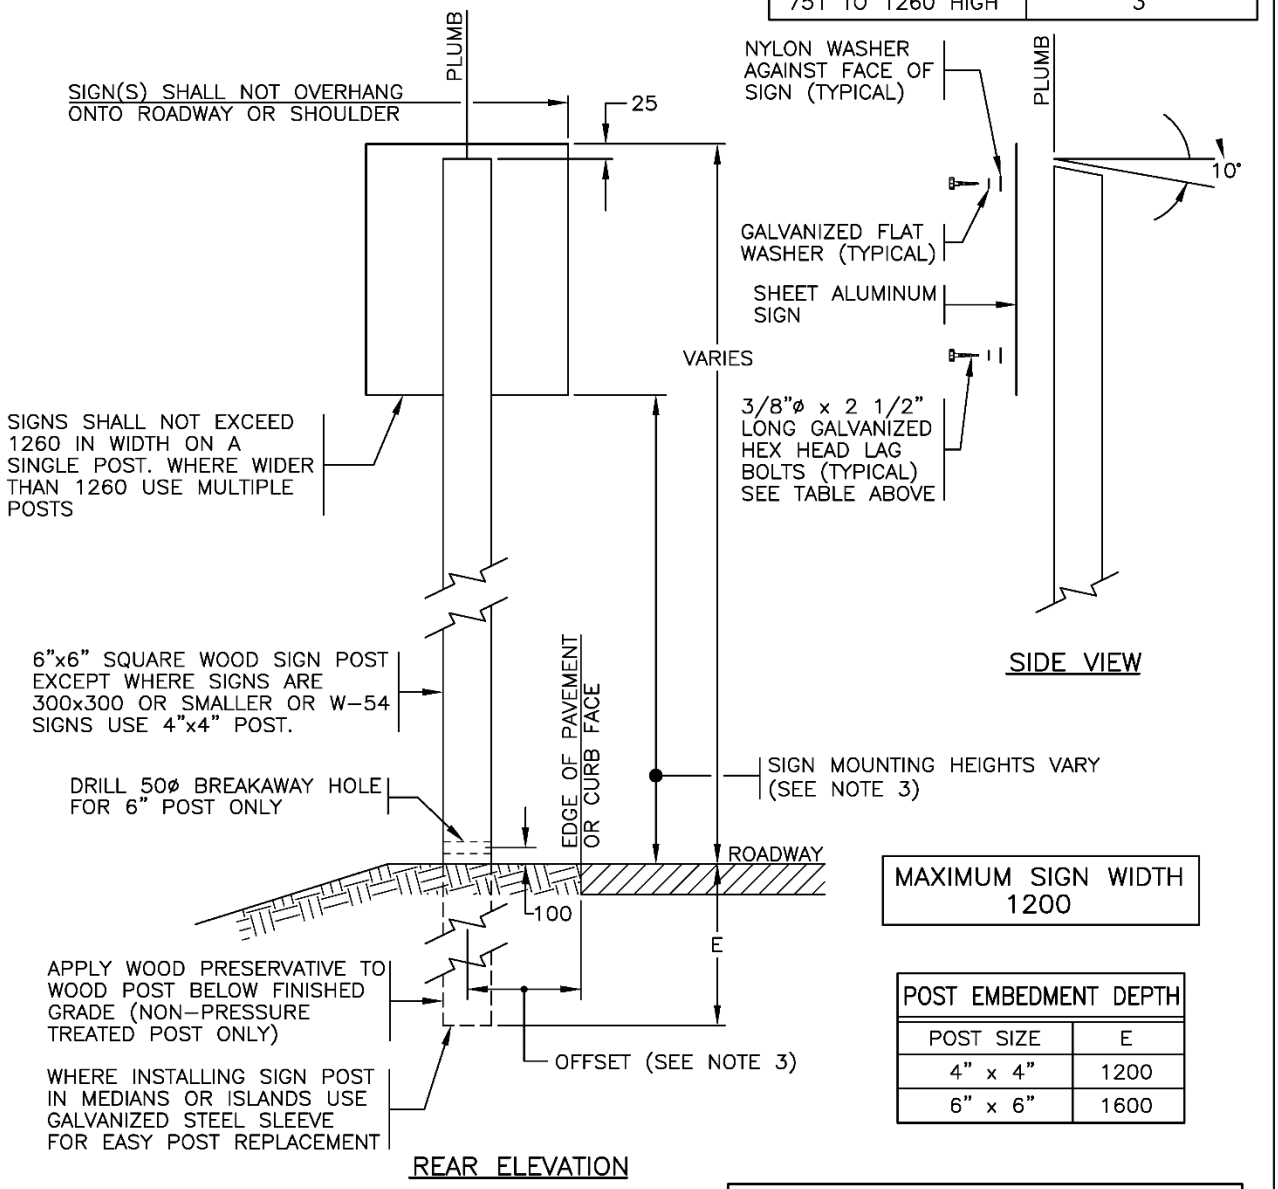

MAXIMUM SIGN WIDTH
1200

POST EMBEDMENT DEPTH	
POST SIZE	E
4" x 4"	1200
6" x 6"	1600

REFER TO MINISTRY ELECTRICAL & TRAFFIC ENGINEERING MANUAL FOR SIGN STRUCTURE LOADING TABLE

NOTES

1. SEE STANDARD SPECIFICATIONS & SPECIAL PROVISIONS FOR ADDITIONAL INFORMATION.
2. ALL DIMENSIONS ARE IN MILLIMETRES UNLESS OTHERWISE NOTED.
3. MOUNTING HEIGHTS & OFFSETS SHALL FALL WITHIN THE RANGES NOTED IN THE MINISTRY MANUAL OF STANDARD TRAFFIC SIGNS & PAVEMENT MARKINGS.

NOT TO SCALE

BRITISH COLUMBIA Ministry of Transportation and Infrastructure

No.	Revision	Date
H	REMOVED PLYWOOD SIGN DETAILS	APR 20
G	GENERAL REVISIONS	APR 17
F	REF. TO NON-PRESSURE TREATED POSTS	APR 05
E	MOUNTING HEIGHTS & OFFSETS REFERED THE MINISTRY MANUAL OF STANDARD TRAFFIC SIGNS	NOV 98
D	PAINTING NOTE REVISED	NOV 98

SINGLE WOOD POST SIGN STRUCTURE INSTALLATION DETAILS


Date Approved

30/09/93 E.L. (Signature on File)

Chief Highway Engineer

SPECIFICATION DRAWING No.

SP635-3.5.1

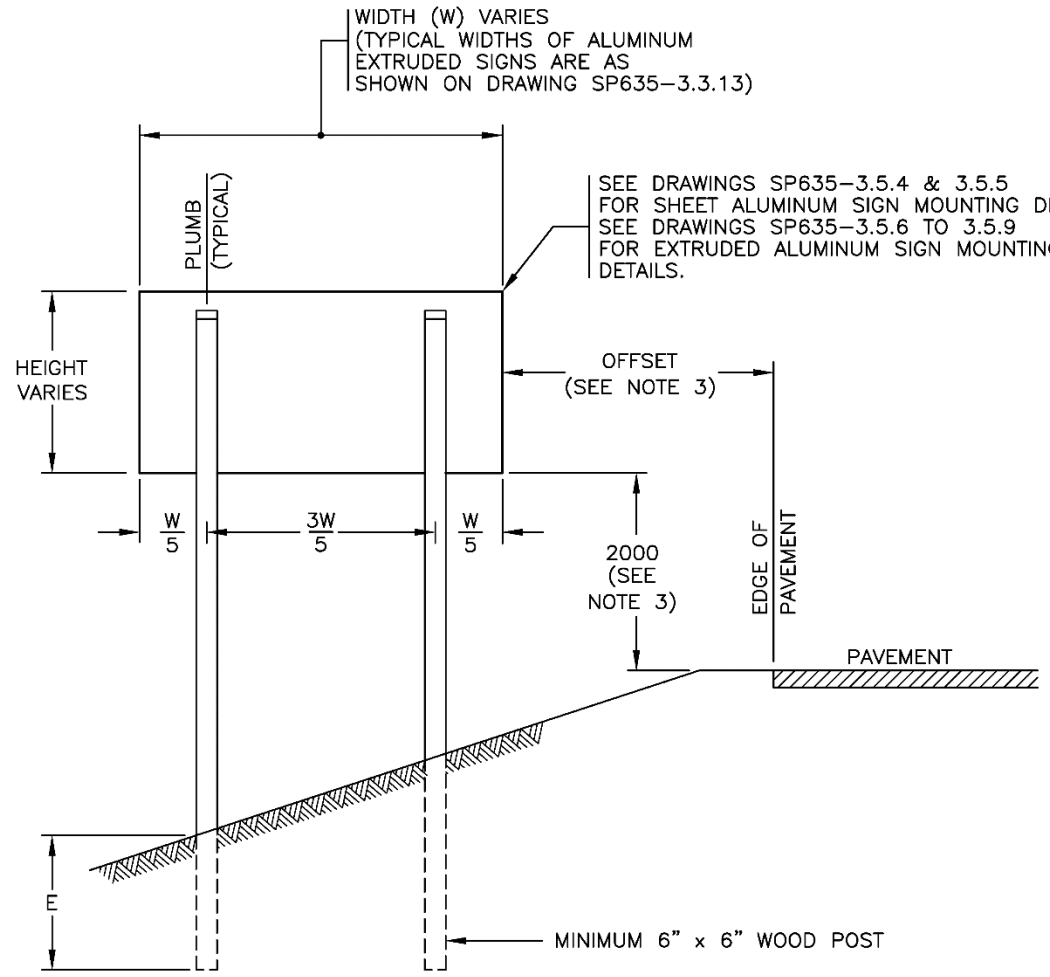

REAR ELEVATION

EMBEDMENT DEPTH	
POST SIZE	E
6" x 6"	1600
8" x 8"	2000
10" x 10"	2200

REFER TO MINISTRY ELECTRICAL & TRAFFIC ENGINEERING MANUAL FOR SIGN STRUCTURE LOADING TABLE

NOTES

1. SEE STANDARD SPECIFICATIONS & SPECIAL PROVISIONS FOR ADDITIONAL INFORMATION.
2. ALL DIMENSIONS ARE IN MILLIMETRES UNLESS OTHERWISE NOTED.
3. MOUNTING HEIGHTS & OFFSETS SHALL FALL WITHIN THE RANGES NOTED IN THE MINISTRY MANUAL OF STANDARD TRAFFIC SIGNS & PAVEMENT MARKINGS.

NOT TO SCALE

BRITISH COLUMBIA Ministry of Transportation and Infrastructure

No.	Revision	Date
G	REMOVED PLYWOOD SIGN DETAILS	APR 20
F	GENERAL REVISIONS	APR 17
E	SHEET ALUMINUM SIGN ADDED	APR 05
D	MOUNTING HEIGHTS & OFFSETS REFERED THE MINISTRY MANUAL OF STANDARD TRAFFIC SIGNS	NOV 98
C	LOADING TABLE REFERENCE NOTE REVISED	AUG 96

WOOD POST SIGN STRUCTURE INSTALLATION DETAILS (TWO POST)


Date Approved

30/09/93 E.L. (Signature on File)

Chief Highway Engineer

SPECIFICATION DRAWING No.

SP635–3.5.2

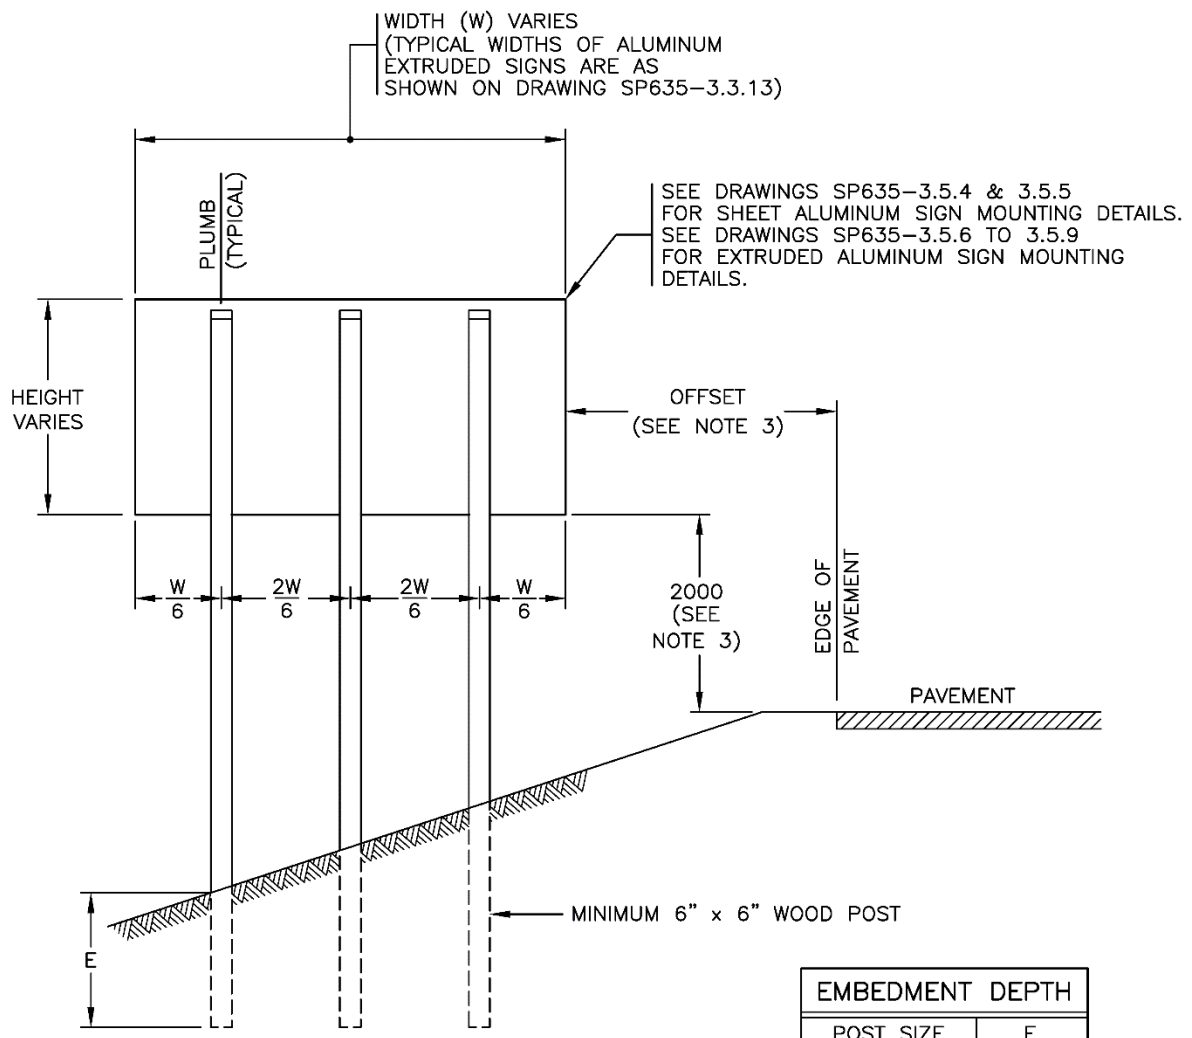

REAR ELEVATION

EMBEDMENT DEPTH	
POST SIZE	E
6" x 6"	1600
8" x 8"	2000
10" x 10"	2200

REFER TO MINISTRY ELECTRICAL & TRAFFIC ENGINEERING MANUAL FOR SIGN STRUCTURE LOADING TABLE

NOTES

1. SEE STANDARD SPECIFICATIONS & SPECIAL PROVISIONS FOR ADDITIONAL INFORMATION.
2. ALL DIMENSIONS ARE IN MILLIMETRES UNLESS OTHERWISE NOTED.
3. MOUNTING HEIGHTS & OFFSETS SHALL FALL WITHIN THE RANGES NOTED IN THE MINISTRY MANUAL OF STANDARD TRAFFIC SIGNS & PAVEMENT MARKINGS.

BRITISH COLUMBIA Ministry of Transportation and Infrastructure

NOT TO SCALE

No.	Revision	Date
G	REMOVED PLYWOOD SIGN DETAILS	APR 20
F	GENERAL REVISIONS	APR 17
E	SHEET ALUMINUM SIGN ADDED	APR 05
D	MOUNTING HEIGHTS & OFFSETS REFERED THE MINISTRY MANUAL OF STANDARD TRAFFIC SIGNS	NOV 98
C	LOADING TABLE REFERENCE NOTE REVISED	AUG 96

WOOD POST SIGN STRUCTURE INSTALLATION DETAILS (THREE POST)


Date Approved

30/09/93 E.L. (Signature on File)

Chief Highway Engineer

SPECIFICATION DRAWING No.

SP635–3.5.3

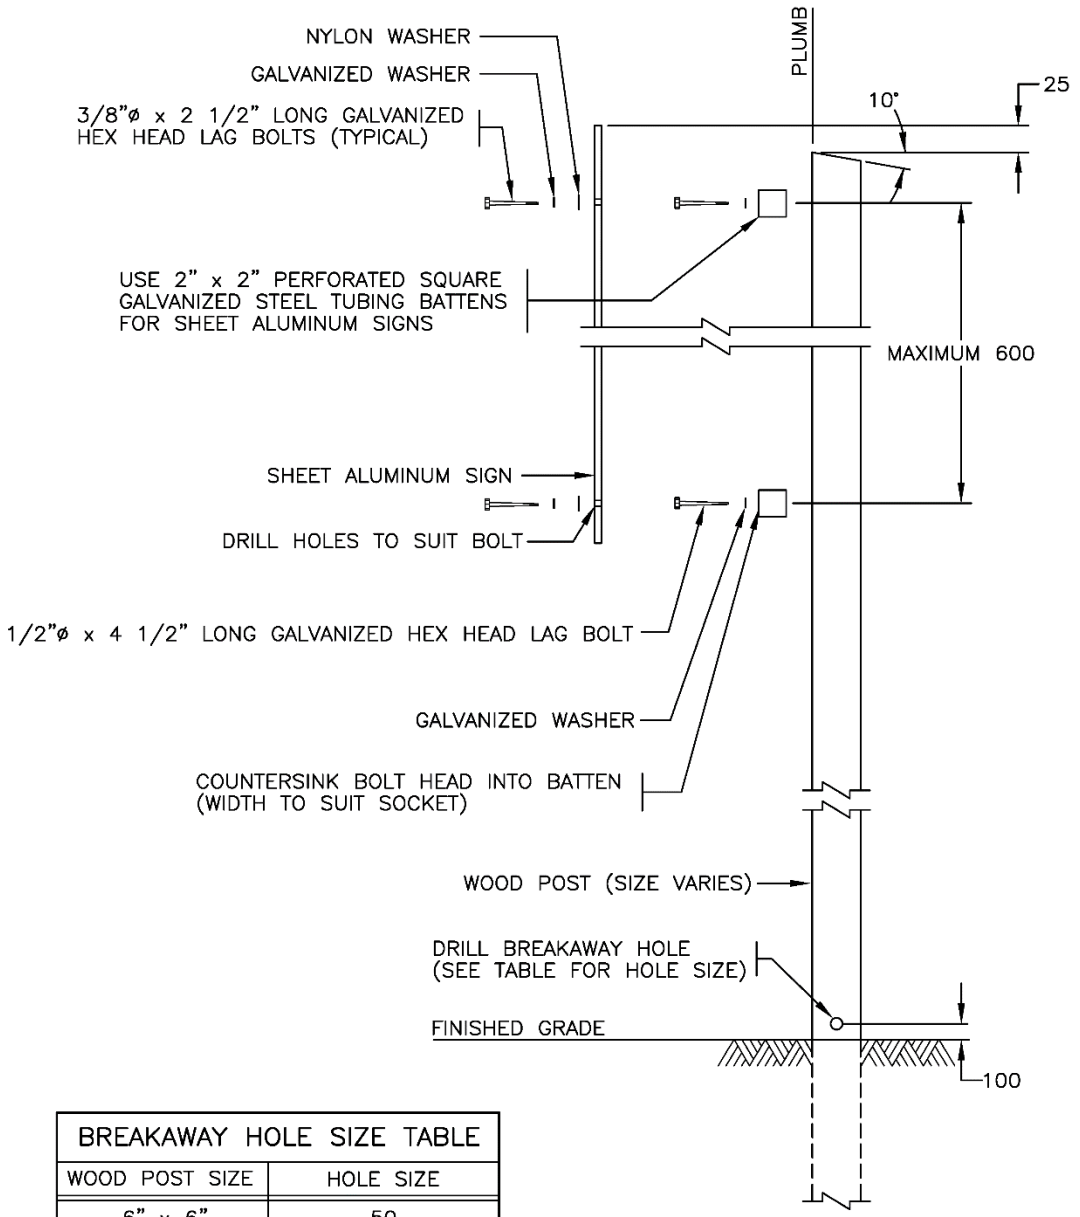

BREAKAWAY HOLE SIZE TABLE	
WOOD POST SIZE	HOLE SIZE
6" x 6"	50
8" x 8"	62
10" x 10"	75

NOTES

1. SEE STANDARD SPECIFICATIONS & SPECIAL PROVISIONS FOR ADDITIONAL INFORMATION.
2. ALL DIMENSIONS ARE IN MILLIMETRES UNLESS OTHERWISE NOTED

NOT TO SCALE

BRITISH COLUMBIA Ministry of Transportation and Infrastructure

No.	Revision	Date
F		
E	REMOVED PLYWOOD SIGN DETAILS	APR 20
D	GENERAL REVISIONS	APR 17
C	GENERAL REVISION	APR 05
B	ANGLE CUT ADDED TO TOP OF POST	AUG 95
A	GENERAL REVISION	AUG 94

SIGN INSTALLATION DETAILS ON WOOD POSTS (2 & 3 POST STRUCTURES)


Date Approved

30/09/93 E.L. (Signature on File)

Chief Highway Engineer

SPECIFICATION DRAWING No.

SP635-3.5.4

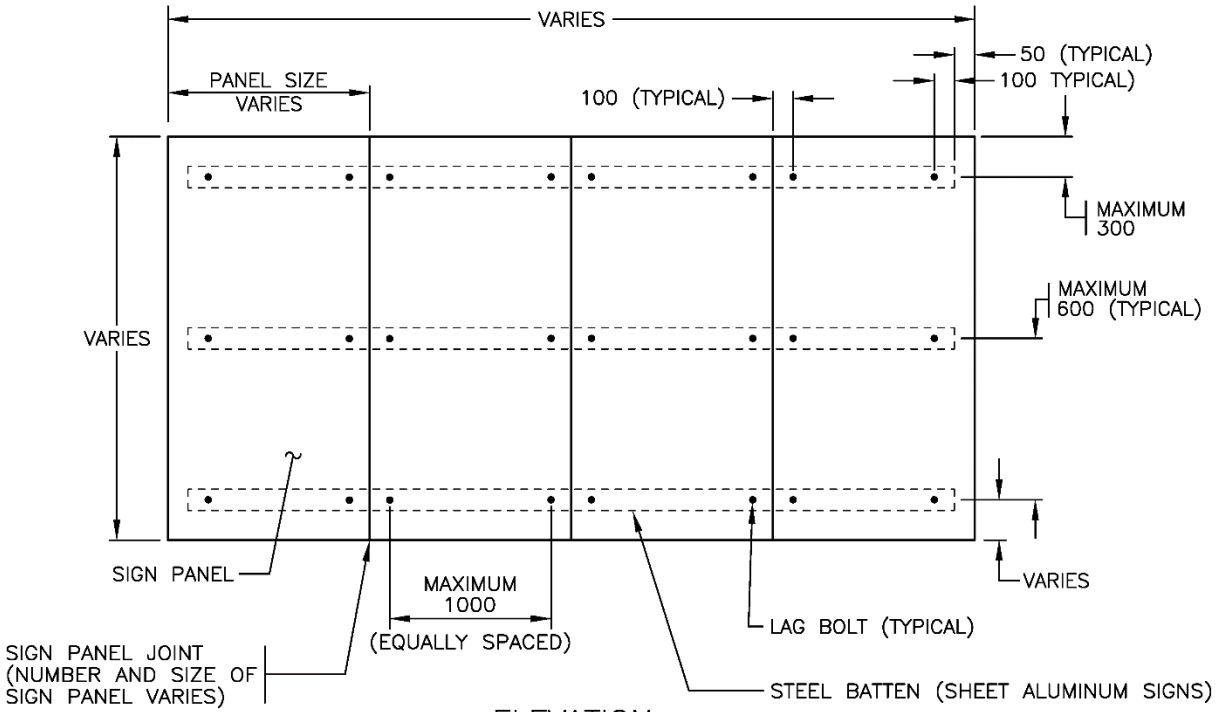

ELEVATION

TOTAL MASS
SIGNBOARD = 10 kg/m^2

NOTES

1. SEE STANDARD SPECIFICATIONS & SPECIAL PROVISIONS FOR ADDITIONAL INFORMATION.
2. ALL DIMENSIONS ARE IN MILLIMETRES UNLESS OTHERWISE NOTED

NOT TO SCALE

BRITISH COLUMBIA | Ministry of Transportation and Infrastructure

No.	Revision	Date
F		
E		
D	PLYWOOD SIGN DETAILS REMOVED	APR 20
C	GENERAL REVISIONS	APR 17
B	SHEET ALUMINUM SIGN ADDED	APR 05
A	GENERAL REVISION	AUG 94

SIGN INSTALLATION DETAILS ON WOOD POSTS


Date Approved

30/09/93 E.L. (Signature on File)

Chief Highway Engineer

SPECIFICATION DRAWING No.

SP635–3.5.5

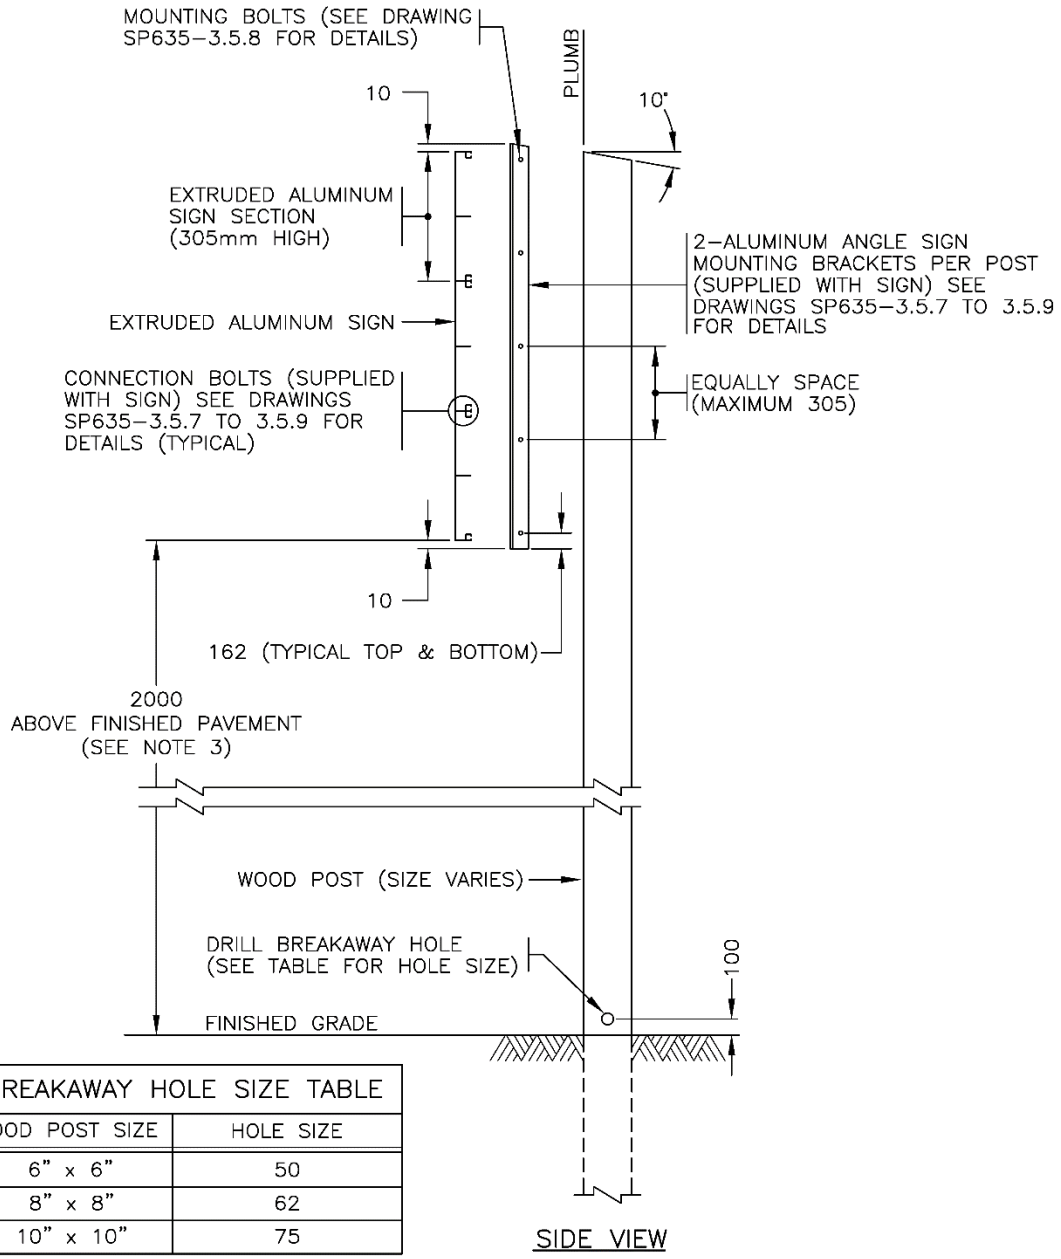

BREAKAWAY HOLE SIZE TABLE	
WOOD POST SIZE	HOLE SIZE
6" x 6"	50
8" x 8"	62
10" x 10"	75

NOTES

1. SEE STANDARD SPECIFICATIONS & SPECIAL PROVISIONS FOR ADDITIONAL INFORMATION.
2. ALL DIMENSIONS ARE IN MILLIMETRES UNLESS OTHERWISE NOTED.
3. MOUNTING HEIGHTS & OFFSETS SHALL FALL WITHIN THE RANGES NOTED IN THE MINISTRY MANUAL OF STANDARD TRAFFIC SIGNS & PAVEMENT MARKINGS.

NOT TO SCALE

TOTAL MASS
EACH EXTRUDED ALUMINUM SIGN SECTION = 4 kg/m


BRITISH COLUMBIA | Ministry of Transportation and Infrastructure

No.	Revision	Date
E		
D		
C	GENERAL REVISIONS	APR 17
B	MOUNTING HEIGHTS & OFFSETS REFERED THE MINISTRY MANUAL OF STANDARD TRAFFIC SIGNS	NOV 98
A	ANGLE CUT ADDED ON TOP OF POST	AUG 95

EXTRUDED ALUMINUM SIGN INSTALLATION DETAILS ON WOOD POSTS

Date: **17/11/94** Approved: **E.L. (Signature on File)**
Chief Highway Engineer

SPECIFICATION DRAWING No.
SP635–3.5.6

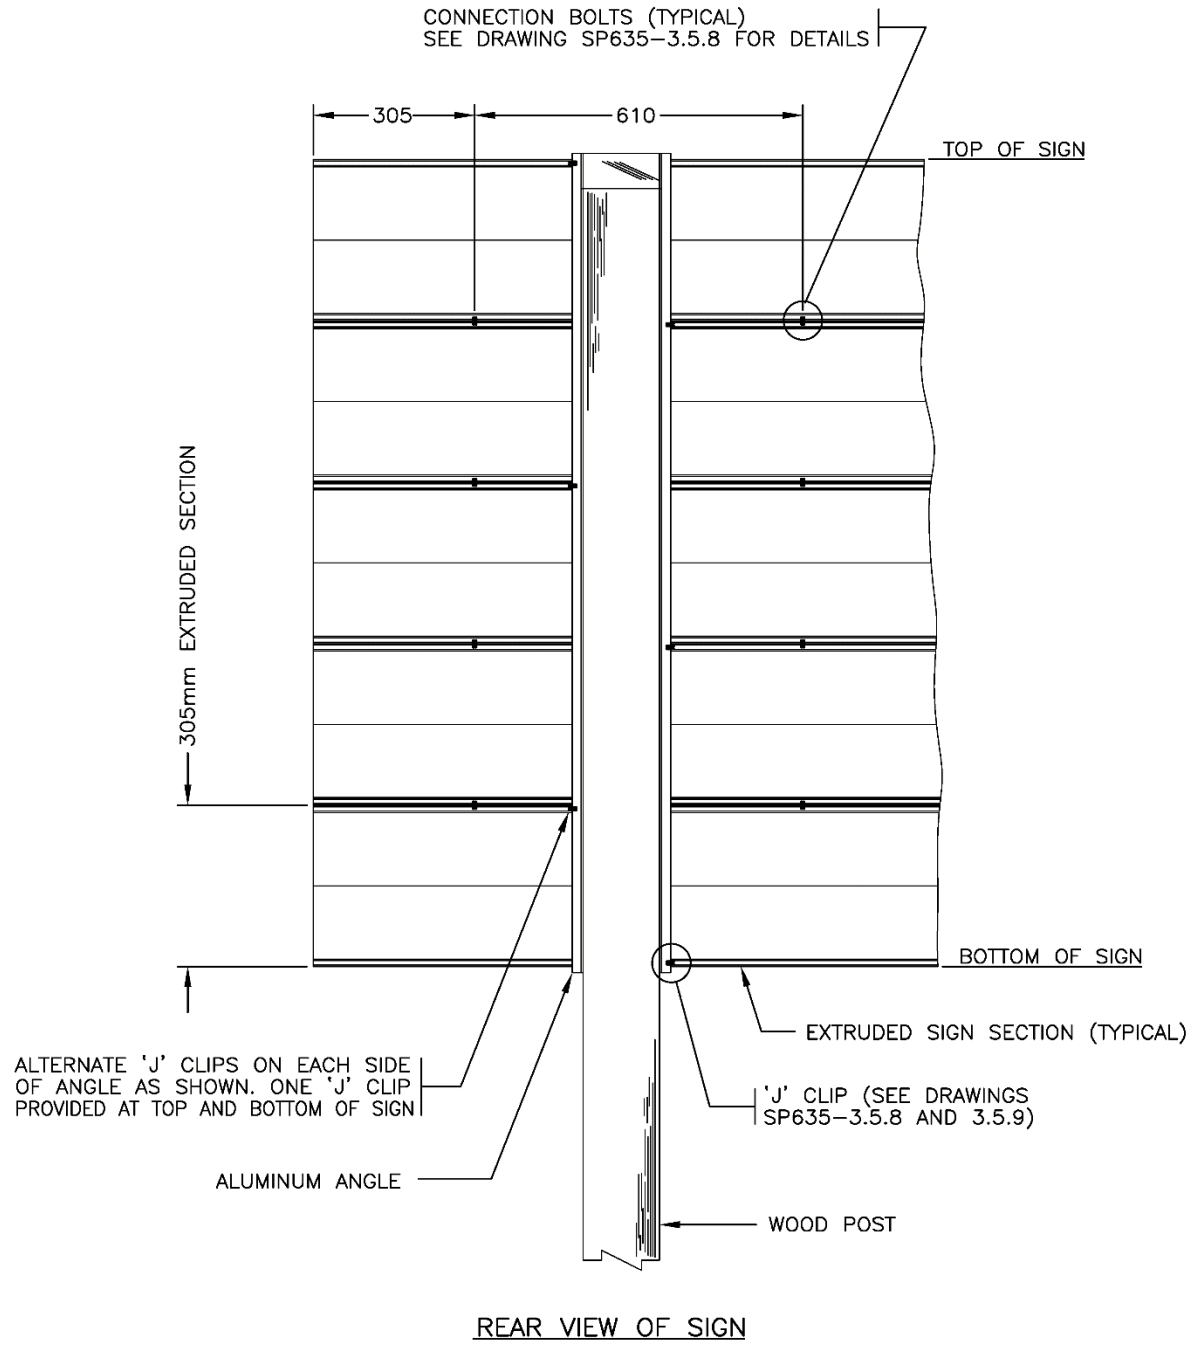

REAR VIEW OF SIGN

SEE DRAWING SP635–3.5.6 FOR NOTES AND ADDITIONAL DETAILS.

SCALE 1:12.5

BRITISH COLUMBIA Ministry of Transportation and Infrastructure

No.	Revision	Date
F		
E		
D		
C		
B	GENERAL REVISIONS	APR 17
A	END HOLE SPACING REVISED	AUG 95

EXTRUDED ALUMINUM SIGN INSTALLATION DETAILS ON WOOD POSTS


Date Approved

18/11/94 E.L. (Signature on File)

Chief Highway Engineer

SPECIFICATION DRAWING No.

SP635–3.5.7

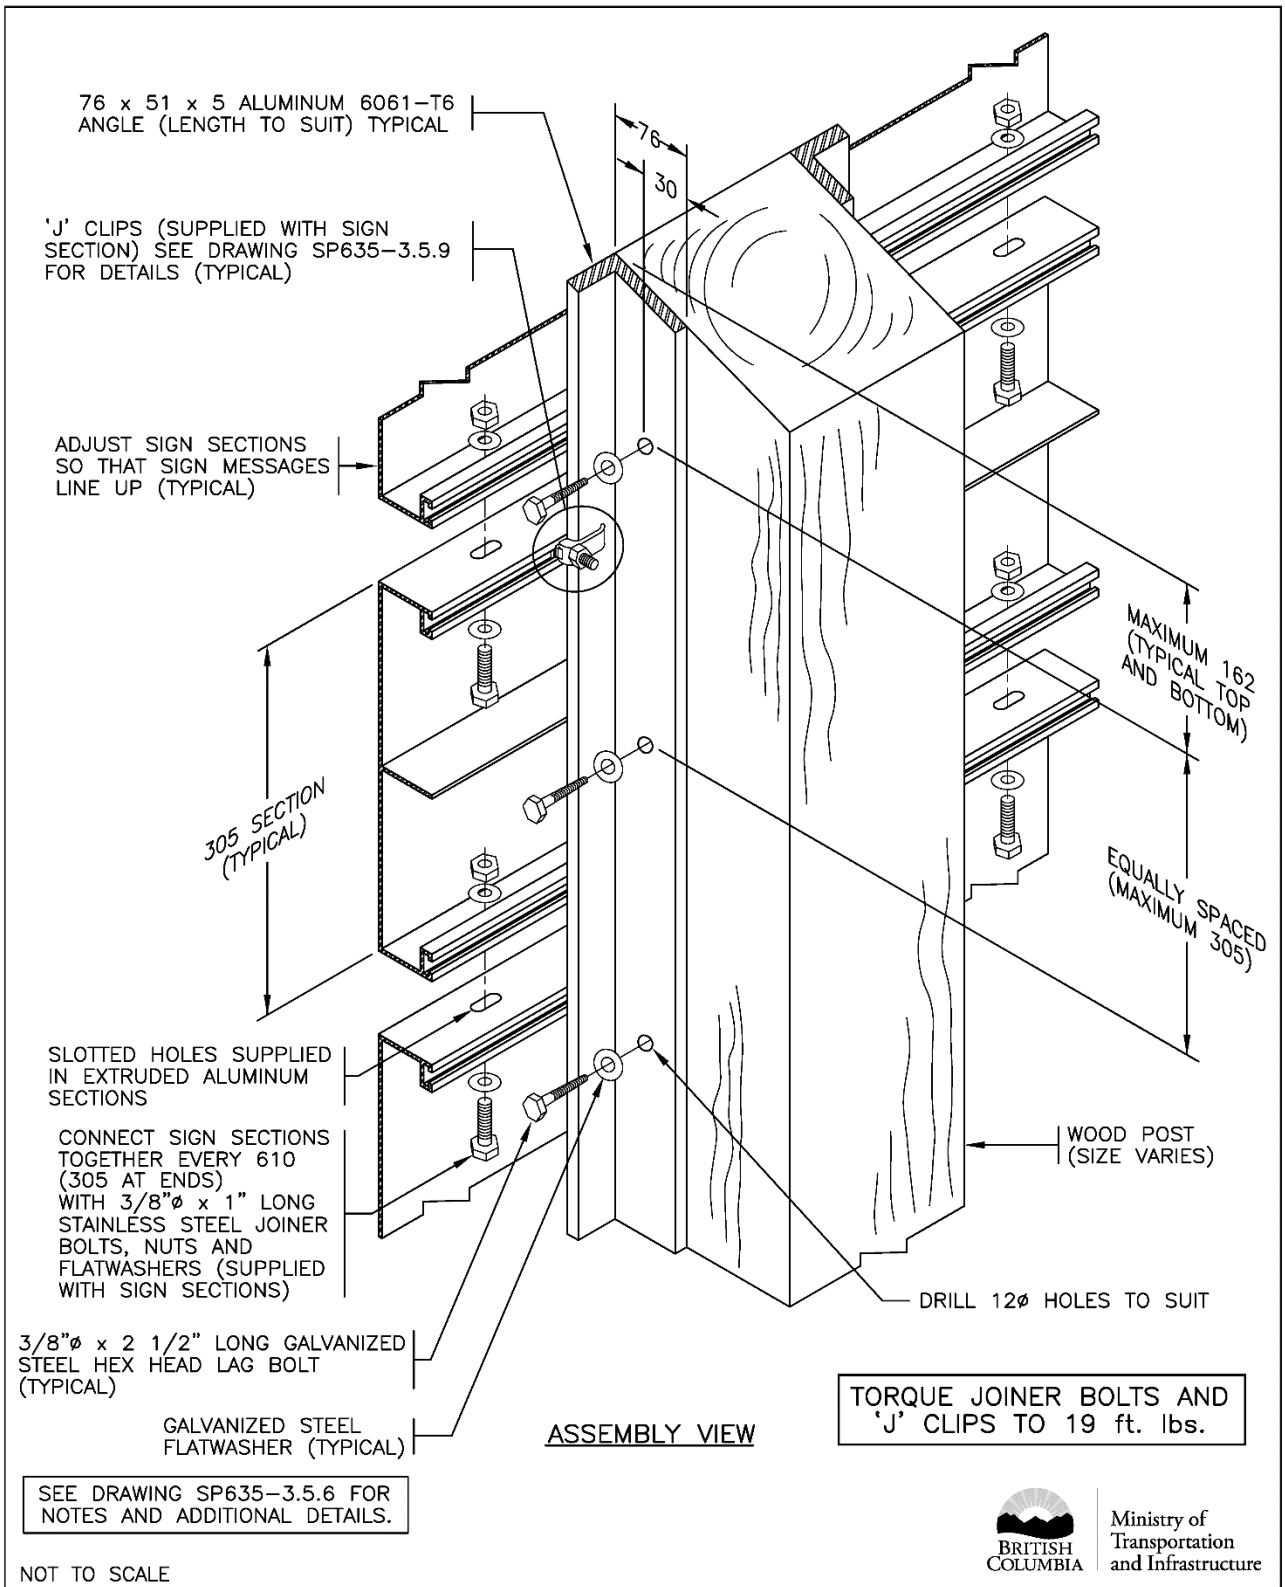

BRITISH COLUMBIA | Ministry of Transportation and Infrastructure

No.	Revision	Date
F		
E		
D		
C		
B	GENERAL REVISIONS	APR 17
A	END HOLE SPACING REVISED & ANGLE CUT ADDED	AUG 95

EXTRUDED ALUMINUM SIGN INSTALLATION DETAILS ON WOOD POST

Date Approved

18/11/94 E.L. (Signature on File)

Chief Highway Engineer

SPECIFICATION DRAWING No.

SP635–3.5.8